
SIMÕES

Arquitetura

& Design de Interiores

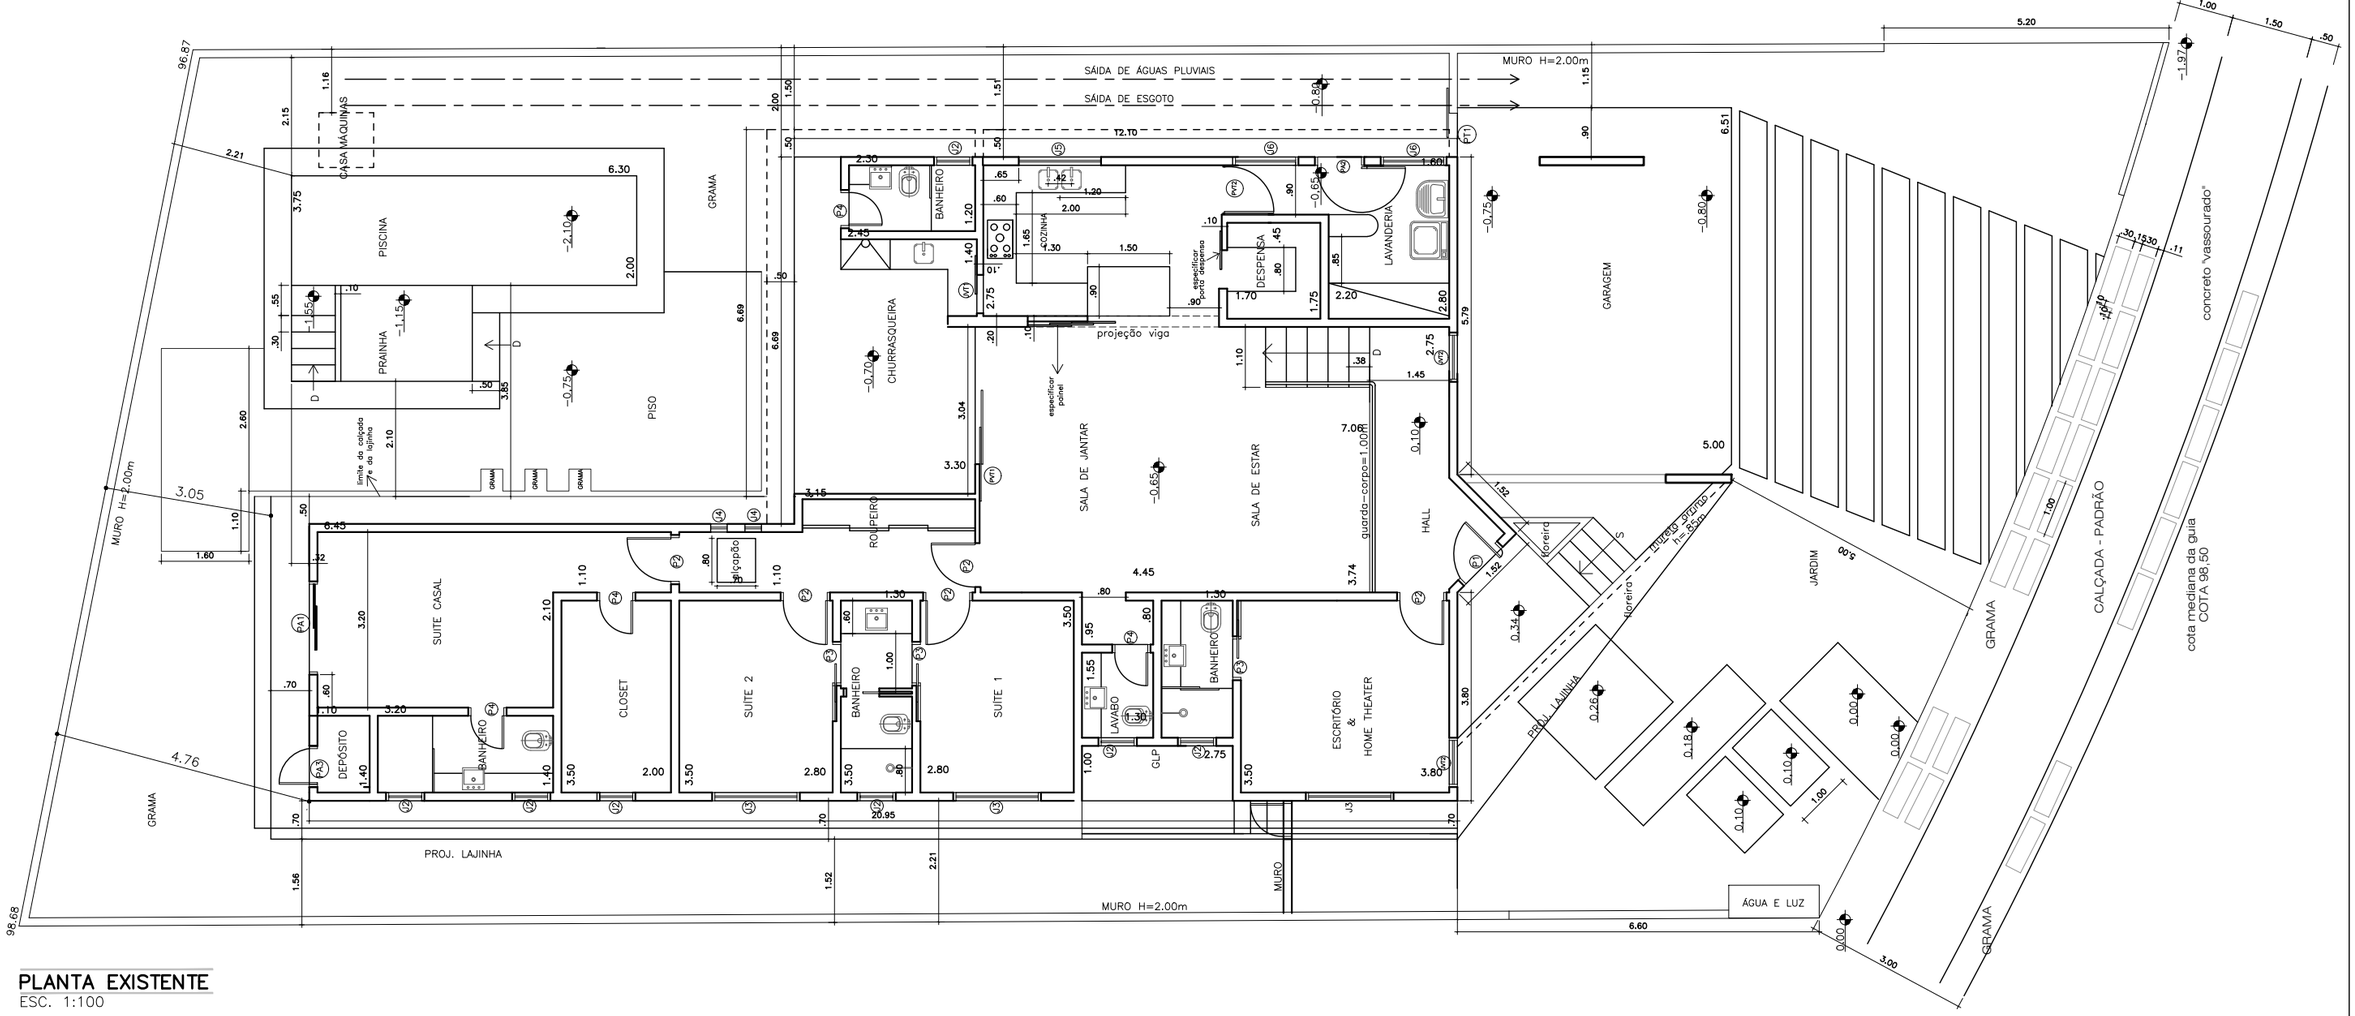

PLANTA EXISTENTE
ESC. 1:100

OBSERVAÇÕES

- COTAS EM METROS;
- COTAS DE NÍVEL EM METROS;
- CONFERIR MEDIDAS, ABERTURAS, NÍVEIS E PRUMOS NO LOCAL;
- MEDIDAS EM COTA PREVALECEM SOBRE O DESENHO;
- ESSA PRANCHA DEVE SER IMPRESSA COLORIDA;
- É RESPONSABILIDADE DO FORNECEDOR MEDIR E AJUSTAR O PROJETO;
- INSTALAR PENDENTES APÓS A INSTALAÇÃO DE MÓVEIS E MARCENARIA;

DATA 08/09/2026 | DESENHO REV00

RESPONSÁVEL FERNANDA SUELLEM SIMÕES LIMA

LOCAL QUADRA B, LOTE 11 – CONDOMÍNIO HEVETIA PARK

ESCALA **INDICADA** | COD. DO PROJETO **0000**

CIDADE INDAIATUBA– SP

FASE EXECUTIVO

FOLHA 01 / 39


FORMATO A3

PROJETO RESIDENCIAL

CLIENTE **KATIA**

ASSUNTO **PLANTA EXISTENTE**

SIMÕES Arquitetura & Design de Interiores
EMAIL: ARQUITETURA@SIMOESARQUITETURA.COM.BR
INSTAGRAM: @SIMOESARQUITETURA

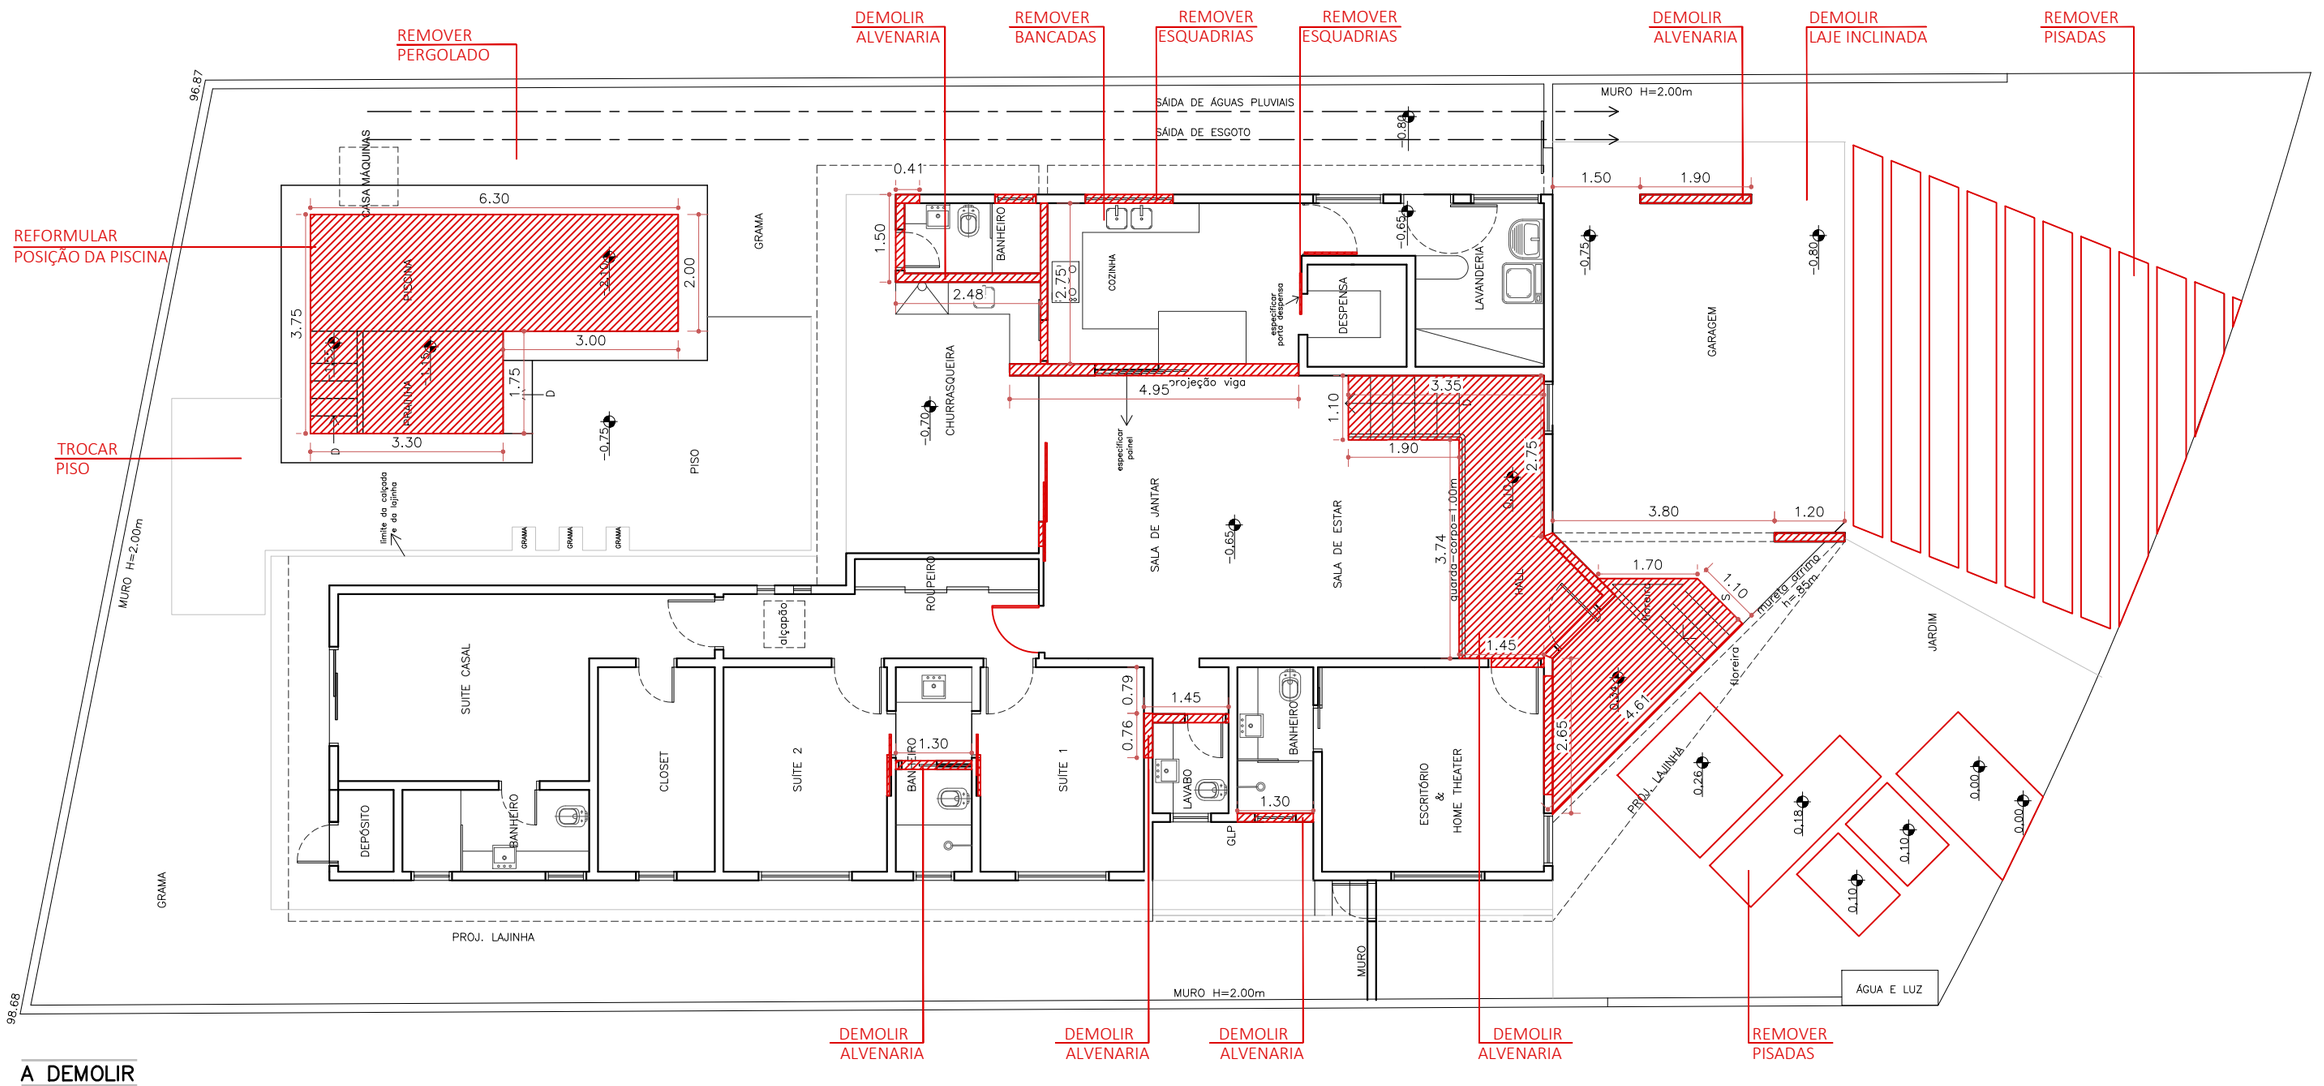

A DEMOLIR
ESC. 1:100

OBSERVAÇÕES

- COTAS EM METROS;
- COTAS DE NÍVEL EM METROS;
- CONFERIR MEDIDAS, ABERTURAS, NÍVEIS E PRUMOS NO LOCAL;
- MEDIDAS EM COTA PREVALECEM SOBRE O DESENHO;
- ESSA PRANCHA DEVE SER IMPRESSA COLORIDA;
- É RESPONSABILIDADE DO FORNECEDOR MEDIR E AJUSTAR O PROJETO;
- INSTALAR PENDENTES APÓS A INSTALAÇÃO DE MÓVEIS E MARCENARIA;

DATA 08/09/2026 | DESENHO REV00

RESPONSÁVEL
FERNANDA SUELLEM SIMÕES LIMA

LOCAL
R. QUADRA B, LOTE 11 – CONDOMÍNIO HEVETIA PARK

ESCALA **INDICADA** | COD. DO PROJETO **0000**

CIDADE
INDAIATUBA– SP

FASE
EXECUTIVO

FOLHA 02/39


FORMATO
A3

PROJETO
RESIDENCIAL

CLIENTE
KATIA

ASSUNTO
A DEMOLIR

SIMÕES Arquitetura & Design de Interiores
EMAIL: ARQUITETURA@SIMOESARQUITETURA.COM.BR
INSTAGRAM: @SIMOESARQUITETURA

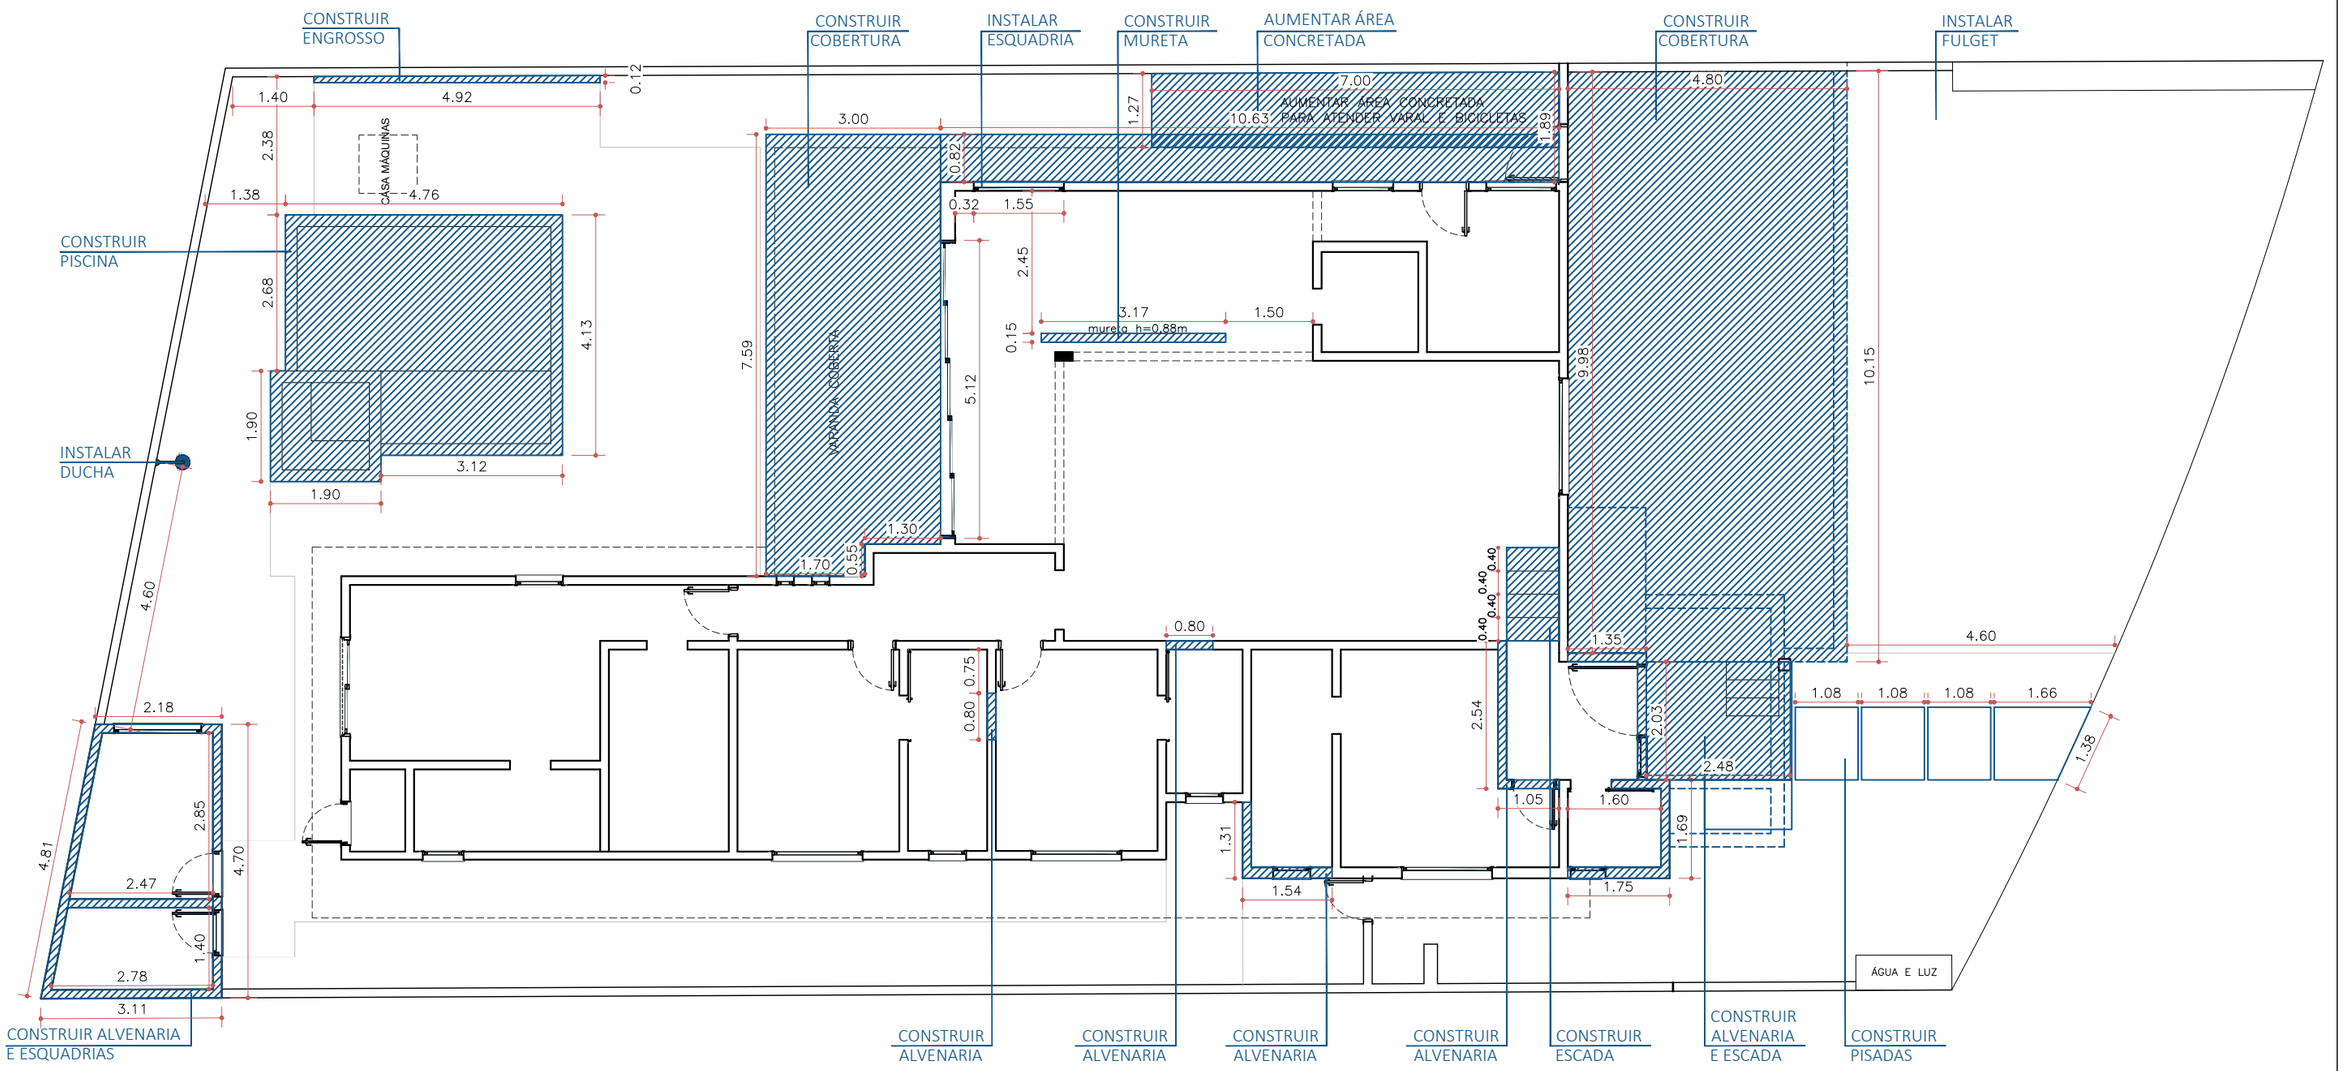

OBSERVAÇÕES

- COTAS EM METROS;
- COTAS DE NÍVEL EM METROS;
- CONFERIR MEDIDAS, ABERTURAS, NÍVEIS E PRUMOS NO LOCAL;
- MEDIDAS EM COTA PREVALECEM SOBRE O DESENHO;
- ESSA PRANCHA DEVE SER IMPRESSA COLORIDA;
- É RESPONSABILIDADE DO FORNECEDOR MEDIR E AJUSTAR O PROJETO;
- INSTALAR PENDENTES APÓS A INSTALAÇÃO DE MÓVEIS E MARCENARIA;

DATA: 08/09/2026 | DESENHO: REV00

RESPONSÁVEL: FERNANDA SUELLEM SIMÕES LIMA

LOCAL: R. QUADRA B, LOTE 11 – CONDOMÍNIO HEVETIA PARK

ESCALA: INDICADA | COD. DO PROJETO: 0000

CIDADE: INDAIATUBA– SP

FASE: EXECUTIVO

FOLHA: 03/39


FORMATO: A3

PROJETO: RESIDENCIAL

CLIENTE: KATIA

ASSUNTO: A CONSTRUIR

SIMÕES Arquitetura & Design de Interiores
EMAIL: ARQUITETURA@SIMOESARQUITETURA.COM.BR
INSTAGRAM: @SIMOESARQUITETURA

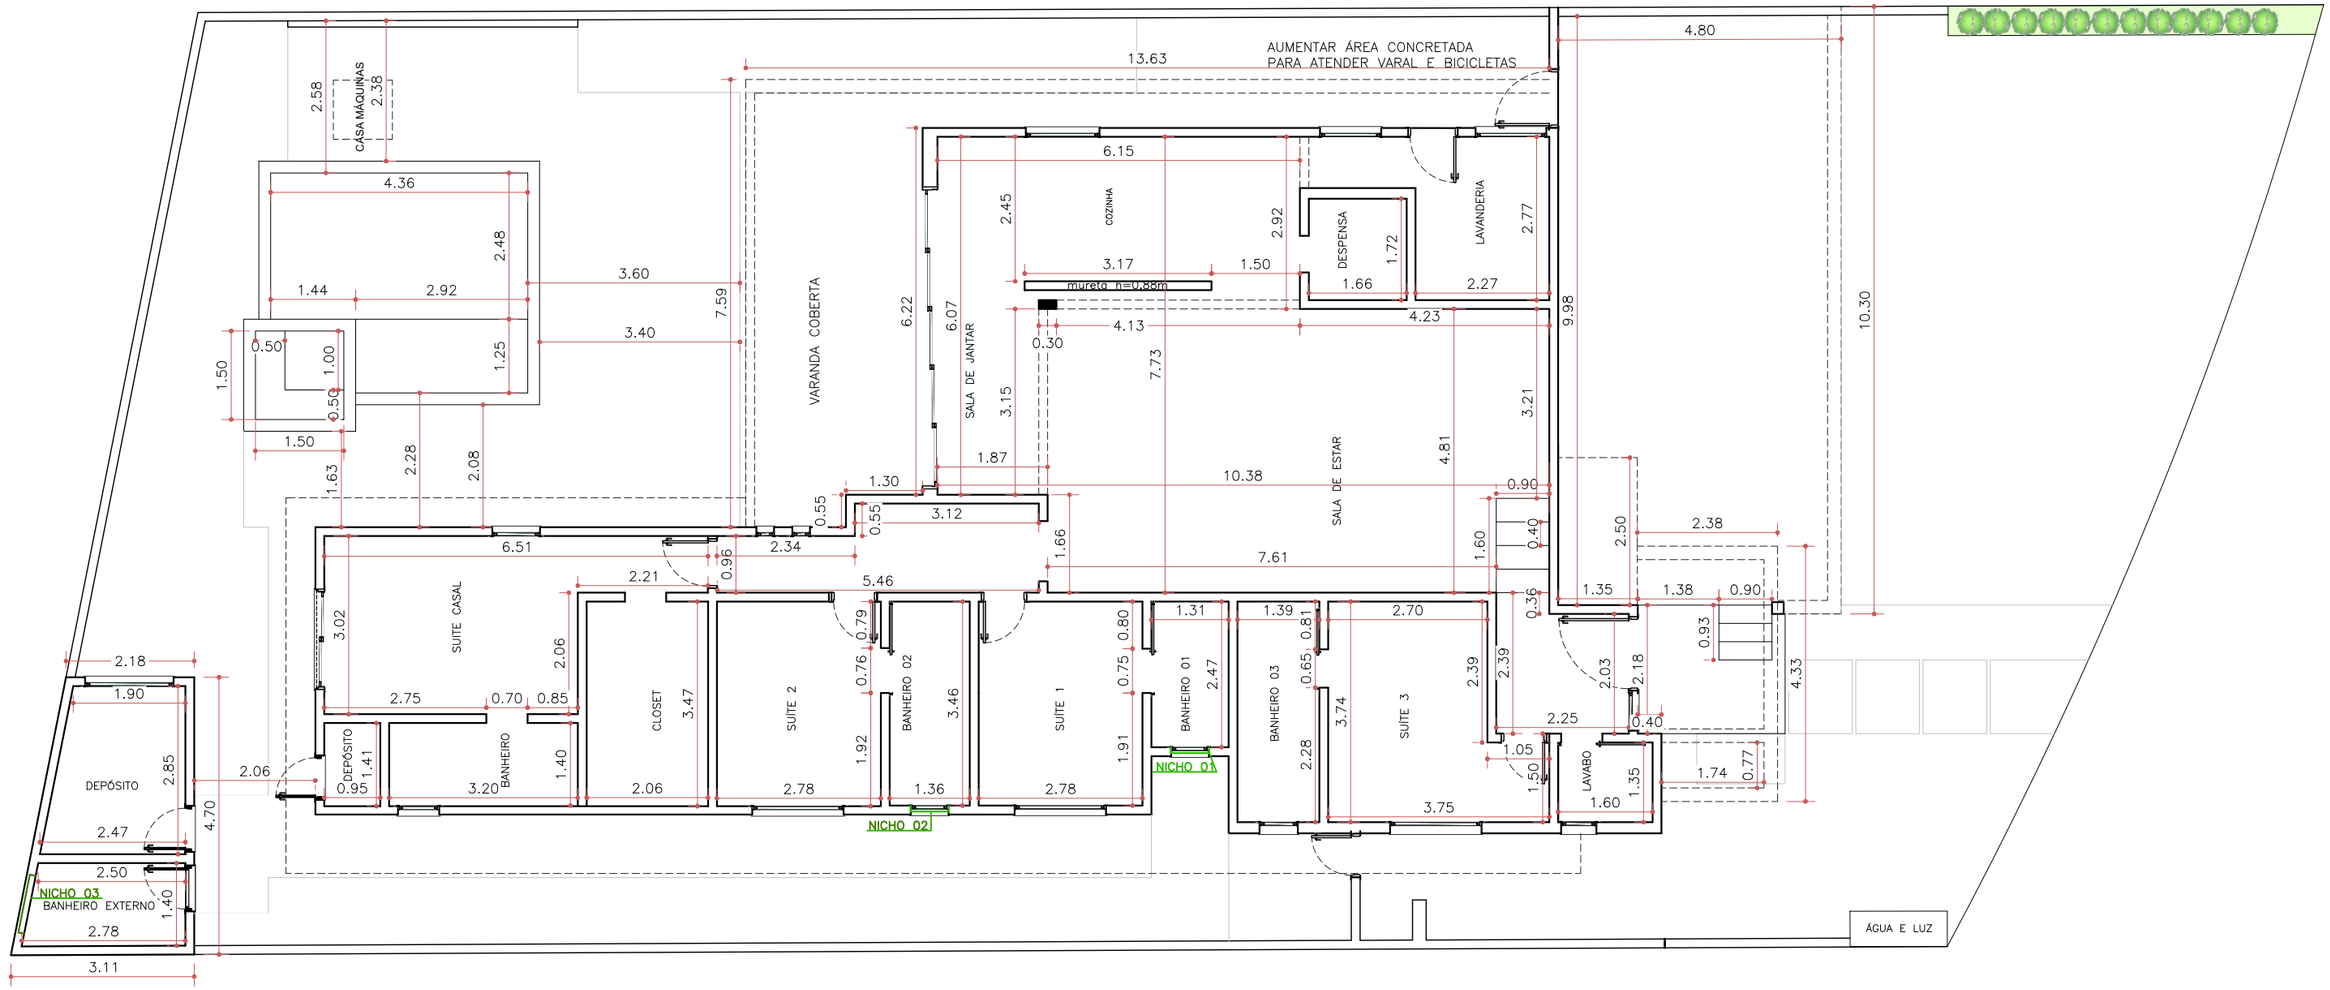

PLANTA BAIXA
ESC. 1:100

OBSERVAÇÕES
- COTAS EM METROS;
- COTAS DE NÍVEL EM METROS;
- CONFERIR MEDIDAS, ABERTURAS, NÍVEIS E PRUMOS NO LOCAL;
- MEDIDAS EM COTA PREVALECEM SOBRE O DESENHO;
- ESSA PRANCHA DEVE SER IMPRESSA COLORIDA;
- É RESPONSABILIDADE DO FORNECEDOR MEDIR E AJUSTAR O PROJETO;
- INSTALAR PENDENTES APÓS A INSTALAÇÃO DE MÓVEIS E MARCENARIA;

DATA: 08/09/2026 | DESENHO: REV00

RESPONSÁVEL: FERNANDA SUELLEM SIMÕES LIMA

LOCAL: R. **QUADRA B, LOTE 11 – CONDOMÍNIO HEVETIA PARK**

ESCALA: **INDICADA** | COD. DO PROJETO: **0000**

CIDADE: INDAIATUBA– SP

FASE: EXECUTIVO

FOLHA: 04/39


FORMATO: A3

PROJETO: RESIDENCIAL


CLIENTE: **KATIA**

ASSUNTO: PLANTA BAIXA


SIMÕES Arquitetura & Design de Interiores
EMAIL: ARQUITETURA@SIMOESARQUITETURA.COM.BR
INSTAGRAM: @SIMOESARQUITETURA

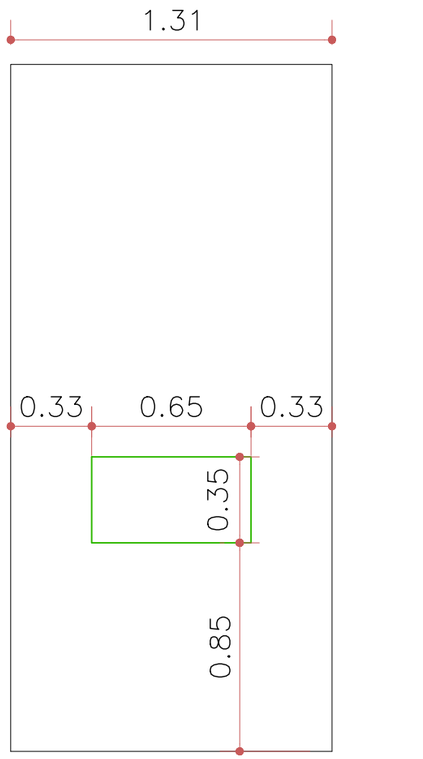

NICHO 01 –PROF. 0.10 M – BH. 01
ESC. 1:25

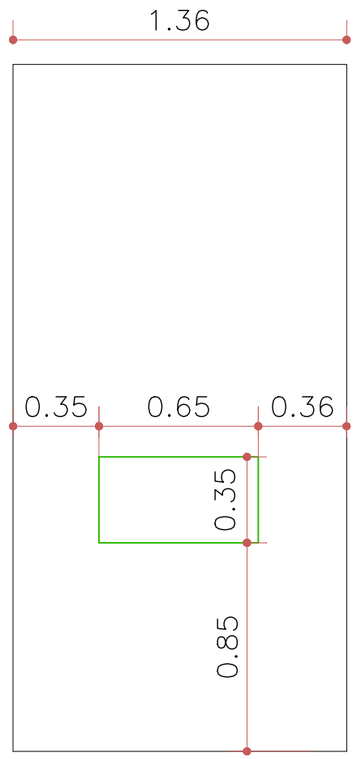

NICHO 02 –PROF. 0.10 M – BH. 02
ESC. 1:25

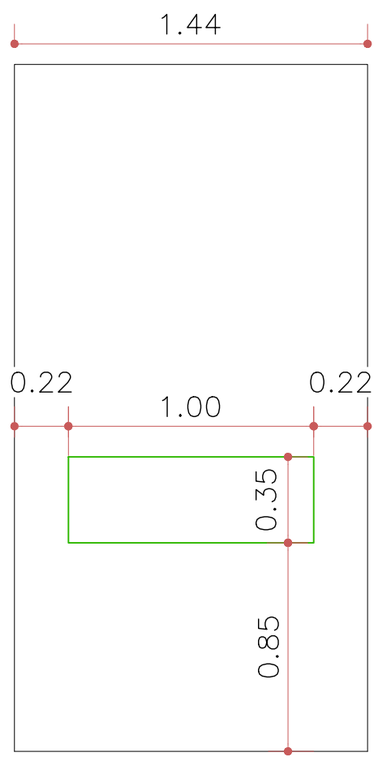

NICHO 03 –PROF. 0.10 M – BH. EXTERNO
ESC. 1:25

OBSERVAÇÕES
- COTAS EM METROS;
- COTAS DE NÍVEL EM METROS;
- CONFERIR MEDIDAS, ABERTURAS, NÍVEIS E PRUMOS NO LOCAL;
- MEDIDAS EM COTA PREVALECEM SOBRE O DESENHO;
- ESSA PRANCHA DEVE SER IMPRESSA COLORIDA;
- É RESPONSABILIDADE DO FORNECEDOR MEDIR E AJUSTAR O PROJETO;
- INSTALAR PENDENTES APÓS A INSTALAÇÃO DE MÓVEIS E MARCENARIA;

DATA 08/09/2026 | DESENHO REV00

RESPONSÁVEL
FERNANDA SUELLEM SIMÕES LIMA

LOCAL
R. **QUADRA B, LOTE 11 – CONDOMÍNIO HEVETIA PARK**

ESCALA **INDICADA** | COD. DO PROJETO **0000**

CIDADE
INDAIATUBA– SP

FASE
EXECUTIVO

FOLHA 05/39


FORMATO
A3

PROJETO
RESIDENCIAL

CLIENTE
KATIA

ASSUNTO
NICHOS

SIMÕES Arquitetura & Design de Interiores
EMAIL: ARQUITETURA@SIMOESARQUITETURA.COM.BR
INSTAGRAM: @SIMOESARQUITETURA

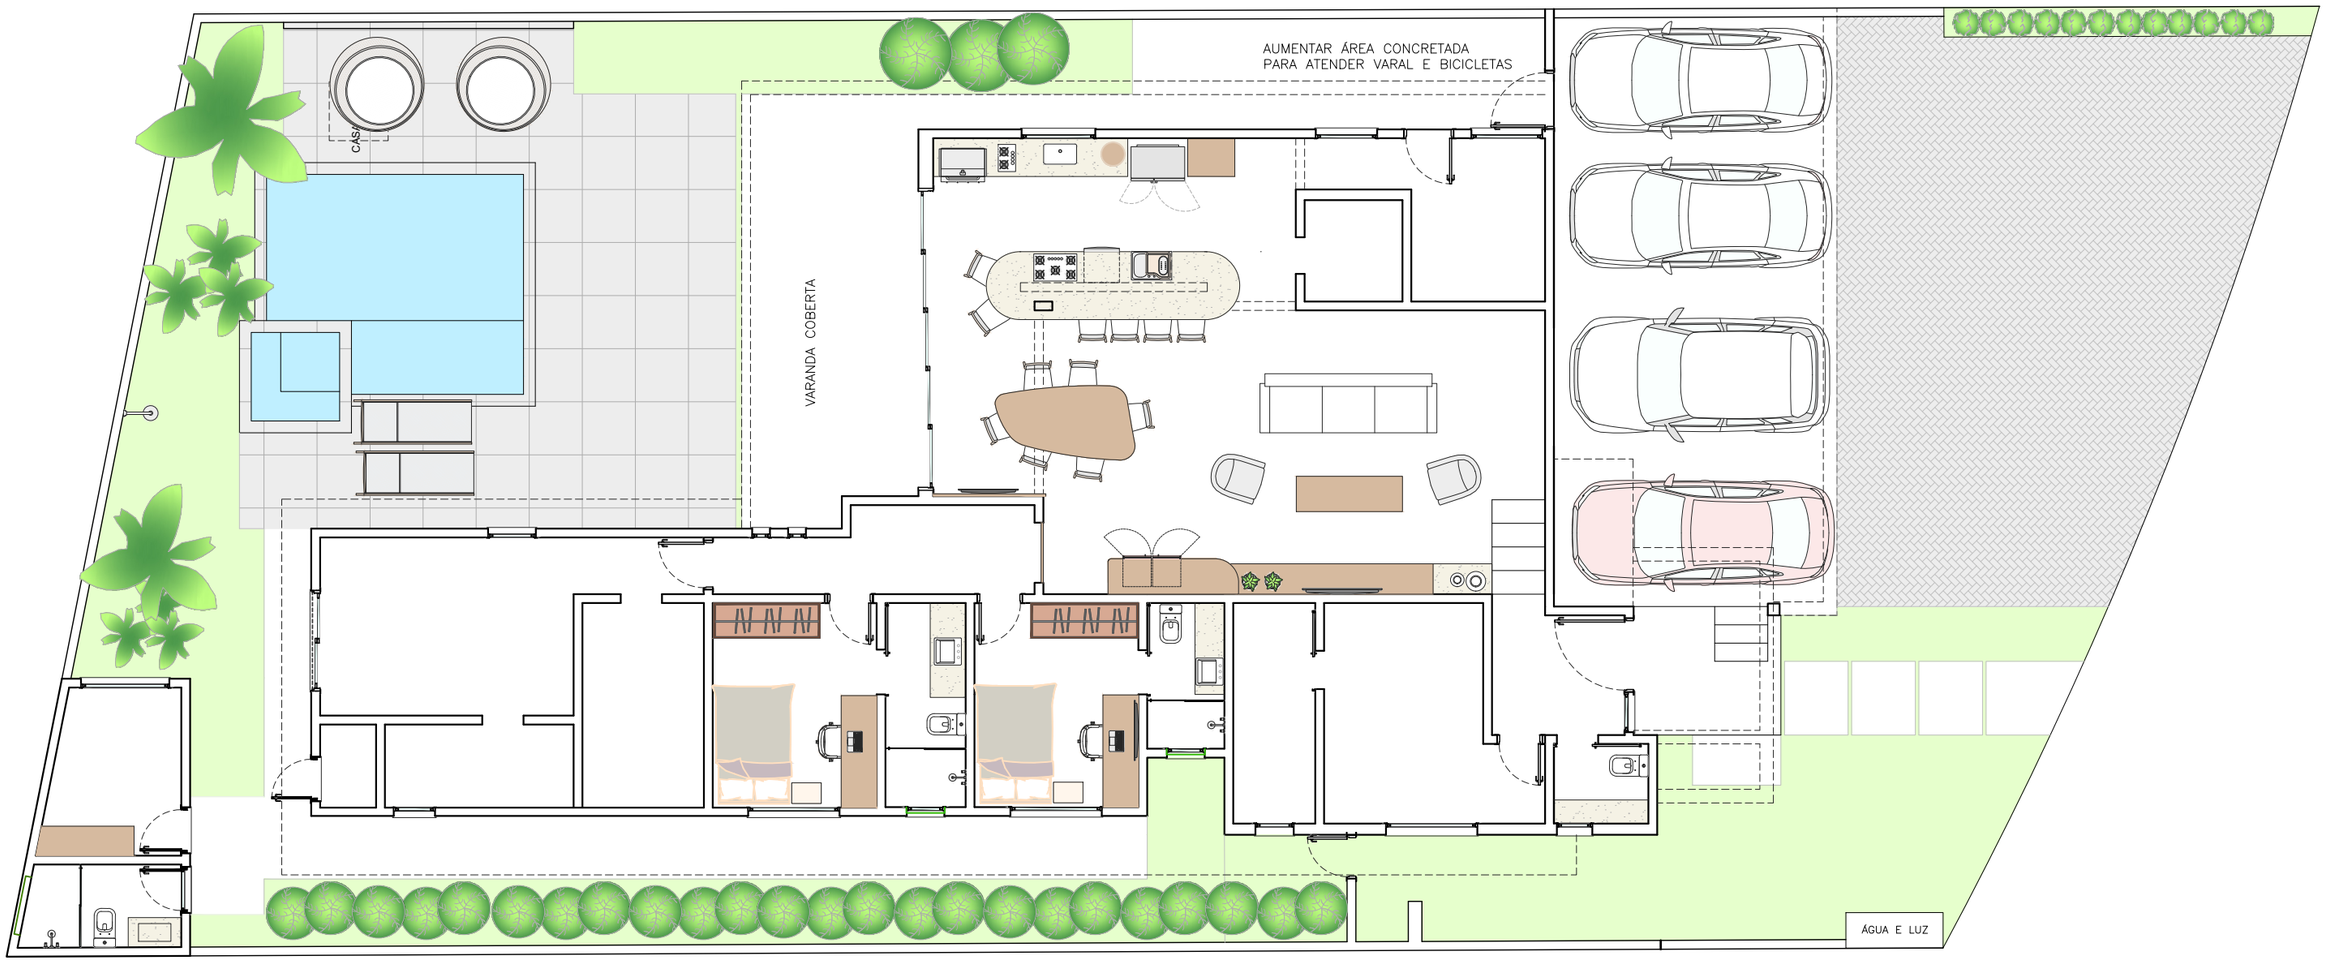

LAYOUT
ESC. 1:100

OBSERVAÇÕES
- COTAS EM METROS;
- COTAS DE NÍVEL EM METROS;
- CONFERIR MEDIDAS, ABERTURAS, NÍVEIS E PRUMOS NO LOCAL;
- MEDIDAS EM COTA PREVALECEM SOBRE O DESENHO;
- ESSA PRANCHA DEVE SER IMPRESSA COLORIDA;
- É RESPONSABILIDADE DO FORNECEDOR MEDIR E AJUSTAR O PROJETO;
- INSTALAR PENDENTES APÓS A INSTALAÇÃO DE MÓVEIS E MARCENARIA;

DATA: 08/09/2026 | DESENHO: REV00

RESPONSÁVEL: FERNANDA SUELLEM SIMÕES LIMA

LOCAL: R. **QUADRA B, LOTE 11 – CONDOMÍNIO HEVETIA PARK**

ESCALA: **INDICADA** | COD. DO PROJETO: **0000**

CIDADE: INDAIATUBA– SP

FASE: EXECUTIVO

FOLHA: 06 / 39


FORMATO: A3

PROJETO: RESIDENCIAL

CLIENTE: **KATIA**

ASSUNTO: LAYOUT

SIMÕES Arquitetura & Design de Interiores
EMAIL: ARQUITETURA@SIMOESARQUITETURA.COM.BR
INSTAGRAM: @SIMOESARQUITETURA

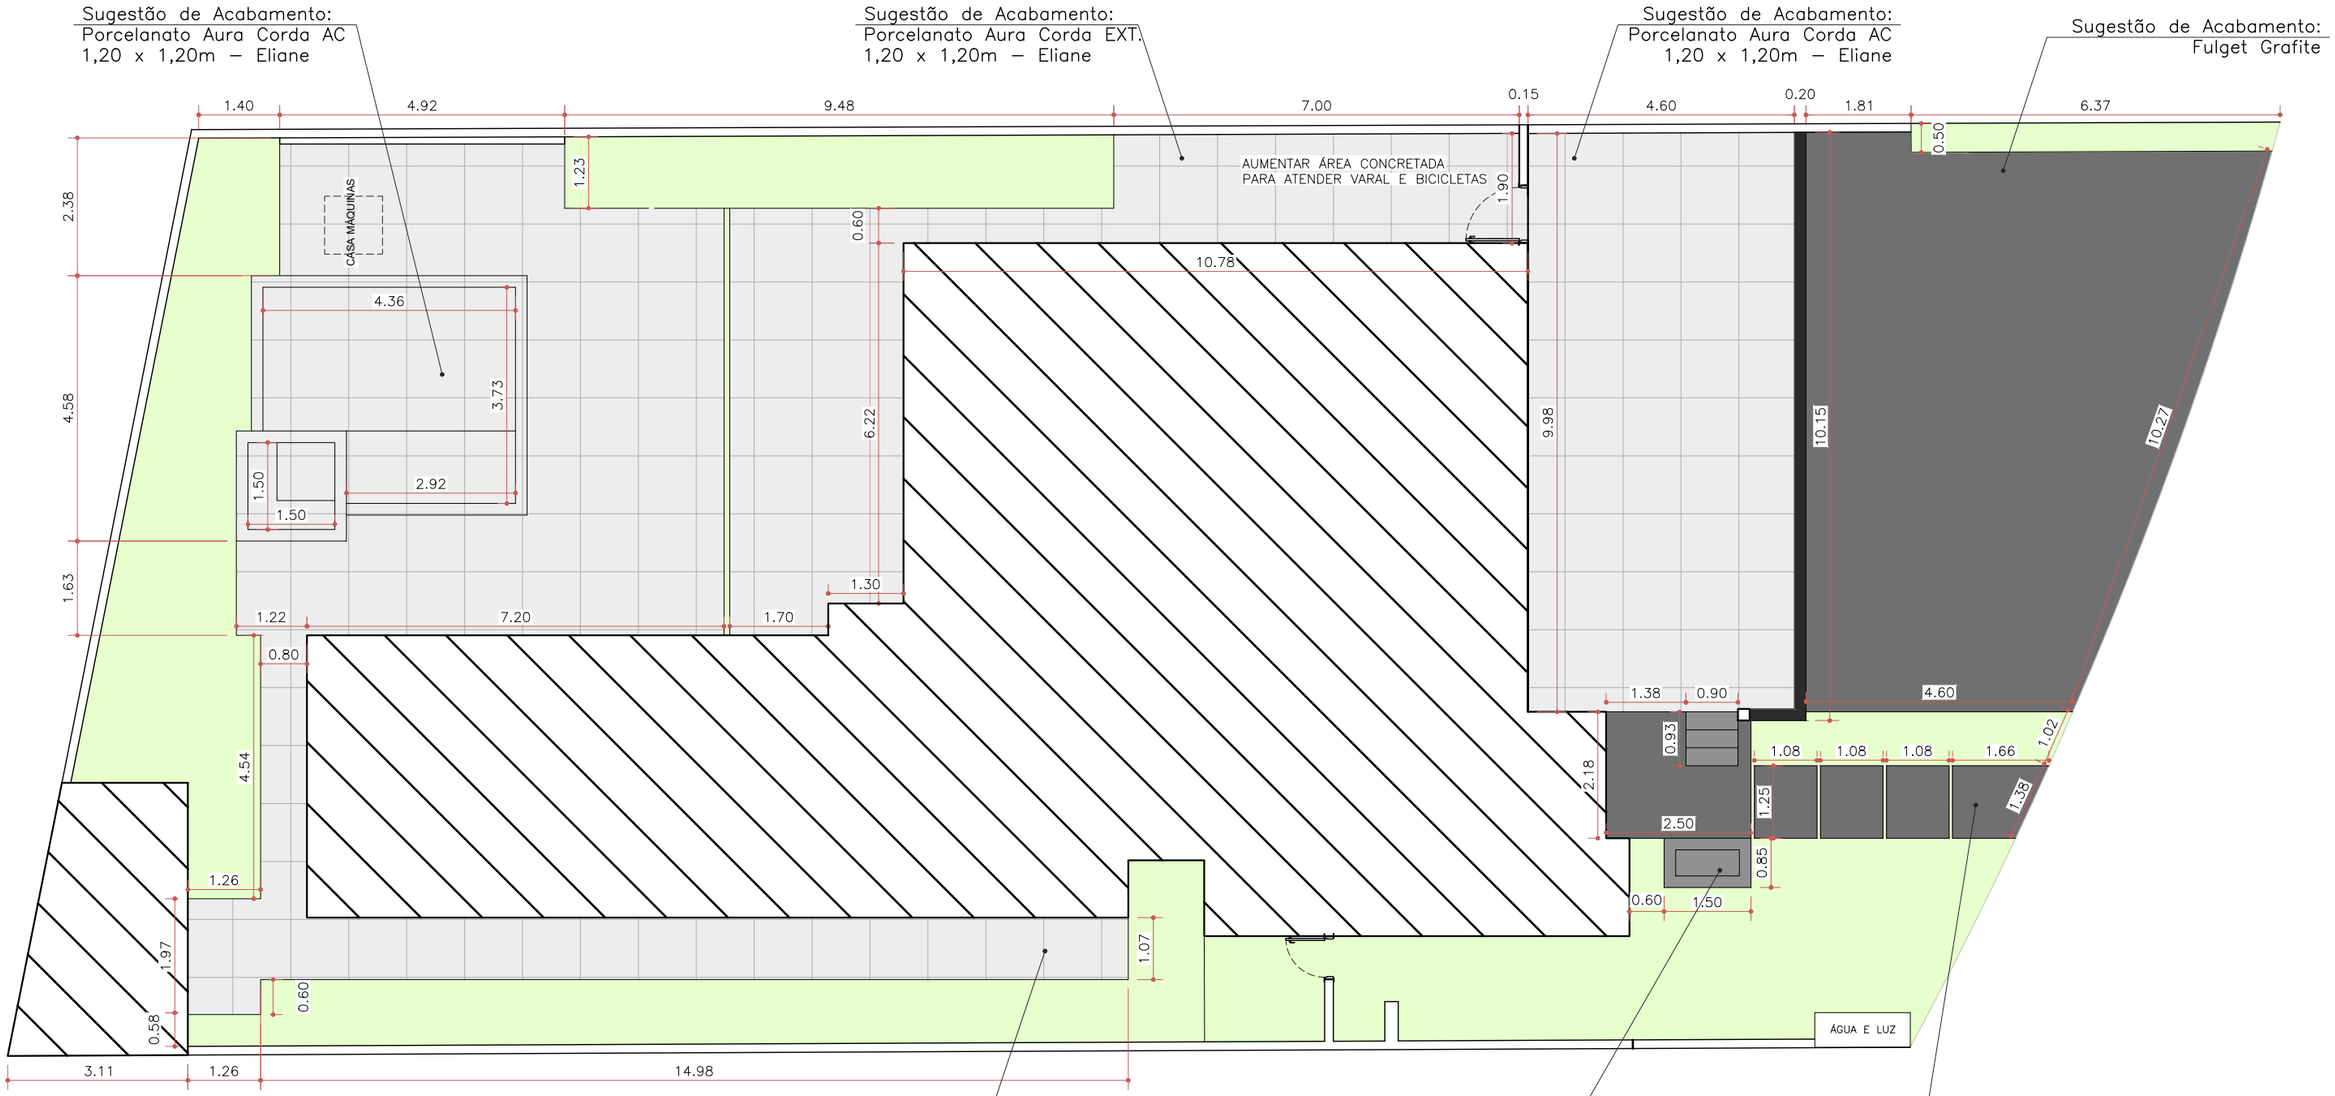

DETALHAMENTO PISOS EXTERNOS

ESC. 1:100

Sugestão de Acabamento:
Porcelanato Aura Corda EXT.
1,20 x 1,20m – Eliane

Sugestão de Acabamento:
Fulget Cinza

Sugestão de Acabamento:
Fulget Grafite

OBSERVAÇÕES

- COTAS EM METROS;
- COTAS DE NÍVEL EM METROS;
- CONFERIR MEDIDAS, ABERTURAS, NÍVEIS E PRUMOS NO LOCAL;
- MEDIDAS EM COTA PREVALECEM SOBRE O DESENHO;
- ESSA PRANCHA DEVE SER IMPRESSA COLORIDA;
- É RESPONSABILIDADE DO FORNECEDOR MEDIR E AJUSTAR O PROJETO;
- INSTALAR PENDENTES APÓS A INSTALAÇÃO DE MÓVEIS E MARCENARIA;

DATA: 08/09/2026 | DESENHO: REV00

RESPONSÁVEL: FERNANDA SUELLEM SIMÕES LIMA

LOCAL: R. **QUADRA B, LOTE 11 – CONDOMÍNIO HEVETIA PARK**

ESCALA: **INDICADA** | COD. DO PROJETO: **0000**

CIDADE: INDAIATUBA– SP

FASE: EXECUTIVO

FOLHA: 07/39

FORMATO: A3


PROJETO: RESIDENCIAL


CLIENTE: **KATIA**

ASSUNTO: DETALHAMENTO PISOS EXTERNOS


SIMÕES Arquitetura & Design de Interiores
EMAIL: ARQUITETURA@SIMOESARQUITETURA.COM.BR
INSTAGRAM: @SIMOESARQUITETURA

Sugestão de Acabamento:
Porcelanato Aura Corda AC
1,20 x 1,20m – Eliane

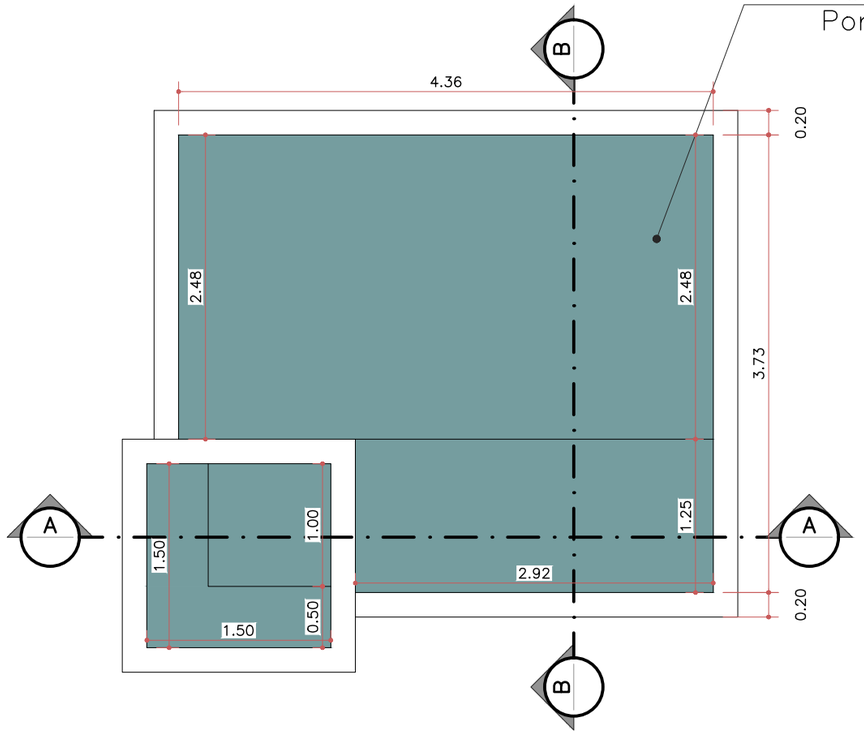

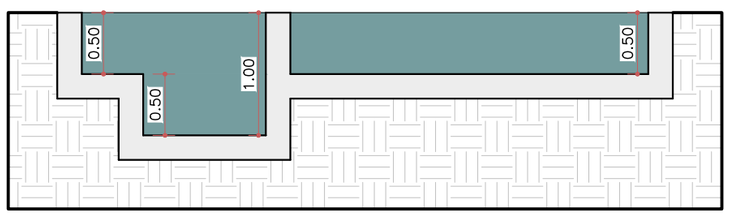

CORTE AA
1:50

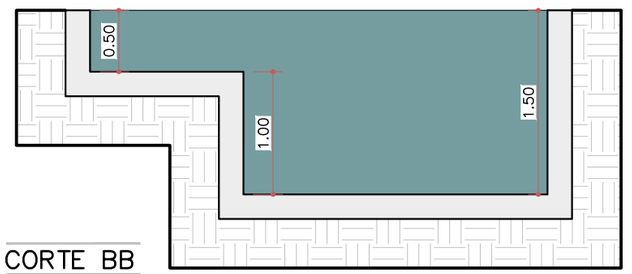

CORTE BB
1:50

OBSERVAÇÕES
- COTAS EM METROS;
- COTAS DE NÍVEL EM METROS;
- CONFERIR MEDIDAS, ABERTURAS, NÍVEIS E PRUMOS NO LOCAL;
- MEDIDAS EM COTA PREVALECEM SOBRE O DESENHO;
- ESSA PRANCHA DEVE SER IMPRESSA COLORIDA;
- É RESPONSABILIDADE DO FORNECEDOR MEDIR E AJUSTAR O PROJETO;
- INSTALAR PENDENTES APÓS A INSTALAÇÃO DE MÓVEIS E MARCENARIA;

DATA 08/09/2026 | DESENHO REV00

RESPONSÁVEL
FERNANDA SUELLEM SIMÕES LIMA

LOCAL
R. **QUADRA B, LOTE 11 – CONDOMÍNIO HEVETIA PARK**

ESCALA | COD. DO PROJETO **0000**

CIDADE
INDAIATUBA– SP

FASE
EXECUTIVO

FOLHA 08/39


FORMATO
A3

PROJETO
RESIDENCIAL

CLIENTE
KATIA

ASSUNTO
DETALHE PISCINA

SIMÕES Arquitetura & Design de Interiores
EMAIL: ARQUITETURA@SIMOESARQUITETURA.COM.BR
INSTAGRAM: @SIMOESARQUITETURA

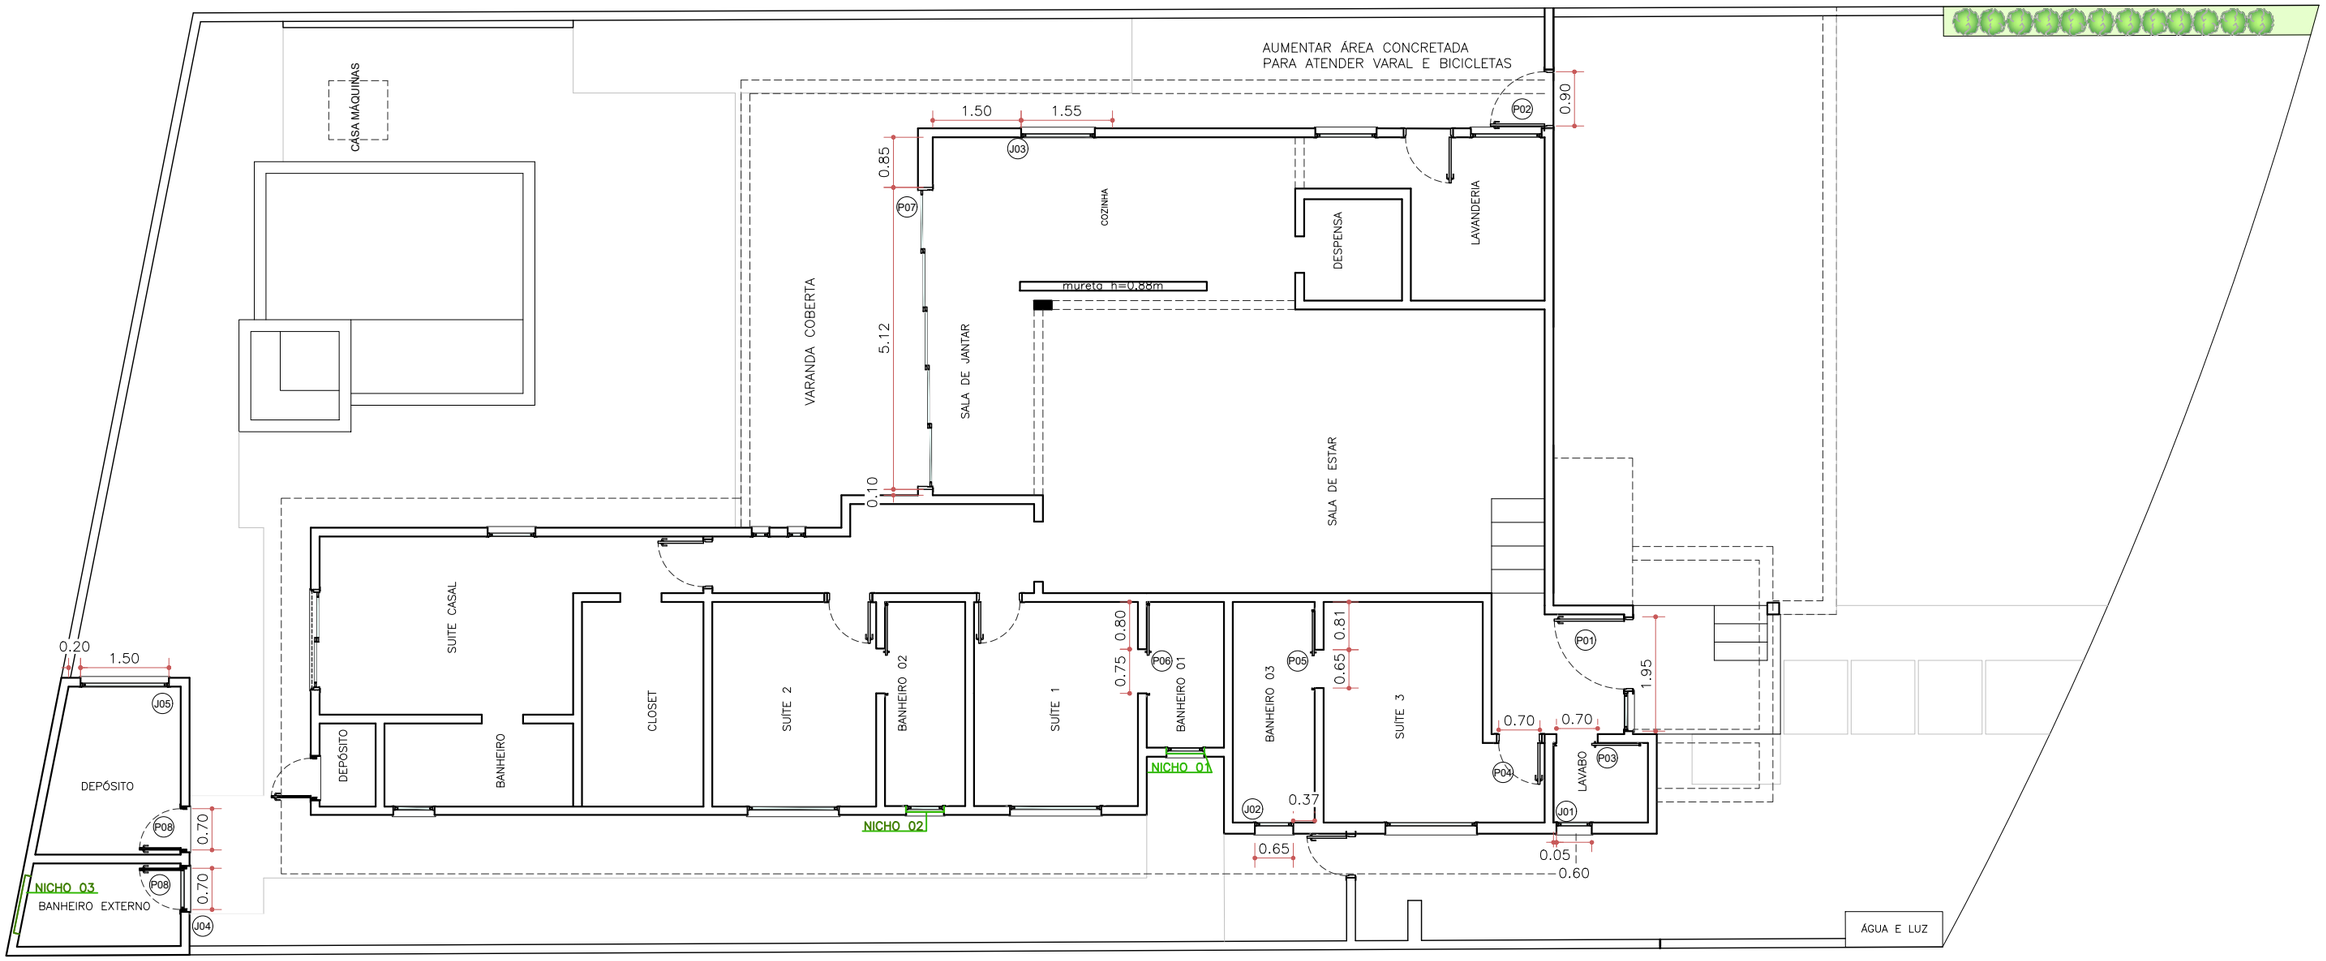

LOCALIZAÇÃO DAS ESQUADRIAS
ESC. 1:100

OBSERVAÇÕES
- COTAS EM METROS;
- COTAS DE NÍVEL EM METROS;
- CONFERIR MEDIDAS, ABERTURAS, NÍVEIS E PRUMOS NO LOCAL;
- MEDIDAS EM COTA PREVALECEM SOBRE O DESENHO;
- ESSA PRANCHA DEVE SER IMPRESSA COLORIDA;
- É RESPONSABILIDADE DO FORNECEDOR MEDIR E AJUSTAR O PROJETO;
- INSTALAR PENDENTES APÓS A INSTALAÇÃO DE MÓVEIS E MARCENARIA;

DATA 08/09/2026 | DESENHO REV00

RESPONSÁVEL
FERNANDA SUELLEM SIMÕES LIMA

LOCAL
R. **QUADRA B, LOTE 11 – CONDOMÍNIO HEVETIA PARK**

ESCALA **INDICADA** | COD. DO PROJETO **0000**

CIDADE
INDAIATUBA– SP

FASE
EXECUTIVO

FOLHA 09/39

FORMATO
A3


PROJETO
RESIDENCIAL

CLIENTE
KATIA

ASSUNTO
LOCALIZAÇÃO DAS ESQUADRIAS

SIMÕES Arquitetura & Design de Interiores
EMAIL: ARQUITETURA@SIMOESARQUITETURA.COM.BR
INSTAGRAM: @SIMOESARQUITETURA


P1
Ambiente: Hall de Entrada.
Porta Pivotante, 1 Folha, Alumínio ou ACM Preto + Vidro Fixo
Dimensões: 1,95 x 2,40m
Qtde.: 1 UNIDADE

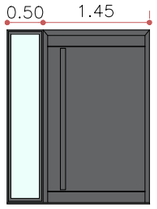


P2
Ambiente: Garagem.
Porta de giro, alumínio ou ACM Preto, 1 folha.
Dimensões: 0,90 x 2,10m
Qtde.: 1 UNIDADE




P3
Ambiente: Lavabo.
Porta de correr, madeira, 1 folha.
Dimensões: 0,70 x 2,10 m
Qtde.: 1 UNIDADE

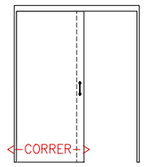


P4
Ambiente: Suíte 03.
Porta de giro, madeira, 1 folha.
Dimensões: 0,70 x 2,10m
Qtde.: 1 UNIDADE

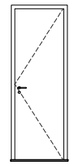


P5
Ambiente: Banho 03.
Porta de correr, madeira, 1 folha.
Dimensões: 0,65 x 2,10 m
Qtde.: 1 UNIDADE

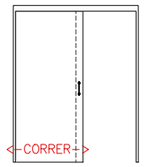


P6
Ambiente: Banho 01.
Porta de correr, madeira, 1 folha.
Dimensões: 0,75 x 2,10 m
Qtde.: 1 UNIDADE

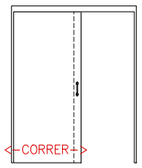

P7
Ambiente: Cozinhar.
Porta de correr, 5 folhas, alumínio branco e vidro incolor.
Dimensões: 5,12 x 2,40m
Qtde.: 1 UNIDADE

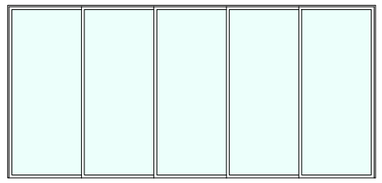

P8
Ambiente: Depósito e Banho Ext.
Porta de alumínio branco, giro, 1 folha, veneziana ventilada.
Dimensões: 0,70 x 2,10 m
Qtde.: 2 UNIDADES

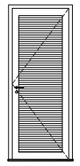


J1
Ambiente: Lavabo.
Janela maxim ar, 1 folha, alumínio branco e vidro miniboreal.
Dimensões: 0,60 x 0,60/1,60m
Qtde.: 1 UNIDADE



J2
Ambiente: Lavabo.
Janela maxim ar, 1 folha, alumínio branco e vidro miniboreal.
Dimensões: 0,65 x 0,60/1,60m
Qtde.: 1 UNIDADE




J3
Ambiente: Cozinha.
Janela de correr, 2 folhas, alumínio branco e vidro incolor.
Dimensões: 1,25 x 0,50/1,00m
Qtde.: 1 UNIDADE

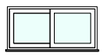

J4
Ambiente: Banho Ext..
Janela maxim ar, 1 folha, alumínio branco e vidro miniboreal.
Dimensões: 0,70 x 0,30/2,10m
Qtde.: 1 UNIDADE



J5
Ambiente: Cozinha.
Janela de correr, 2 folhas, alumínio branco e vidro incolor.
Dimensões: 1,50 x 1,55/0,60m
Qtde.: 1 UNIDADE

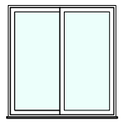

OBSERVAÇÕES
- COTAS EM METROS;
- COTAS DE NÍVEL EM METROS;
- CONFERIR MEDIDAS, ABERTURAS, NÍVEIS E PRUMOS NO LOCAL;
- MEDIDAS EM COTA PREVALECEM SOBRE O DESENHO;
- ESSA PRANCHA DEVE SER IMPRESSA COLORIDA;
- É RESPONSABILIDADE DO FORNECEDOR MEDIR E AJUSTAR O PROJETO;
- INSTALAR PENDENTES APÓS A INSTALAÇÃO DE MÓVEIS E MARCENARIA;

DATA 08/09/2026 | DESENHO REV00

RESPONSÁVEL
FERNANDA SUELLEM SIMÕES LIMA

LOCAL
R. **QUADRA B, LOTE 11 – CONDOMÍNIO HEVETIA PARK**

ESCALA | COD. DO PROJETO **0000**

CIDADE
INDAIATUBA– SP

FASE
EXECUTIVO

FOLHA 10/39

FORMATO
A3


PROJETO
RESIDENCIAL

CLIENTE
KATIA

ASSUNTO
ESQUADRIAS

SIMÕES Arquitetura & Design de Interiores
EMAIL: ARQUITETURA@SIMOESARQUITETURA.COM.BR
INSTAGRAM: @SIMOESARQUITETURA

*PEDRA SUGERIDA:
BRANCO ESPÍRITO SANTO

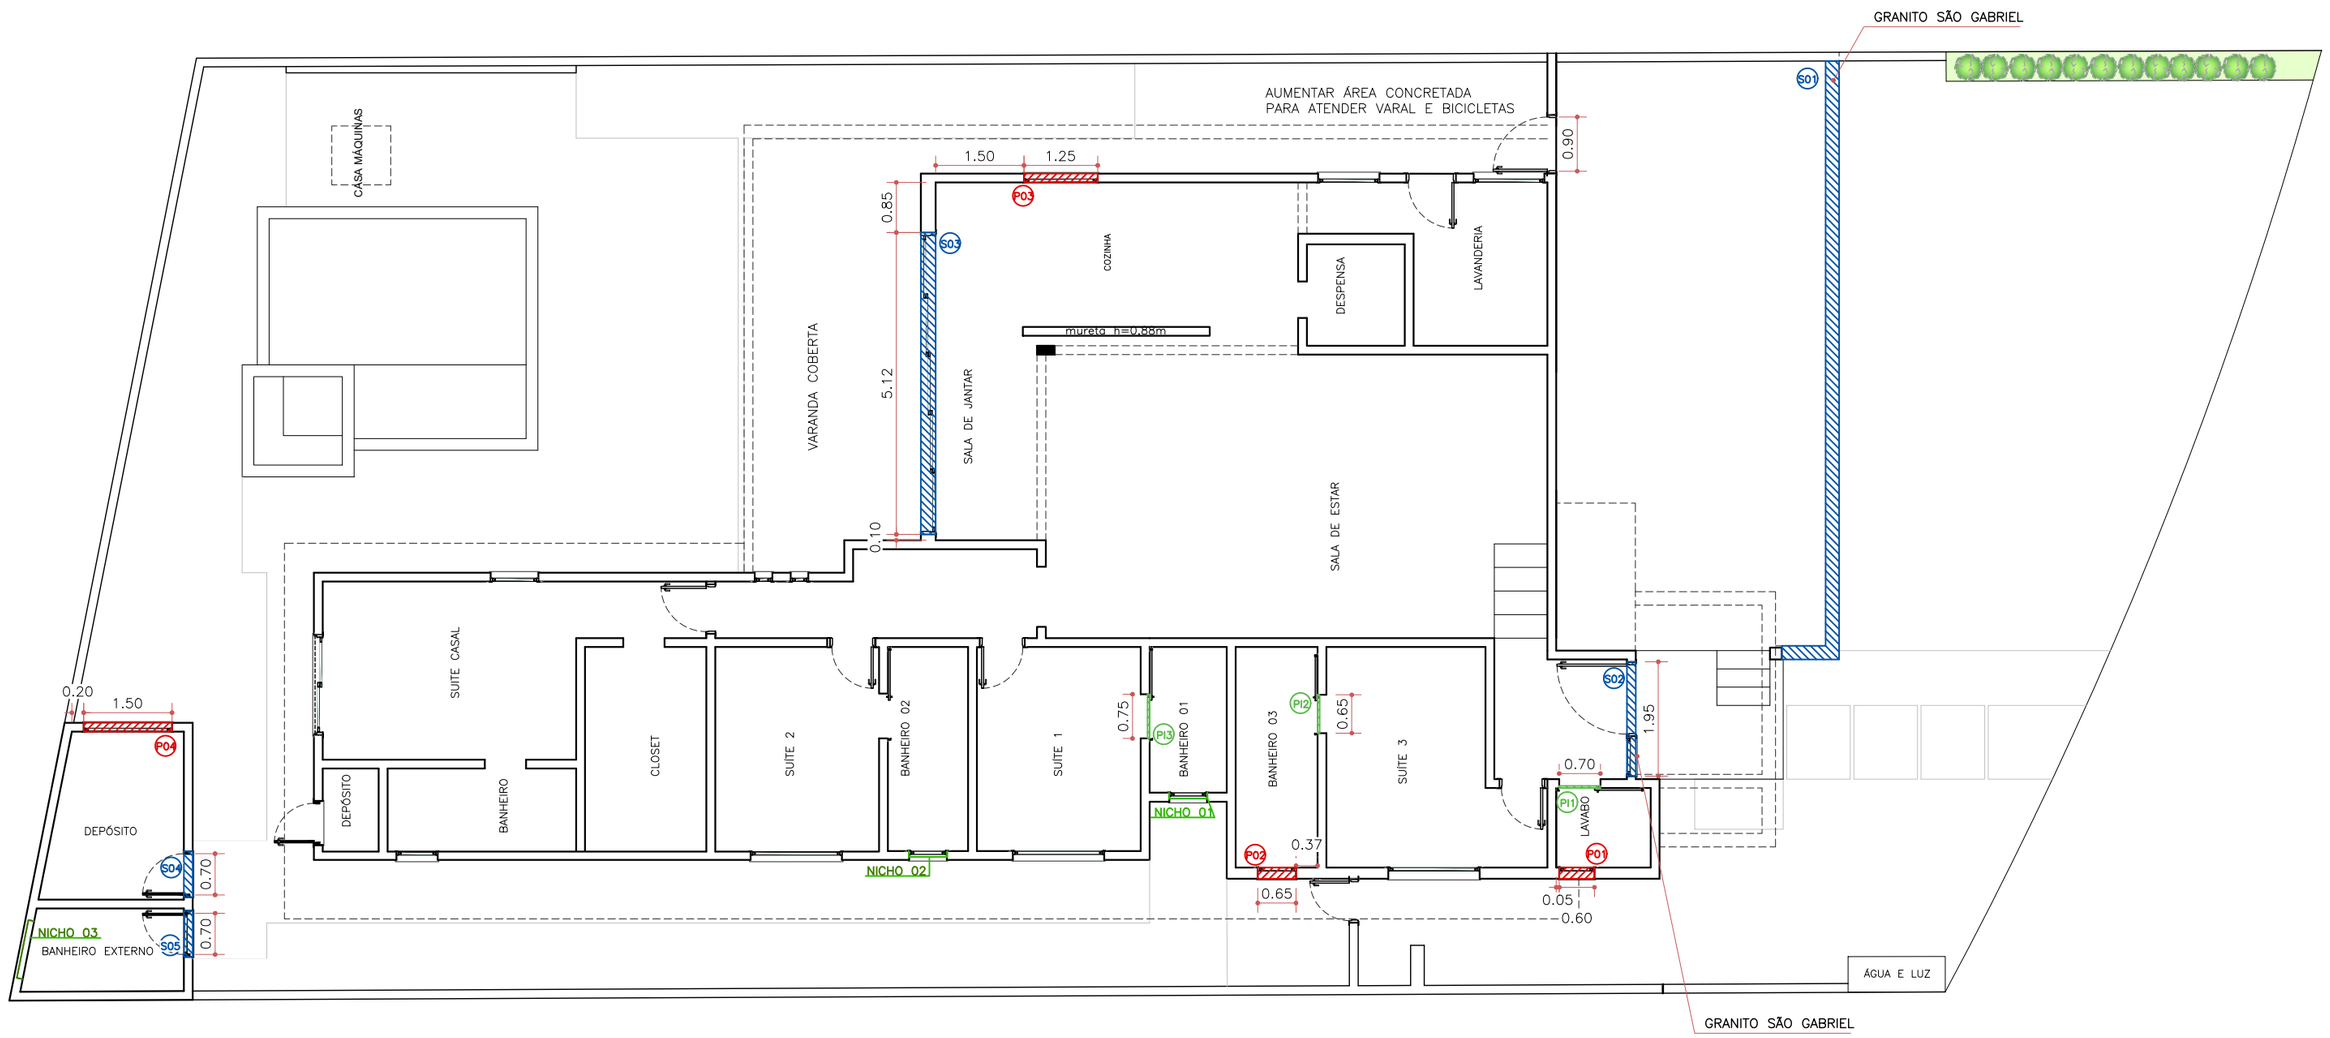

SOLEIRAS E PINGADEIRAS
ESC. 1:100


OBSERVAÇÕES
- COTAS EM METROS;
- COTAS DE NÍVEL EM METROS;
- CONFERIR MEDIDAS, ABERTURAS, NÍVEIS E PRUMOS NO LOCAL;
- MEDIDAS EM COTA PREVALECEM SOBRE O DESENHO;
- ESSA PRANCHA DEVE SER IMPRESSA COLORIDA;
- É RESPONSABILIDADE DO FORNECEDOR MEDIR E AJUSTAR O PROJETO;
- INSTALAR PENDENTES APÓS A INSTALAÇÃO DE MÓVEIS E MARCENARIA;

DATA: 08/09/2026 | DESENHO: REV00
RESPONSÁVEL: FERNANDA SUELLEM SIMÕES LIMA
LOCAL: R. **QUADRA B, LOTE 11 – CONDOMÍNIO HEVETIA PARK**
ESCALA: **INDICADA** | COD. DO PROJETO: **0000**

CIDADE: INDAIATUBA– SP
FASE: EXECUTIVO
FOLHA: 11 / 39
FORMATO: A3

PROJETO: RESIDENCIAL
CLIENTE: **KATIA**
ASSUNTO: SOLEIRAS E PINGADEIRAS

SIMÕES Arquitetura & Design de Interiores
EMAIL: ARQUITETURA@SIMOESARQUITETURA.COM.BR
INSTAGRAM: @SIMOESARQUITETURA

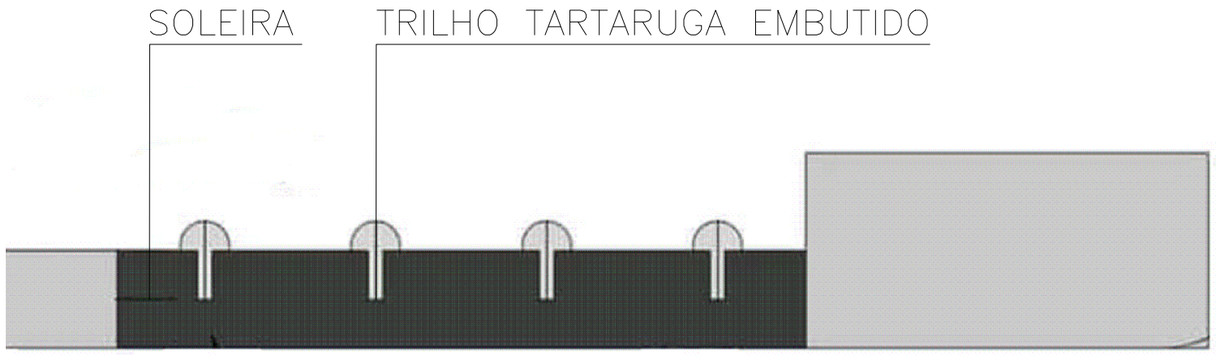

LEGENDA	
SÍMBOLO	DESCRIÇÃO
	PINGADEIRA (P)
	SOLEIRA (S)
	PERFIL INOX

PINGADEIRAS

CÓDIGO	AMBIENTE	DIMENSÃO (EM METRO) (LARGURA X PROF.)
P01	LAVABO	0,60 X 0,17
P02	BANHO 03	0,65 X 0,17
P03	COZINHA	1,25 X 0,17
P04	DEPÓSITO	1,50 X 0,17

PERFIL INOX

CÓDIGO	AMBIENTE	DIMENSÃO (EM METRO) (LARGURA X PROF.)
PI1	LAVABO	0,70 X 0,03
PI2	BANHO 03	0,65 X 0,03
PI3	BANHO 01	0,75 X 0,03

SOLEIRAS

CÓDIGO	AMBIENTE	DIMENSÃO (EM METRO) (LARGURA X PROF.)
S1	GARAGEM	VIDE PLANTA
S2	SALA	1,95 X 0,20
S3	COZINHA	5,12 X 0,25
S4	DEPÓSITO	0,70 X 0,15
S5	BANHO EXTERNO	0,70 X 0,15

OBSERVAÇÕES

- COTAS EM METROS;
- COTAS DE NÍVEL EM METROS;
- CONFERIR MEDIDAS, ABERTURAS, NÍVEIS E PRUMOS NO LOCAL;
- MEDIDAS EM COTA PREVALECEM SOBRE O DESENHO;
- ESSA PRANCHA DEVE SER IMPRESSA COLORIDA;
- É RESPONSABILIDADE DO FORNECEDOR MEDIR E AJUSTAR O PROJETO;
- INSTALAR PENDENTES APÓS A INSTALAÇÃO DE MÓVEIS E MARCENARIA;

DATA 08/09/2026 | DESENHO REV00

RESPONSÁVEL FERNANDA SUELLEM SIMÕES LIMA

LOCAL R. **QUADRA B, LOTE 11 – CONDOMÍNIO HEVETIA PARK**

ESCALA **INDICADA** | COD. DO PROJETO **0000**

CIDADE INDAIATUBA– SP

FASE EXECUTIVO

FOLHA 12/39

FORMATO A3


PROJETO RESIDENCIAL

CLIENTE **KATIA**


ASSUNTO SOLEIRAS E PINGADEIRAS

SIMÕES Arquitetura & Design de Interiores
EMAIL: ARQUITETURA@SIMOESARQUITETURA.COM.BR
INSTAGRAM: @SIMOESARQUITETURA

*REALIZAR TESTE DE COR NO LOCAL

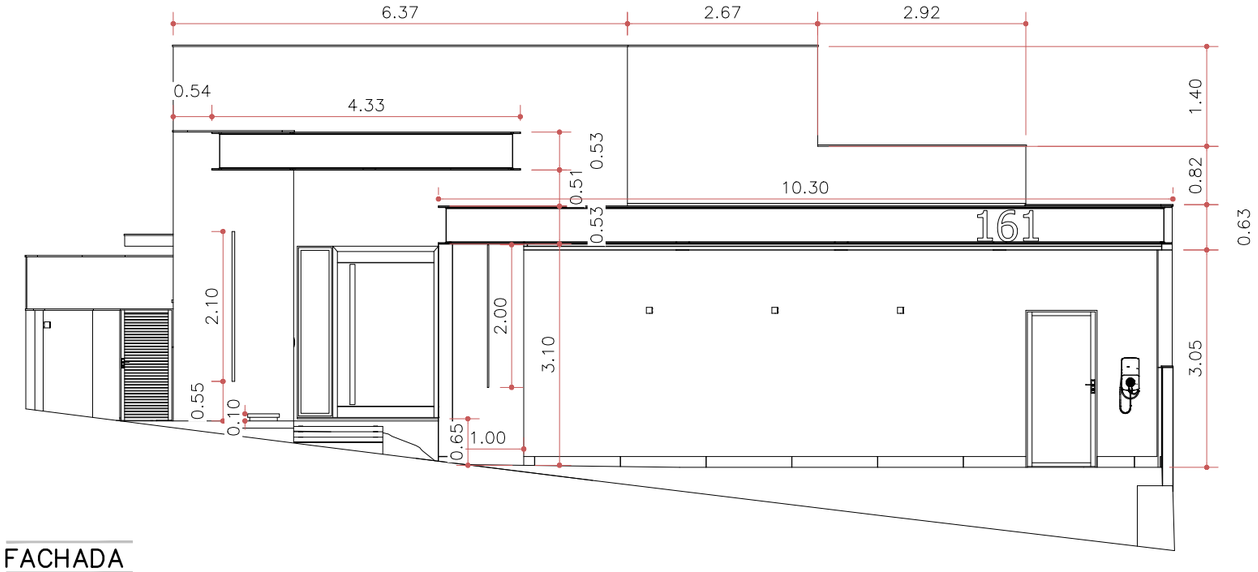

FACHADA
ESC. 1:100

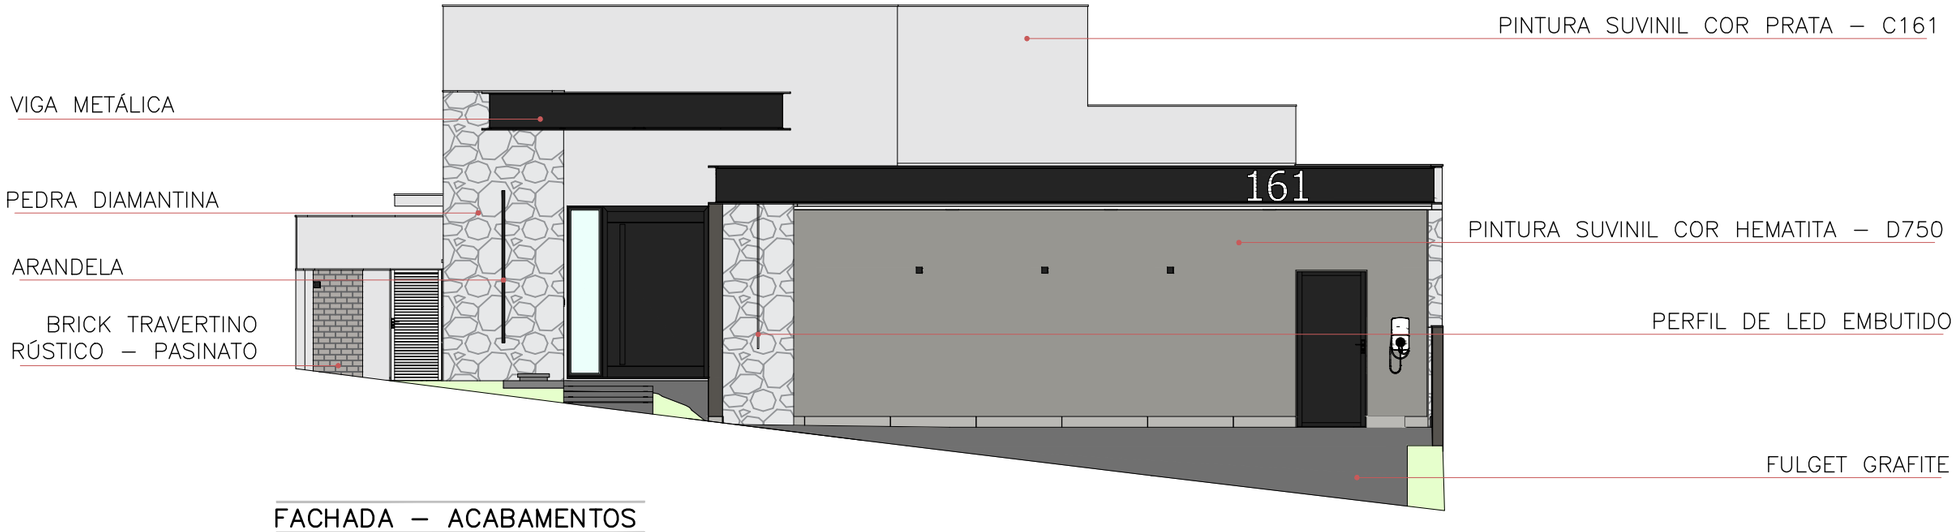

FACHADA – ACABAMENTOS
ESC. 1:100

OBSERVAÇÕES
- COTAS EM METROS;
- COTAS DE NÍVEL EM METROS;
- CONFERIR MEDIDAS, ABERTURAS, NÍVEIS E PRUMOS NO LOCAL;
- MEDIDAS EM COTA PREVALECEM SOBRE O DESENHO;
- ESSA PRANCHA DEVE SER IMPRESSA COLORIDA;
- É RESPONSABILIDADE DO FORNECEDOR MEDIR E AJUSTAR O PROJETO;
- INSTALAR PENDENTES APÓS A INSTALAÇÃO DE MÓVEIS E MARCENARIA;

DATA 08/09/2026 | DESENHO REV00

RESPONSÁVEL
FERNANDA SUELLEM SIMÕES LIMA

LOCAL
R. **QUADRA B, LOTE 11 – CONDOMÍNIO HEVETIA PARK**

ESCALA **INDICADA** | COD. DO PROJETO **0000**

CIDADE
INDAIATUBA– SP

FASE
EXECUTIVO

FOLHA 13/39

FORMATO
A3

PROJETO
RESIDENCIAL

CLIENTE
KATIA

ASSUNTO
FACHADA

SIMÕES Arquitetura & Design de Interiores
EMAIL: ARQUITETURA@SIMOESARQUITETURA.COM.BR
INSTAGRAM: @SIMOESARQUITETURA



PERSPECTIVA FACHADA
ESC. 1:100

OBSERVAÇÕES
- COTAS EM METROS;
- COTAS DE NÍVEL EM METROS;
- CONFERIR MEDIDAS, ABERTURAS, NÍVEIS E PRUMOS NO LOCAL;
- MEDIDAS EM COTA PREVALECEM SOBRE O DESENHO;
- ESSA PRANCHA DEVE SER IMPRESSA COLORIDA;
- É RESPONSABILIDADE DO FORNECEDOR MEDIR E AJUSTAR O PROJETO;
- INSTALAR PENDENTES APÓS A INSTALAÇÃO DE MÓVEIS E MARCENARIA;

DATA: 08/09/2026 | DESENHO: REV00

RESPONSÁVEL: FERNANDA SUELLEM SIMÕES LIMA

LOCAL: R. **QUADRA B, LOTE 11 – CONDOMÍNIO HEVETIA PARK**

ESCALA: **INDICADA** | COD. DO PROJETO: **0000**

CIDADE: INDAIATUBA– SP

FASE: EXECUTIVO

FOLHA: 14 / 39


FORMATO: A3

PROJETO: RESIDENCIAL

CLIENTE: **KATIA**

ASSUNTO: PERPSECTIVA FACHADA

SIMÕES Arquitetura & Design de Interiores
EMAIL: ARQUITETURA@SIMOESARQUITETURA.COM.BR
INSTAGRAM: @SIMOESARQUITETURA

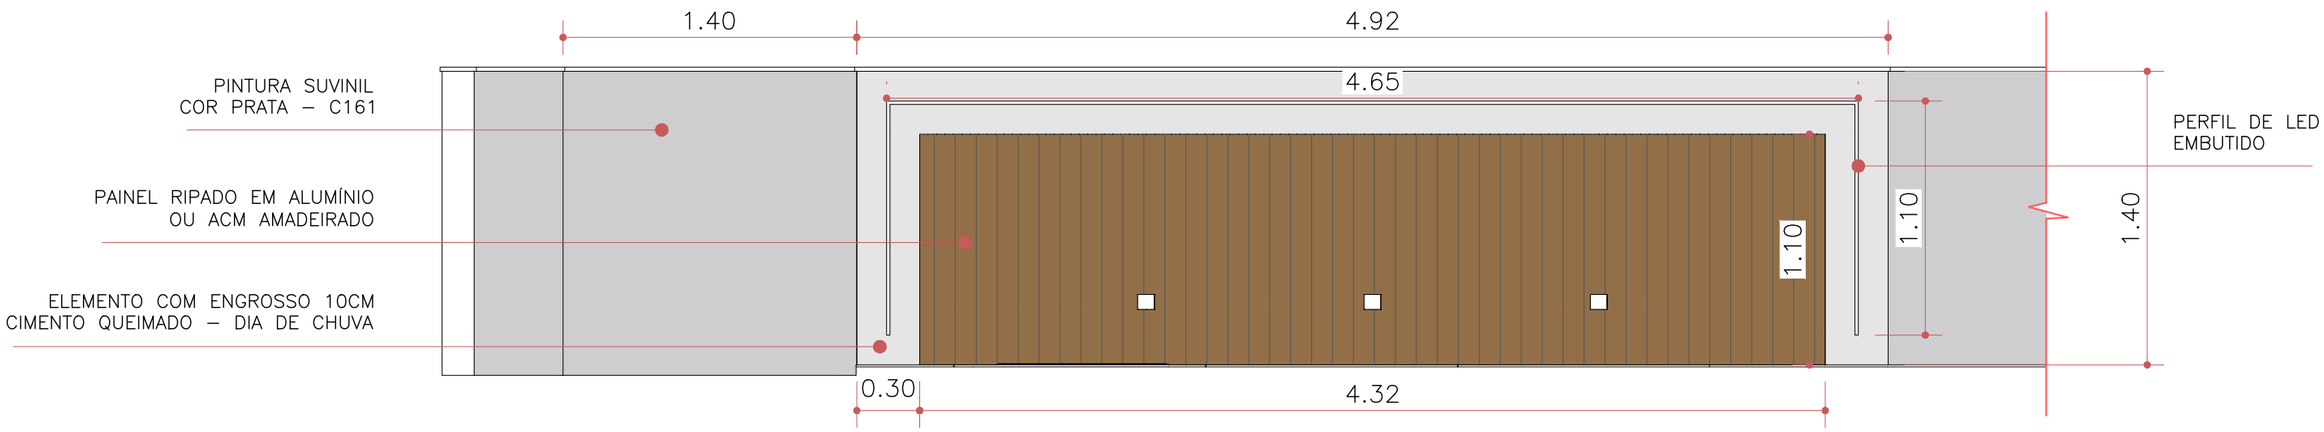

VISTA MURO FUNDO INTERNO
ESC. 1:25

OBSERVAÇÕES
- COTAS EM METROS;
- COTAS DE NÍVEL EM METROS;
- CONFERIR MEDIDAS, ABERTURAS, NÍVEIS E PRUMOS NO LOCAL;
- MEDIDAS EM COTA PREVALECEM SOBRE O DESENHO;
- ESSA PRANCHA DEVE SER IMPRESSA COLORIDA;
- É RESPONSABILIDADE DO FORNECEDOR MEDIR E AJUSTAR O PROJETO;
- INSTALAR PENDENTES APÓS A INSTALAÇÃO DE MÓVEIS E MARCENARIA;

DATA 08/09/2026 | DESENHO REV00

RESPONSÁVEL
FERNANDA SUELLEM SIMÕES LIMA

LOCAL
R. **QUADRA B, LOTE 11 – CONDOMÍNIO HEVETIA PARK**

ESCALA **INDICADA** | COD. DO PROJETO **0000**

CIDADE
INDAIATUBA– SP

FASE
EXECUTIVO

FOLHA 15/39


FORMATO
A3

PROJETO
RESIDENCIAL


CLIENTE
KATIA

ASSUNTO
VISTA MURO

SIMÕES Arquitetura & Design de Interiores
EMAIL: ARQUITETURA@SIMOESARQUITETURA.COM.BR
INSTAGRAM: @SIMOESARQUITETURA

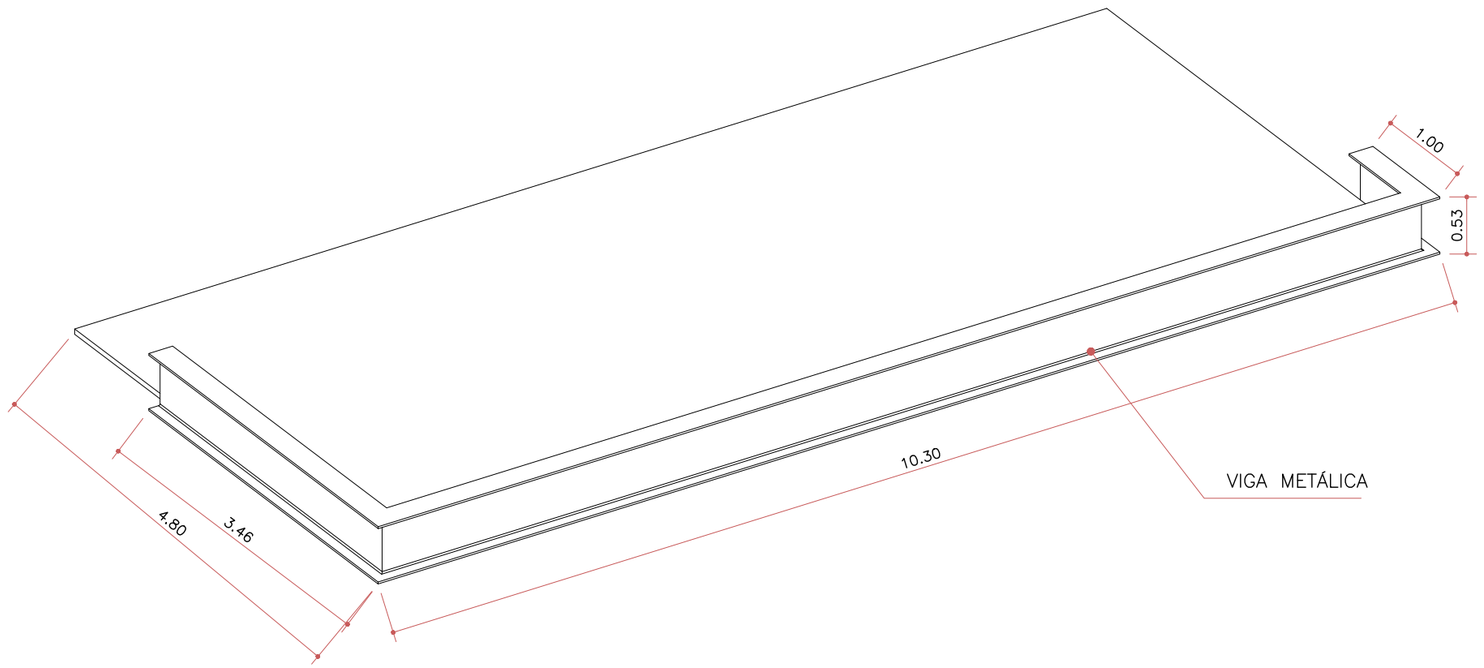

DETALHE – ELEMENTO 01
ESC. 1:50

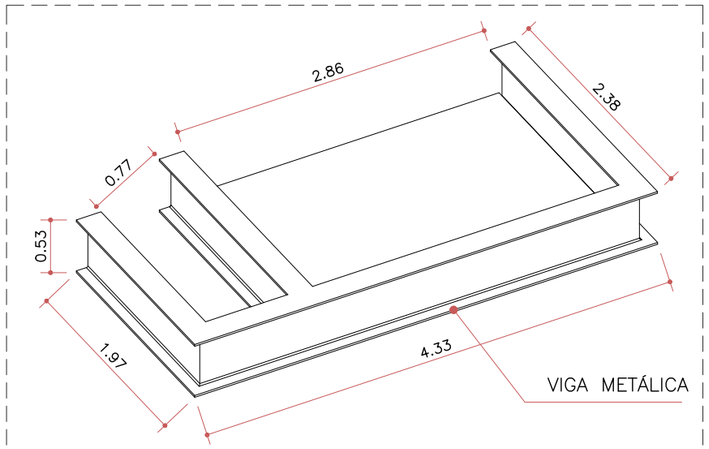

DETALHE – ELEMENTO 01
ESC. 1:50

OBSERVAÇÕES
- COTAS EM METROS;
- COTAS DE NÍVEL EM METROS;
- CONFERIR MEDIDAS, ABERTURAS, NÍVEIS E PRUMOS NO LOCAL;
- MEDIDAS EM COTA PREVALECEM SOBRE O DESENHO;
- ESSA PRANCHA DEVE SER IMPRESSA COLORIDA;
- É RESPONSABILIDADE DO FORNECEDOR MEDIR E AJUSTAR O PROJETO;
- INSTALAR PENDENTES APÓS A INSTALAÇÃO DE MÓVEIS E MARCENARIA;

DATA 08/09/2026 | DESENHO REV00

RESPONSÁVEL
FERNANDA SUELLEM SIMÕES LIMA

LOCAL
R. **QUADRA B, LOTE 11 – CONDOMÍNIO HEVETIA PARK**

ESCALA **INDICADA** | COD. DO PROJETO **0000**

CIDADE
INDAIATUBA– SP

FASE
EXECUTIVO

FOLHA 16/39


FORMATO
A3

PROJETO
RESIDENCIAL

CLIENTE
KATIA

ASSUNTO
ELEMENTOS FACHADA

SIMÕES Arquitetura & Design de Interiores
EMAIL: ARQUITETURA@SIMOESARQUITETURA.COM.BR
INSTAGRAM: @SIMOESARQUITETURA

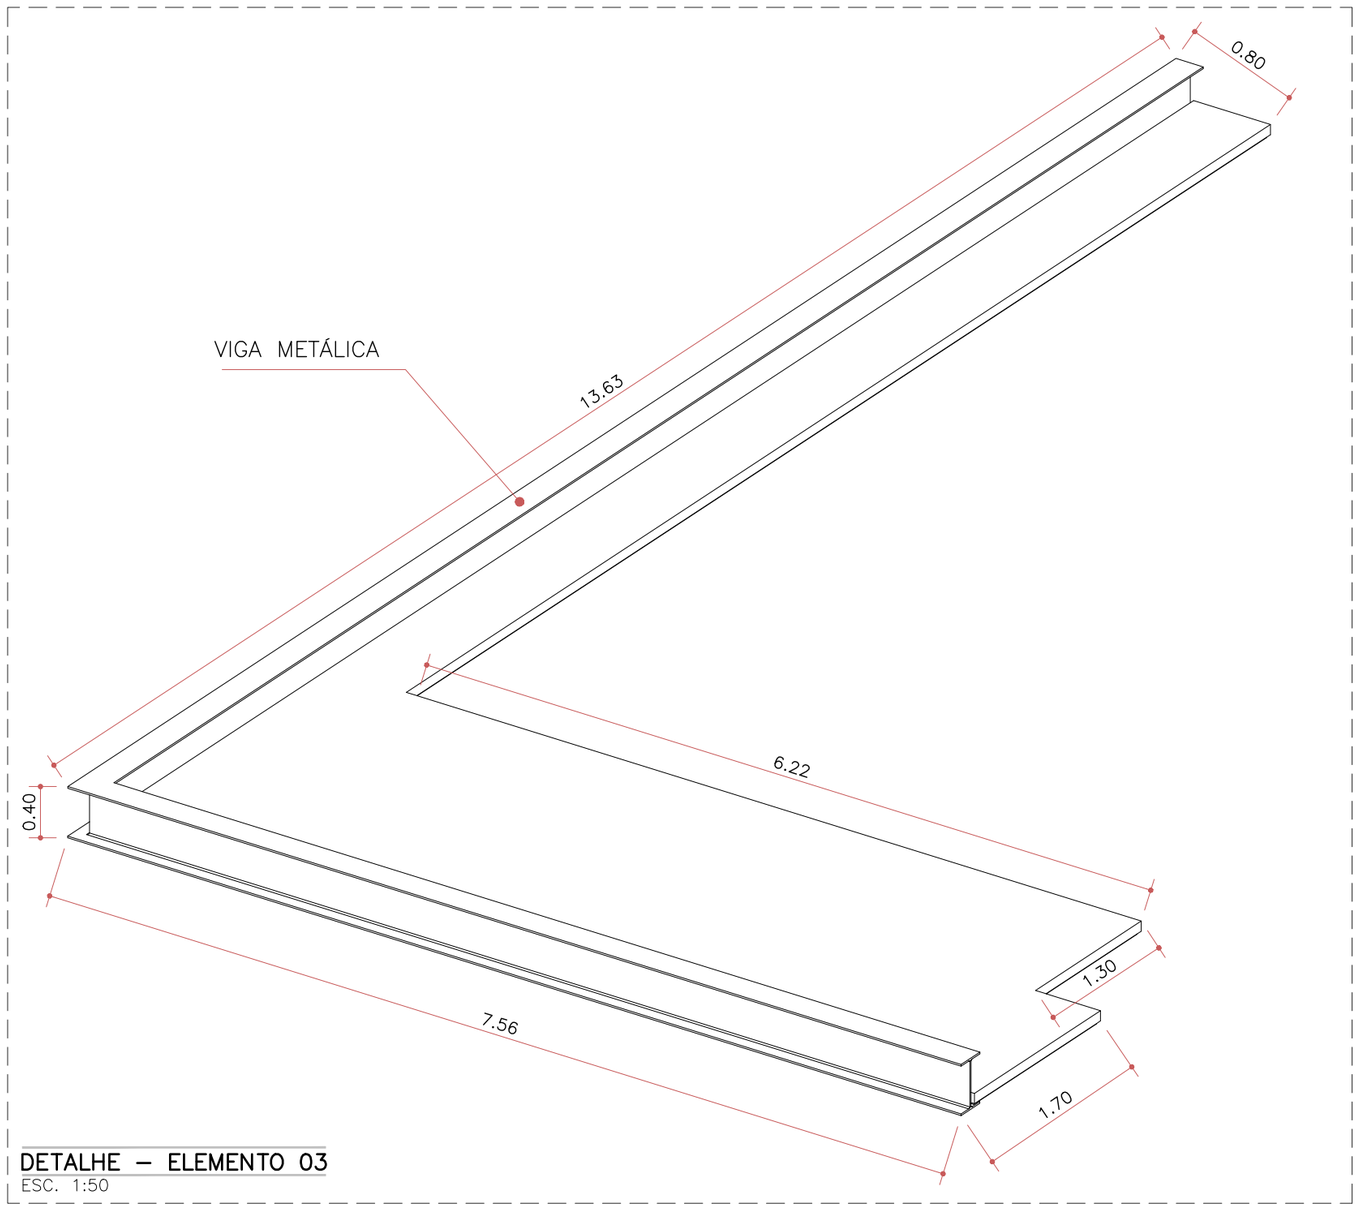

DETALHE – ELEMENTO 03
ESC. 1:50

OBSERVAÇÕES
- COTAS EM METROS;
- COTAS DE NÍVEL EM METROS;
- CONFERIR MEDIDAS, ABERTURAS, NÍVEIS E PRUMOS NO LOCAL;
- MEDIDAS EM COTA PREVALECEM SOBRE O DESENHO;
- ESSA PRANCHA DEVE SER IMPRESSA COLORIDA;
- É RESPONSABILIDADE DO FORNECEDOR MEDIR E AJUSTAR O PROJETO;
- INSTALAR PENDENTES APÓS A INSTALAÇÃO DE MÓVEIS E MARCENARIA;

DATA: 08/09/2026 | DESENHO: REV00

RESPONSÁVEL: FERNANDA SUELLEM SIMÕES LIMA

LOCAL: R. QUADRA B, LOTE 11 – CONDOMÍNIO HEVETIA PARK

ESCALA: INDICADA | COD. DO PROJETO: 0000

CIDADE: INDAIATUBA– SP

FASE: EXECUTIVO

FOLHA: 17 / 39


FORMATO: A3

PROJETO: RESIDENCIAL

CLIENTE: KATIA

ASSUNTO: ELEMENTO FUNDO

SIMÕES Arquitetura & Design de Interiores
EMAIL: ARQUITETURA@SIMOESARQUITETURA.COM.BR
INSTAGRAM: @SIMOESARQUITETURA

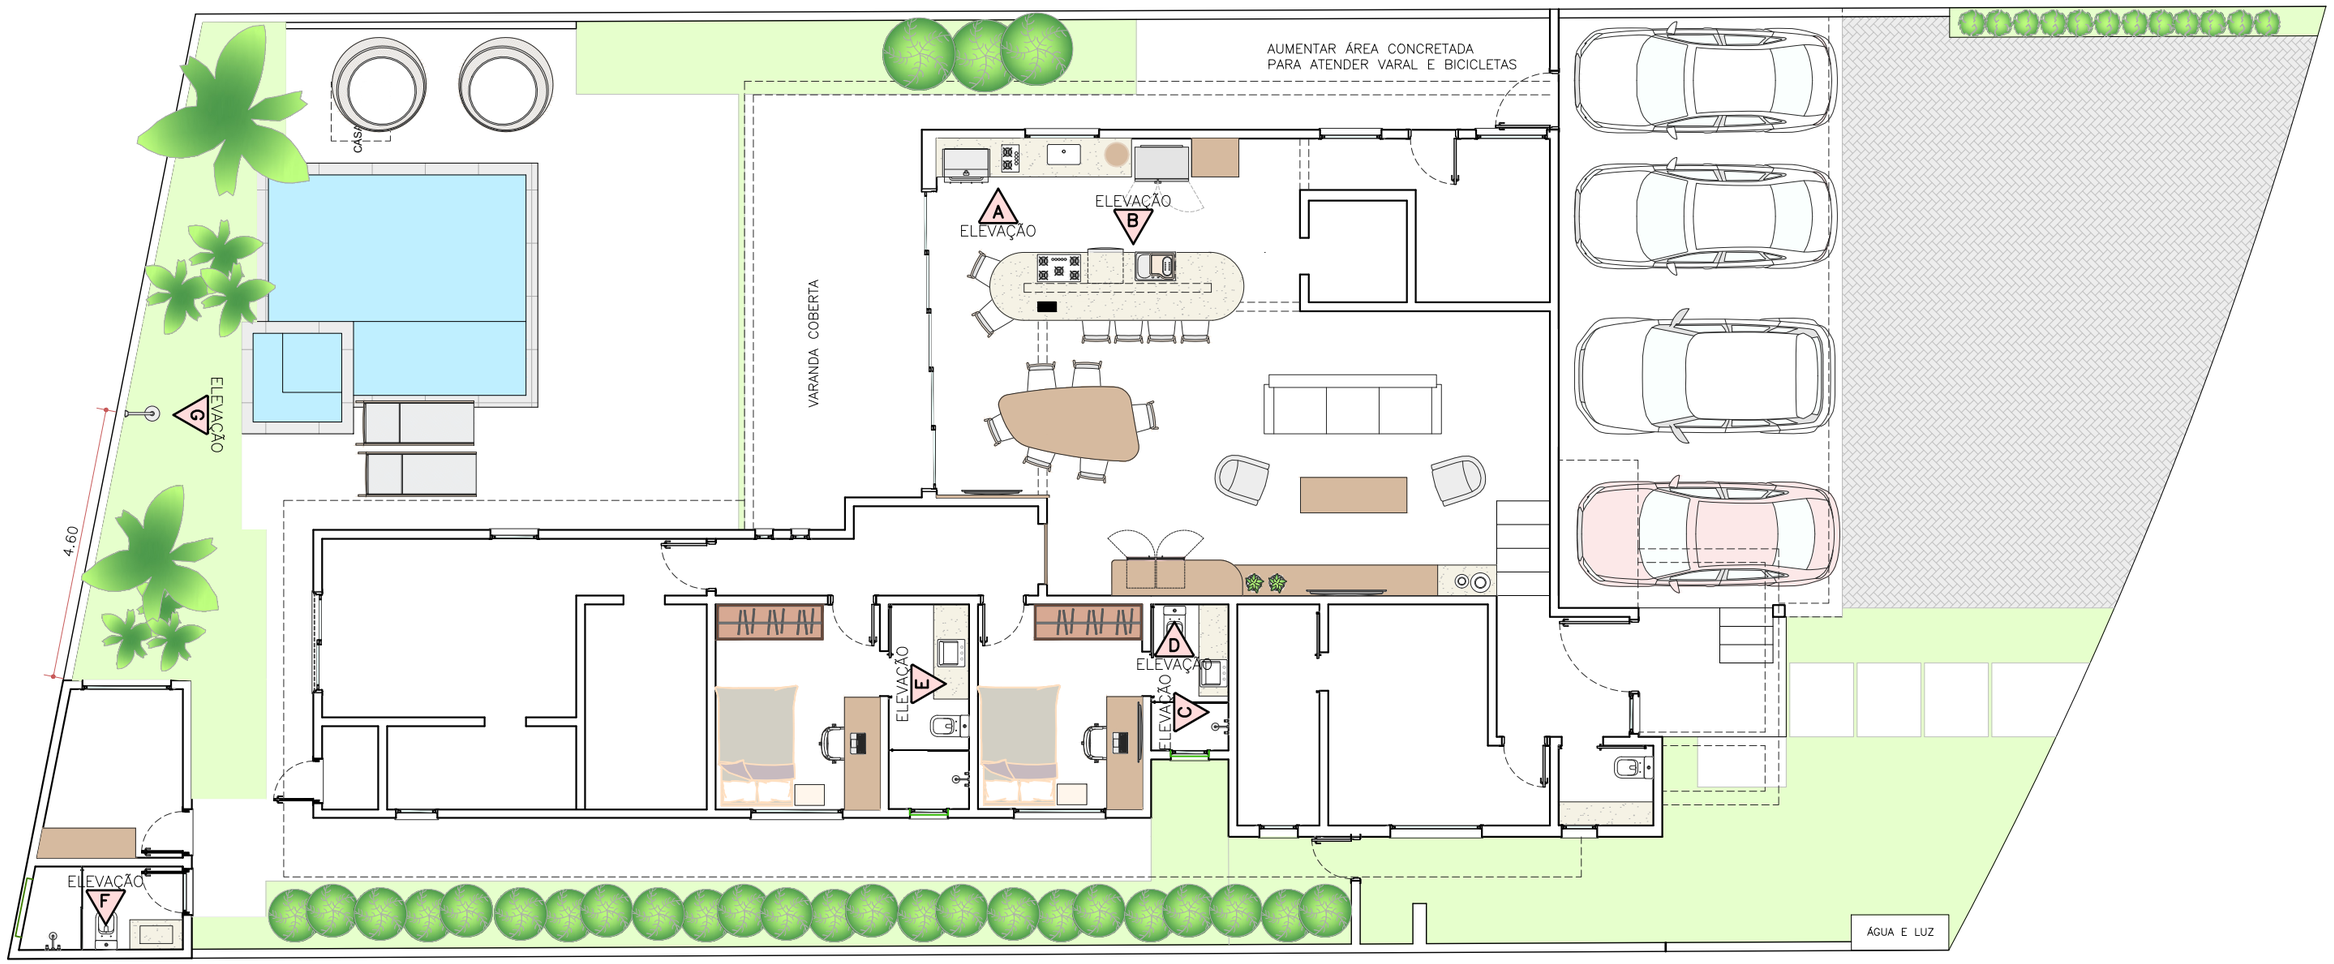

INDICAÇÃO VISTAS HIDRÁULICAS
ESC. 1:100

OBSERVAÇÕES

- COTAS EM METROS;
- COTAS DE NÍVEL EM METROS;
- CONFERIR MEDIDAS, ABERTURAS, NÍVEIS E PRUMOS NO LOCAL;
- MEDIDAS EM COTA PREVALECEM SOBRE O DESENHO;
- ESSA PRANCHA DEVE SER IMPRESSA COLORIDA;
- É RESPONSABILIDADE DO FORNECEDOR MEDIR E AJUSTAR O PROJETO;
- INSTALAR PENDENTES APÓS A INSTALAÇÃO DE MÓVEIS E MARCENARIA;

DATA 08/09/2026 | DESENHO REV00

RESPONSÁVEL
FERNANDA SUELLEM SIMÕES LIMA

LOCAL
R. **QUADRA B, LOTE 11 – CONDOMÍNIO HEVETIA PARK**

ESCALA **INDICADA** | COD. DO PROJETO **0000**

CIDADE
INDAIATUBA– SP

FASE
EXECUTIVO

FOLHA 18/39

FORMATO
A3


PROJETO
RESIDENCIAL

CLIENTE
KATIA

ASSUNTO
INDICAÇÃO VISTAS HIDRÁULICAS

SIMÕES Arquitetura & Design de Interiores
EMAIL: ARQUITETURA@SIMOESARQUITETURA.COM.BR
INSTAGRAM: @SIMOESARQUITETURA

*VERIFICAR PONTOS EXISTENTE NO LOCAL E
ADEQUAR CONFORME NECESSÁRIO

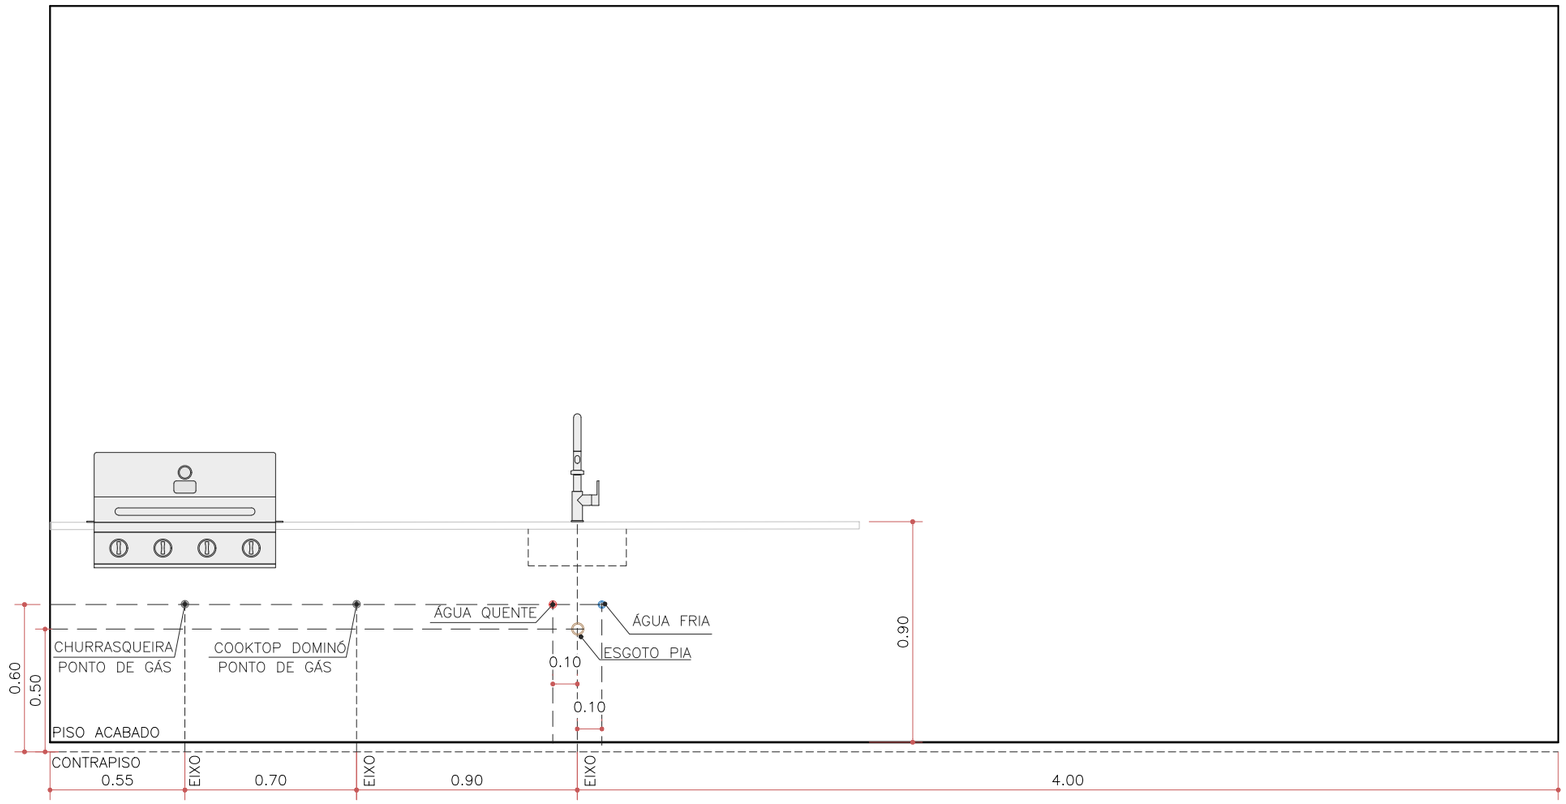

ELEVAÇÃO A – COZINHA
ESC. 1:25

OBSERVAÇÕES
- COTAS EM METROS;
- COTAS DE NÍVEL EM METROS;
- CONFERIR MEDIDAS, ABERTURAS, NÍVEIS E PRUMOS NO LOCAL;
- MEDIDAS EM COTA PREVALECEM SOBRE O DESENHO;
- ESSA PRANCHA DEVE SER IMPRESSA COLORIDA;
- É RESPONSABILIDADE DO FORNECEDOR MEDIR E AJUSTAR O PROJETO;
- INSTALAR PENDENTES APÓS A INSTALAÇÃO DE MÓVEIS E MARCENARIA;

DATA 08/09/2026 | DESENHO REV00

RESPONSÁVEL FERNANDA SUELLEM SIMÕES LIMA

LOCAL R. **QUADRA B, LOTE 11 – CONDOMÍNIO HEVETIA PARK**

ESCALA **INDICADA** | COD. DO PROJETO **0000**

CIDADE INDAIATUBA– SP

FASE EXECUTIVO

FOLHA 19 / 39

FORMATO A3


PROJETO RESIDENCIAL

CLIENTE **KATIA**

ASSUNTO VISTAS HIDRÁULICAS

SIMÕES Arquitetura & Design de Interiores
EMAIL: ARQUITETURA@SIMOESARQUITETURA.COM.BR
INSTAGRAM: @SIMOESARQUITETURA

*VERIFICAR PONTOS EXISTENTE NO LOCAL E
ADEQUAR CONFORME NECESSÁRIO

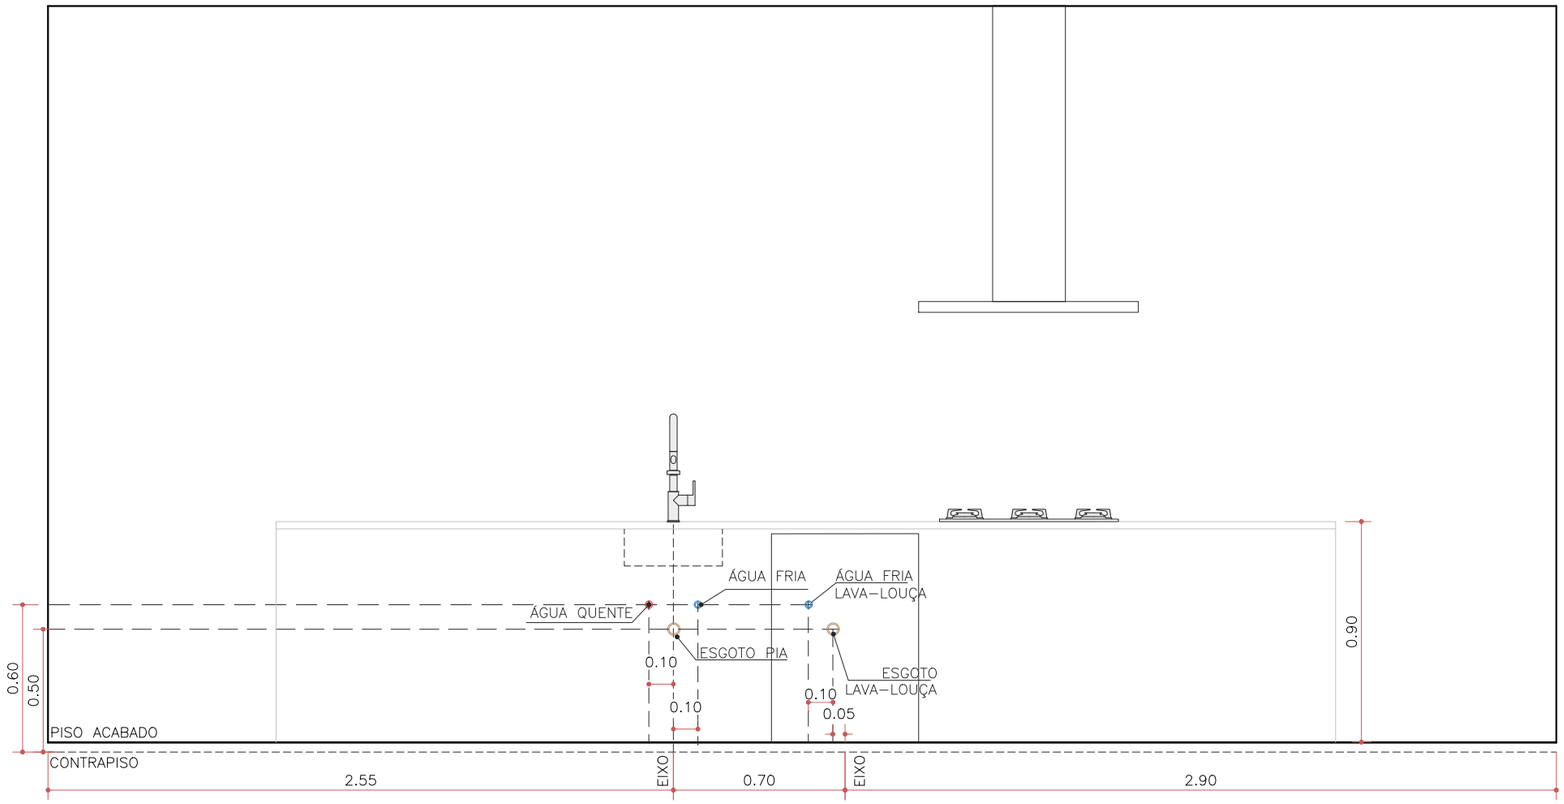

ELEVAÇÃO B – COZINHA
ESC. 1:25

OBSERVAÇÕES
- COTAS EM METROS;
- COTAS DE NÍVEL EM METROS;
- CONFERIR MEDIDAS, ABERTURAS, NÍVEIS E PRUMOS NO LOCAL;
- MEDIDAS EM COTA PREVALECEM SOBRE O DESENHO;
- ESSA PRANCHA DEVE SER IMPRESSA COLORIDA;
- É RESPONSABILIDADE DO FORNECEDOR MEDIR E AJUSTAR O PROJETO;
- INSTALAR PENDENTES APÓS A INSTALAÇÃO DE MÓVEIS E MARCENARIA;

DATA 08/09/2026 | DESENHO REV00

RESPONSÁVEL
FERNANDA SUELLEM SIMÕES LIMA

LOCAL
R. **QUADRA B, LOTE 11 – CONDOMÍNIO HEVETIA PARK**

ESCALA **INDICADA** | COD. DO PROJETO **0000**

CIDADE
INDAIATUBA– SP

FASE
EXECUTIVO

FOLHA 20 / 39

FORMATO
A3


PROJETO
RESIDENCIAL

CLIENTE
KATIA


ASSUNTO
VISTAS HIDRÁULICAS

SIMÕES Arquitetura & Design de Interiores
EMAIL: ARQUITETURA@SIMOESARQUITETURA.COM.BR
INSTAGRAM: @SIMOESARQUITETURA


*VERIFICAR PONTOS EXISTENTE NO LOCAL E ADEQUAR CONFORME NECESSÁRIO

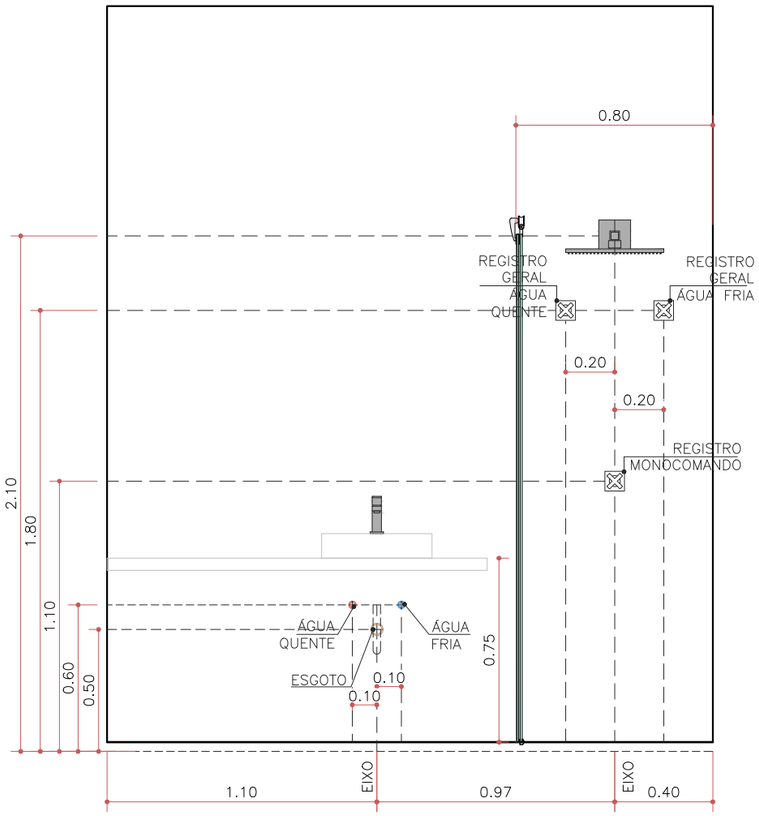

ELEVAÇÃO C – BANHO 01
ESC. 1:25

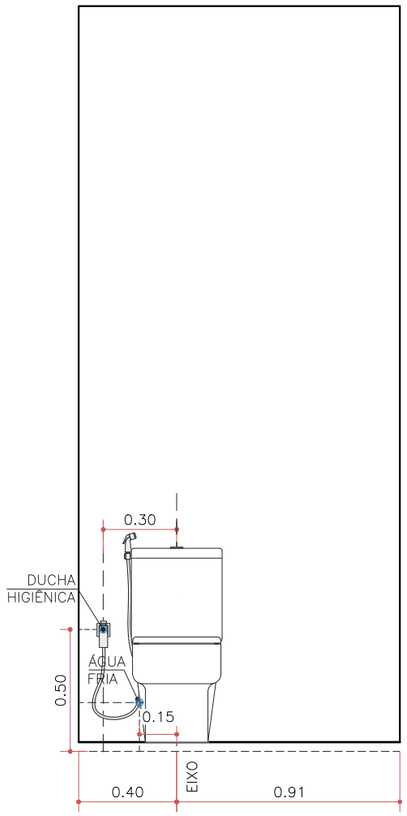

ELEVAÇÃO D – BANHO 01
ESC. 1:25

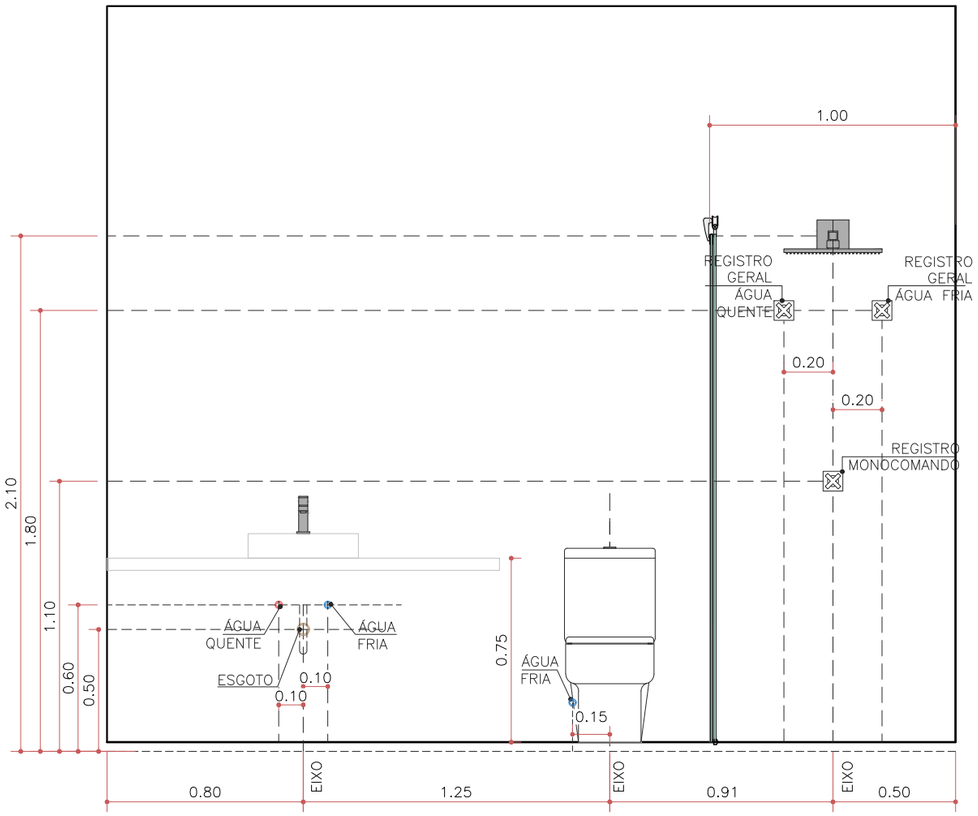

ELEVAÇÃO E – BANHO 02
ESC. 1:25

OBSERVAÇÕES
- COTAS EM METROS;
- COTAS DE NÍVEL EM METROS;
- CONFERIR MEDIDAS, ABERTURAS, NÍVEIS E PRUMOS NO LOCAL;
- MEDIDAS EM COTA PREVALECEM SOBRE O DESENHO;
- ESSA PRANCHA DEVE SER IMPRESSA COLORIDA;
- É RESPONSABILIDADE DO FORNECEDOR MEDIR E AJUSTAR O PROJETO;
- INSTALAR PENDENTES APÓS A INSTALAÇÃO DE MÓVEIS E MARCENARIA;

DATA 08/09/2026 | DESENHO REV00

RESPONSÁVEL
FERNANDA SUELLEM SIMÕES LIMA

LOCAL
R. **QUADRA B, LOTE 11 – CONDOMÍNIO HEVETIA PARK**

ESCALA **INDICADA** | COD. DO PROJETO **0000**

CIDADE
INDAIATUBA– SP

FASE
EXECUTIVO

FOLHA 21 / 39

FORMATO
A3


PROJETO
RESIDENCIAL

CLIENTE
KATIA


ASSUNTO
VISTAS HIDRÁULICAS

SIMÕES Arquitetura & Design de Interiores
EMAIL: ARQUITETURA@SIMOESARQUITETURA.COM.BR
INSTAGRAM: @SIMOESARQUITETURA

*VERIFICAR PONTOS EXISTENTE NO LOCAL E ADEQUAR CONFORME NECESSÁRIO

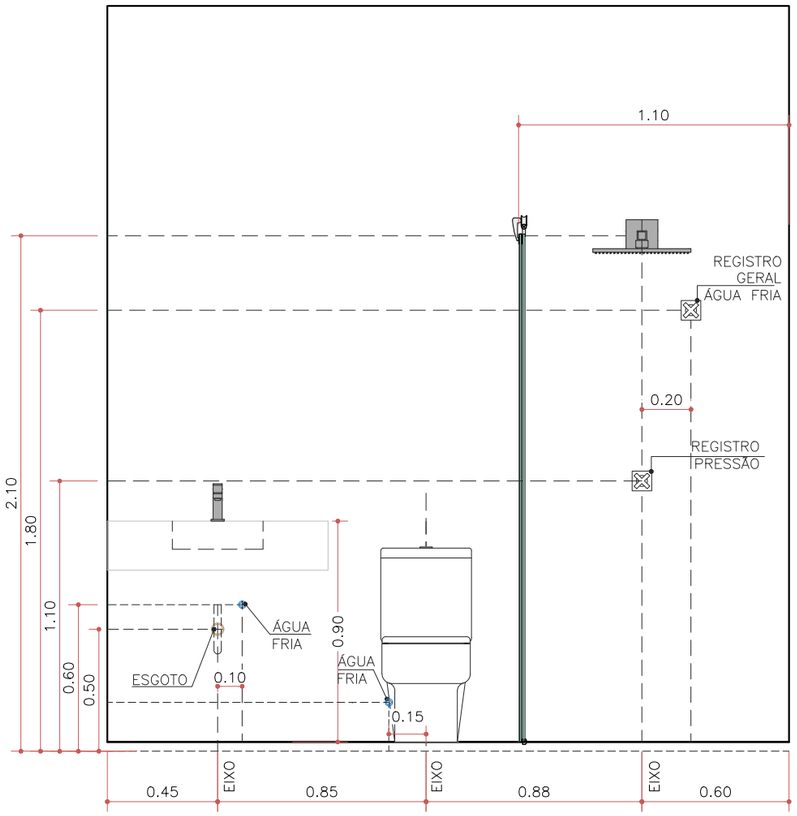

ELEVAÇÃO F – BANHO EXTERNO
ESC. 1:25

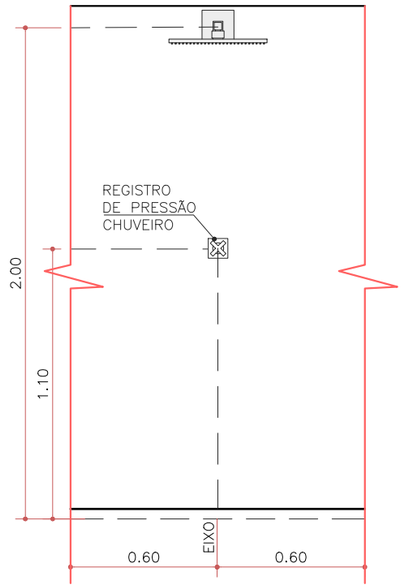

ELEVAÇÃO G – ÁREA EXTERNA
ESCALA 1:25

OBSERVAÇÕES
- COTAS EM METROS;
- COTAS DE NÍVEL EM METROS;
- CONFERIR MEDIDAS, ABERTURAS, NÍVEIS E PRUMOS NO LOCAL;
- MEDIDAS EM COTA PREVALECEM SOBRE O DESENHO;
- ESSA PRANCHA DEVE SER IMPRESSA COLORIDA;
- É RESPONSABILIDADE DO FORNECEDOR MEDIR E AJUSTAR O PROJETO;
- INSTALAR PENDENTES APÓS A INSTALAÇÃO DE MÓVEIS E MARCENARIA;

DATA 08/09/2026 | DESENHO REV00

RESPONSÁVEL
FERNANDA SUELLEM SIMÕES LIMA

LOCAL
R. **QUADRA B, LOTE 11 – CONDOMÍNIO HEVETIA PARK**

ESCALA **INDICADA** | COD. DO PROJETO **0000**

CIDADE
INDAIATUBA– SP

FASE
EXECUTIVO

FOLHA 22 / 39


FORMATO
A3

PROJETO
RESIDENCIAL


CLIENTE
KATIA

ASSUNTO
VISTAS HIDRÁULICAS


SIMÕES Arquitetura & Design de Interiores
EMAIL: ARQUITETURA@SIMOESARQUITETURA.COM.BR
INSTAGRAM: @SIMOESARQUITETURA

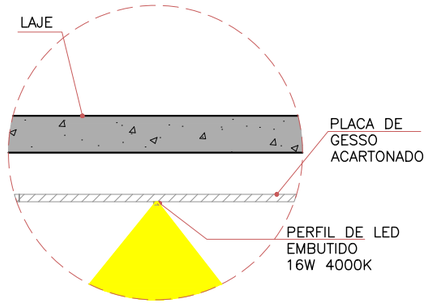

DET. 01 – PERFIL DE LED
ESC. 1:25

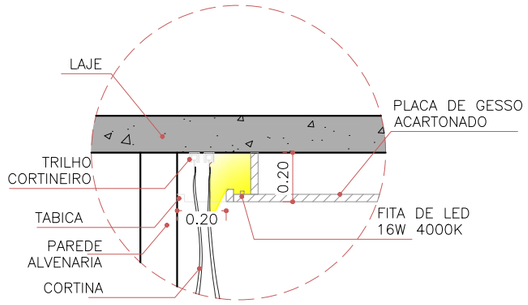

DET. 02 – CORTINEIRO COM ILUM. LED
ESC. 1:25

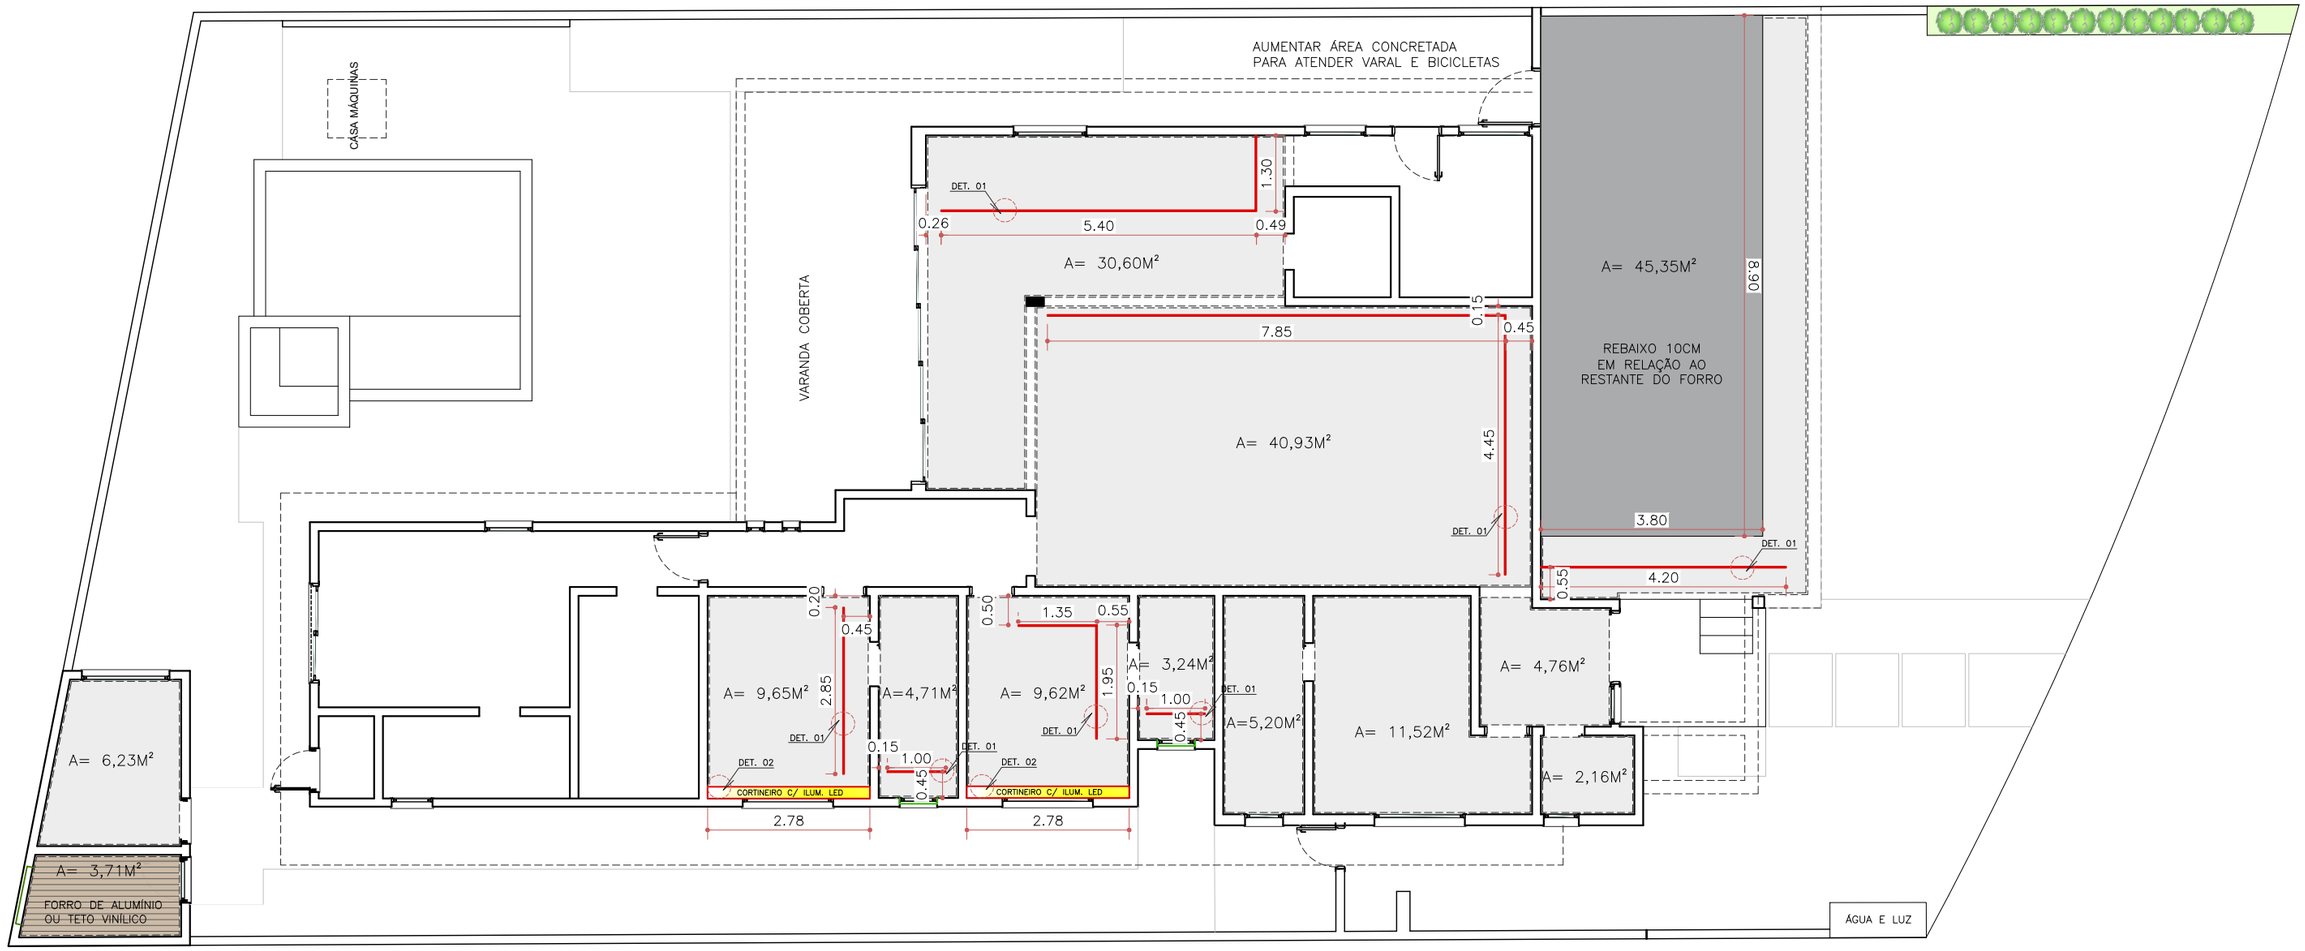

FORRO DE GESSO
ESC. 1:100

OBSERVAÇÕES

- COTAS EM METROS;
- COTAS DE NÍVEL EM METROS;
- CONFERIR MEDIDAS, ABERTURAS, NÍVEIS E PRUMOS NO LOCAL;
- MEDIDAS EM COTA PREVALECEM SOBRE O DESENHO;
- ESSA PRANCHA DEVE SER IMPRESSA COLORIDA;
- É RESPONSABILIDADE DO FORNECEDOR MEDIR E AJUSTAR O PROJETO;
- INSTALAR PENDENTES APÓS A INSTALAÇÃO DE MÓVEIS E MARCENARIA;

DATA: 08/09/2026 | DESENHO: REV00

RESPONSÁVEL: FERNANDA SUELLEM SIMÕES LIMA

LOCAL: R. **QUADRA B, LOTE 11 – CONDOMÍNIO HEVETIA PARK**

ESCALA: **INDICADA** | COD. DO PROJETO: **0000**

CIDADE: INDAIATUBA– SP

FASE: EXECUTIVO

FOLHA: 23 / 39

FORMATO: A3

PROJETO: RESIDENCIAL

CLIENTE: **KATIA**

ASSUNTO: FORRO DE GESSO

SIMÕES Arquitetura & Design de Interiores
EMAIL: ARQUITETURA@SIMOESARQUITETURA.COM.BR
INSTAGRAM: @SIMOESARQUITETURA

PONTOS EM VERMELHO 220V – PONTOS EM AZUL 110V

TOMADAS

- SIMPLES/DUPLA 220V DE PISO
- SIMPLES/DUPLA/TRIPLA 220V A 30CM
- SIMPLES/DUPLA/TRIPLA 220V A 60CM
- SIMPLES/DUPLA/TRIPLA 220V A 80CM
- SIMPLES/DUPLA/TRIPLA 220V A 90CM
- DUPLA 220V A 100CM (no frontão)
- SIMPLES/DUPLA/TRIPLA 220V A 110CM
- SIMPLES/DUPLA/TRIPLA 220V A 140CM
- SIMPLES/DUPLA/TRIPLA 220V A 230CM
- TOMADA DE TETO 220V
- TOMADA PARA TOALHEIRO ELÉTRICO 130CM
- TOMADA P/ CORTINA AUTOMATIZADA

PONTOS

- TV A 30CM/110CM
- REDE ETHERNET A 30CM/110CM
- INTERFONE A 110CM
- LÓGICA NO PISO / A 30CM / TETO
- BOTÃO DA CAMPAINHA A 110CM / CAMPAINHA A 220CM
- CÂMERA DE SEGURANÇA
- CAIXA DE SOM

CIRCUITOS

- QUADRO DE DISTRIBUIÇÃO DE FORÇA
- QUADRO DE DADOS/TELEFONIA

LUMINÁRIAS



Arandela EFFEKT | 2 FACHOS ABERTOS 2x4W – STELLA – Interna e Externa h= altura no ponto



Balizador Lisse Newline Embutir 12x8cm Led 6W 2700K – IN10471LED



Balizador Led Alumínio Preto 3w 3000k Ip65 – Yamamura



ESPETO LED SMD 38° 6W PRETO – LUZ 3000K – EvoLed



Iluminação subaquática em LED 18w



Refletor Holofote MicroLED Slim 100W – 6000k



ESPETO LED SMD 38° 6W PRETO – LUZ 3000K – EvoLed



ponto para caixa de som



Embutido de Piso e Solo Flat In LED 4w 2700K IP67 – Interlight IL3927




EFFEKT | 1 FACHO ABERTO – STELLA 4W 3000K



SPOT DE EMBUTIR FACE PLANA – DICRÓICA MR16 LED 7W – EvoLed



EMBUTIDO FLAT MINI DICRÓICA GU10 MR11 4W – NEW LINE 3000K

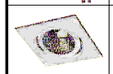

EMBUTIDO FLAT PAR20 E27 9W – NEWLINE 3000K



SPOT DE EMBUTIR Lâmpada Led AR70 4.8W – Save Energy



SPOT DE EMBUTIR Lâmpada LED AR111 Refletora 13W 2700K – Save Energy



SPOT SOBREPOR PAR20 E27 9W – NEWLINE 3000K (EXTERNO)



spot Sobrepor Orion Redondo Par 20 9W NEWLINE



DEEP : LUMINÁRIA DE EMBUTIR RECUADA 12W,17W OU 22W–STELLA



SPOT DE EMBUTIR LED PICCO 2 MÓDULOS



SPOT DE EMBUTIR LED PICCO 3 MÓDULOS

LUMINÁRIAS



SPOT DE EMBUTIR LED PICCO 4 MÓDULOS



SPOT DE EMBUTIR LED PICCO 6 MÓDULOS (PÉ DIREITO ALTO)



SPOT DE EMBUTIR RECUADO FLAT RETANGULAR DUPLO AR70 4 LAMPADAS IN65124 – ANGULO 15°



SPOT DE EMBUTIR RECUADO FLAT RETANGULAR DUPLO AR70 2 LAMPADAS IN65124 – ANGULO 15°



Spot Recuado AR111 Embutir 3xGU10 Newline IN51354 – ANGULO 25°



Spot Recuado AR111 Embutir 4xGU10 Newline IN51354 – ANGULO 25°



Spot Recuado AR111 Embutir 2xGU10 Newline IN51354 – ANGULO 25°


PERFIL LED DE SOBREPOR PRETO 2m Itamonte LED 5050 60led's 14,4W 4000K



PERFIL EMBUTIDO LED LED 16W/m 3000K



MANGUEIRA DE LED (EXTERNA) Led Double Line 10W/m 3000K

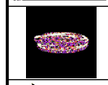

FITA DE LED (INTERNA) LED 16W/m 3000K



TRILHO ELETRIFICADO C/ SPOTS

Ponto de Iluminaçãona Parede h= Altura definida no ponto



Ponto para Pendente ou Lustre

Iluminação dentro da churrasqueira

AR CONDICIONADO



VENTILADOR DE TETO



SPLIT CASSETE



HI–WALL OU MULTI SPLIT

OBSERVAÇÕES

- COTAS EM METROS;
- COTAS DE NÍVEL EM METROS;
- CONFERIR MEDIDAS, ABERTURAS, NÍVEIS E PRUMOS NO LOCAL;
- MEDIDAS EM COTA PREVALECEM SOBRE O DESENHO;
- ESSA PRANCHA DEVE SER IMPRESSA COLORIDA;
- É RESPONSABILIDADE DO FORNECEDOR MEDIR E AJUSTAR O PROJETO;
- INSTALAR PENDENTES APÓS A INSTALAÇÃO DE MÓVEIS E MARCENARIA;

DATA: 08/09/2026 | DESENHO: REV00

RESPONSÁVEL: FERNANDA SUELLEM SIMÕES LIMA

LOCAL: R. **QUADRA B, LOTE 11 – CONDOMÍNIO HEVETIA PARK**

ESCALA: **INDICADA** | COD. DO PROJETO: **0000**

CIDADE: INDAIATUBA– SP

FASE: EXECUTIVO

FOLHA: 24 / 39

FORMATO: A3

PROJETO: RESIDENCIAL


CLIENTE: **KATIA**

ASSUNTO: LEGENDA ELÉTRICA

SIMÕES Arquitetura & Design de Interiores

EMAIL: ARQUITETURA@SIMOESARQUITETURA.COM.BR
INSTAGRAM: @SIMOESARQUITETURA

*VERIFICAR PONTOS EXISTENTE NO LOCAL E ADEQUAR CONFORME NECESSÁRIO

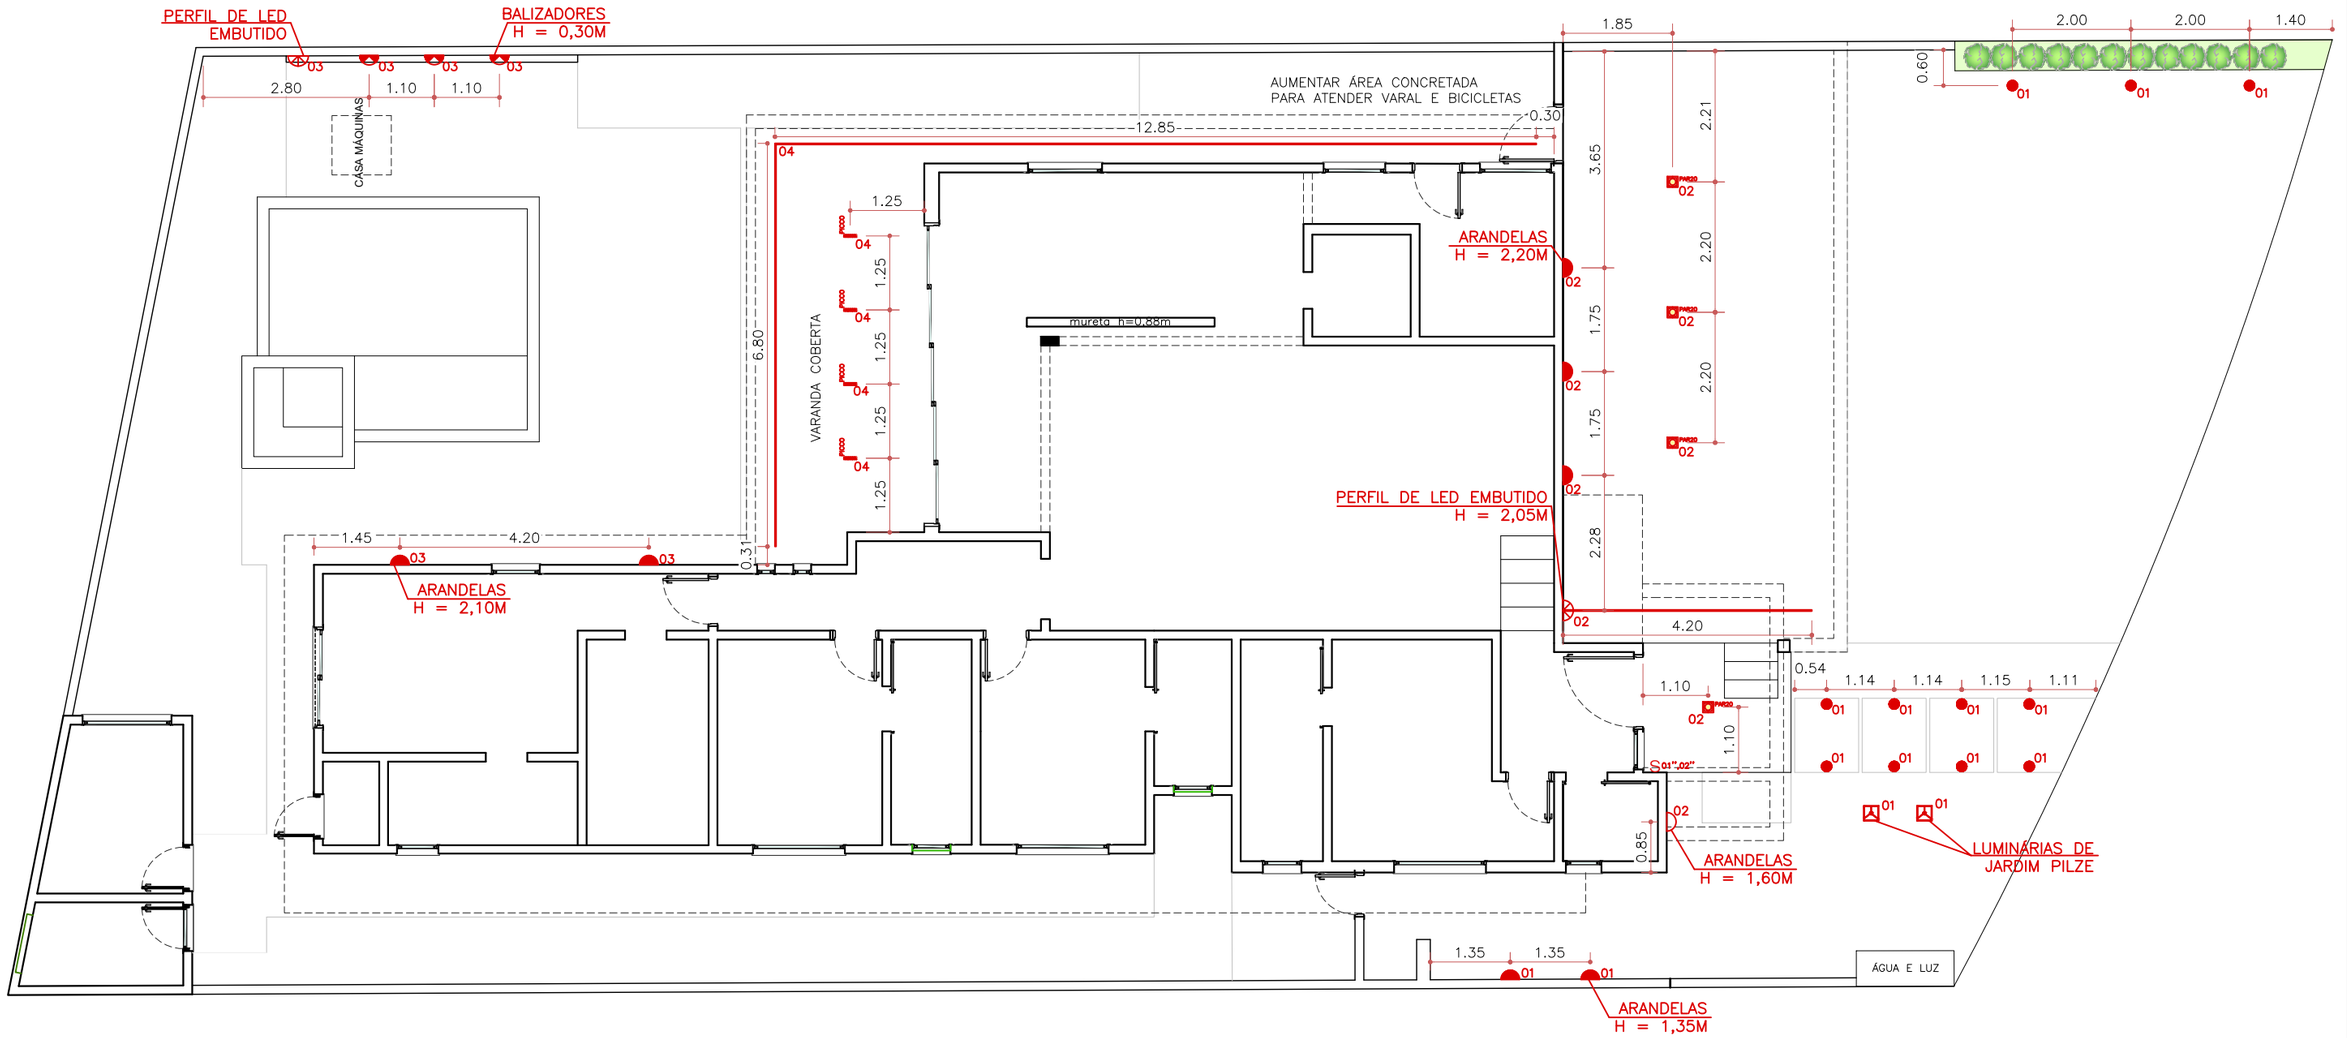

ILUMINAÇÃO ÁREA EXTERNA
ESC. 1:100

OBSERVAÇÕES
- COTAS EM METROS;
- COTAS DE NÍVEL EM METROS;
- CONFERIR MEDIDAS, ABERTURAS, NÍVEIS E PRUMOS NO LOCAL;
- MEDIDAS EM COTA PREVALECEM SOBRE O DESENHO;
- ESSA PRANCHA DEVE SER IMPRESSA COLORIDA;
- É RESPONSABILIDADE DO FORNECEDOR MEDIR E AJUSTAR O PROJETO;
- INSTALAR PENDENTES APÓS A INSTALAÇÃO DE MÓVEIS E MARCENARIA;

DATA 08/09/2026 | DESENHO REV00

RESPONSÁVEL FERNANDA SUELLEM SIMÕES LIMA

LOCAL R. QUADRA B, LOTE 11 – CONDOMÍNIO HEVETIA PARK

ESCALA INDICADA | COD. DO PROJETO 0000

CIDADE INDAIATUBA– SP

FASE EXECUTIVO

FOLHA 25 / 39

FORMATO A3


PROJETO RESIDENCIAL

CLIENTE KATIA

ASSUNTO ILUMINAÇÃO

SIMÕES Arquitetura & Design de Interiores
EMAIL: ARQUITETURA@SIMOESARQUITETURA.COM.BR
INSTAGRAM: @SIMOESARQUITETURA

*VERIFICAR PONTOS EXISTENTE NO LOCAL E ADEQUAR CONFORME NECESSÁRIO

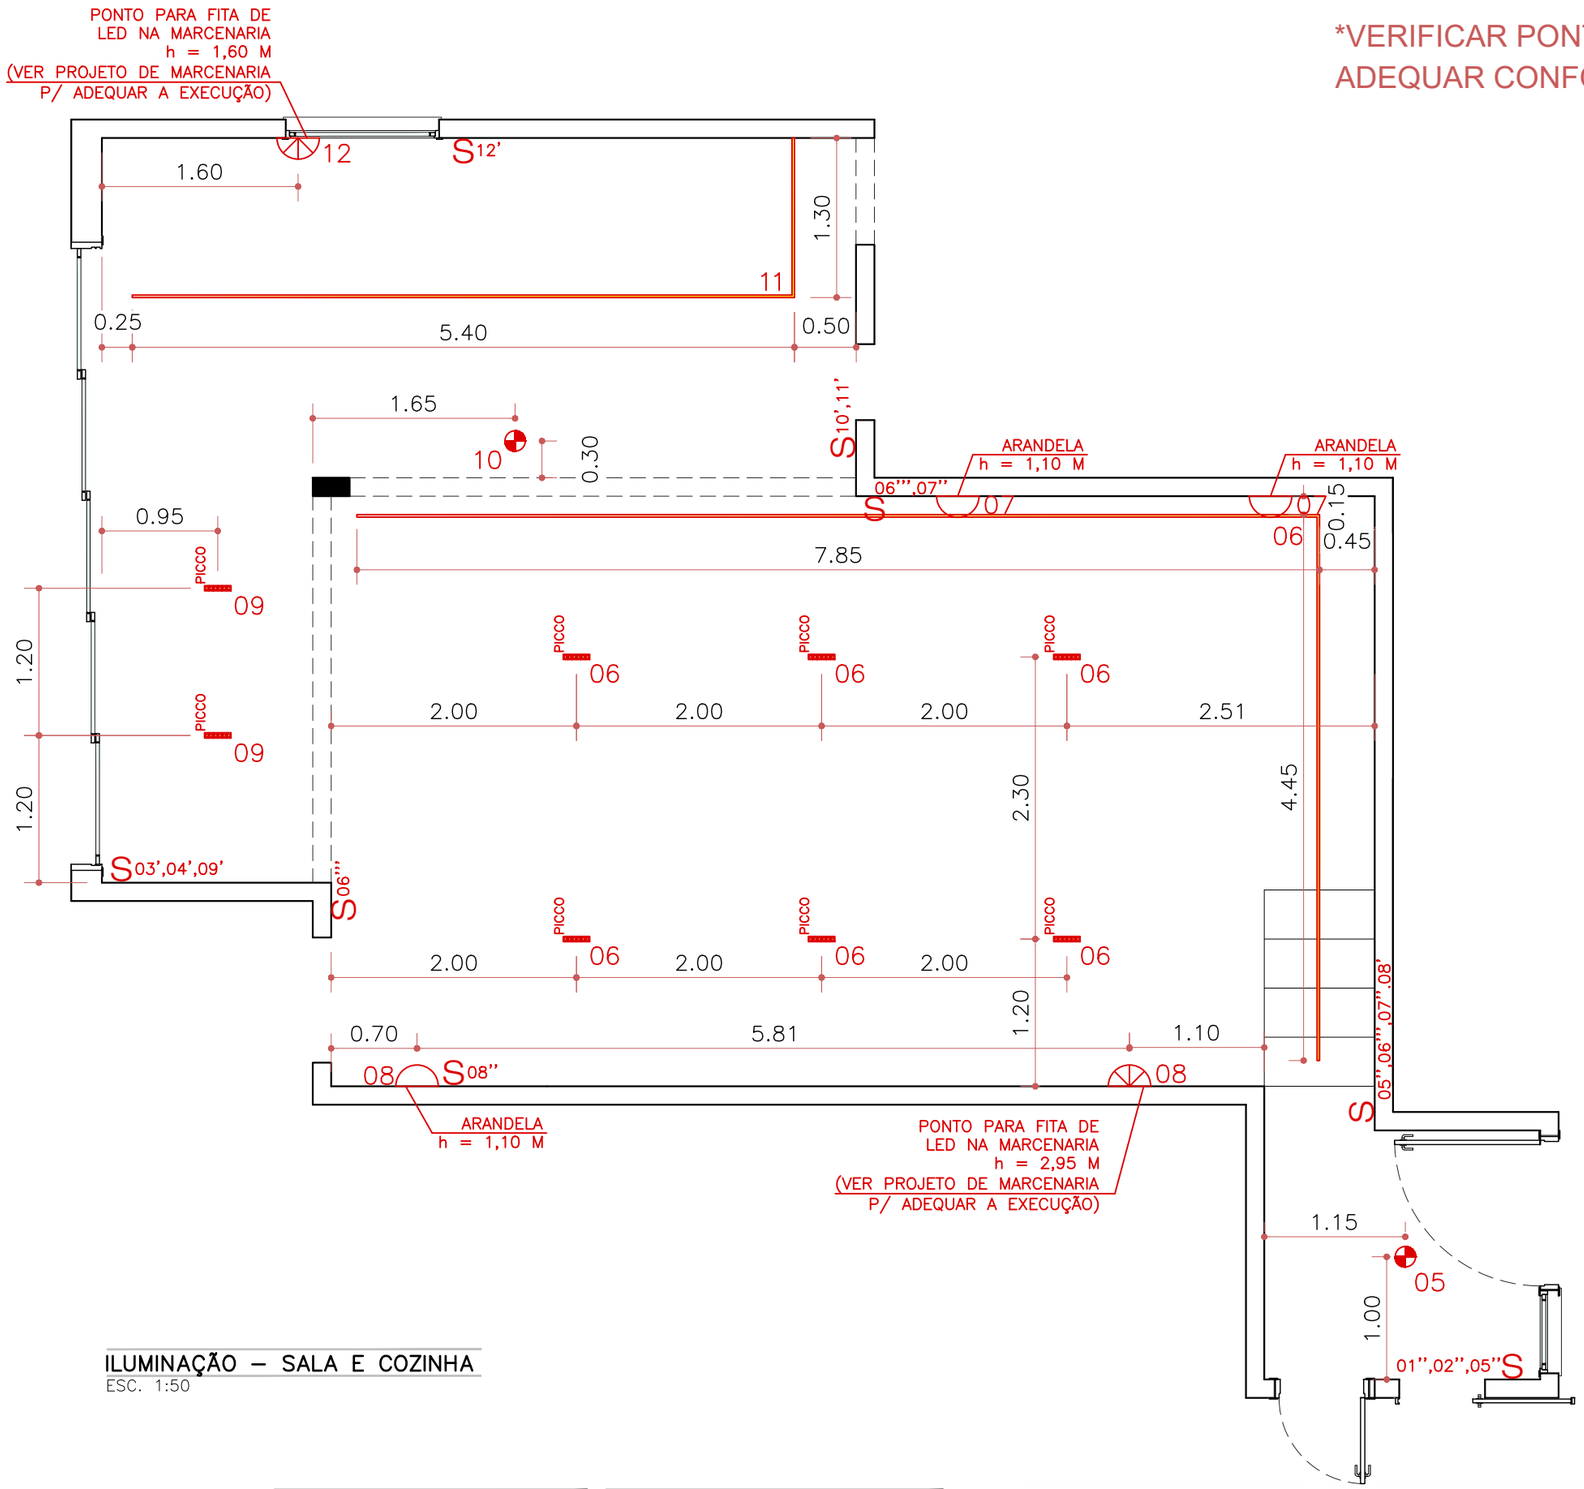

ILUMINAÇÃO – SALA E COZINHA

ESC. 1:50

OBSERVAÇÕES

- COTAS EM METROS;
- COTAS DE NÍVEL EM METROS;
- CONFERIR MEDIDAS, ABERTURAS, NÍVEIS E PRUMOS NO LOCAL;
- MEDIDAS EM COTA PREVALECEM SOBRE O DESENHO;
- ESSA PRANCHA DEVE SER IMPRESSA COLORIDA;
- É RESPONSABILIDADE DO FORNECEDOR MEDIR E AJUSTAR O PROJETO;
- INSTALAR PENDENTES APÓS A INSTALAÇÃO DE MÓVEIS E MARCENARIA;

DATA 08/09/2026 | DESENHO REV00

RESPONSÁVEL FERNANDA SUELLEM SIMÕES LIMA

LOCAL R. QUADRA B, LOTE 11 – CONDOMÍNIO HEVETIA PARK

ESCALA INDICADA | COD. DO PROJETO 0000

CIDADE INDAIATUBA– SP

FASE EXECUTIVO

FOLHA 26 / 39

FORMATO A3


PROJETO RESIDENCIAL

CLIENTE KATIA

ASSUNTO ILUMINAÇÃO

SIMÕES Arquitetura & Design de Interiores
EMAIL: ARQUITETURA@SIMOESARQUITETURA.COM.BR
INSTAGRAM: @SIMOESARQUITETURA

*VERIFICAR PONTOS EXISTENTE NO LOCAL E
ADEQUAR CONFORME NECESSÁRIO

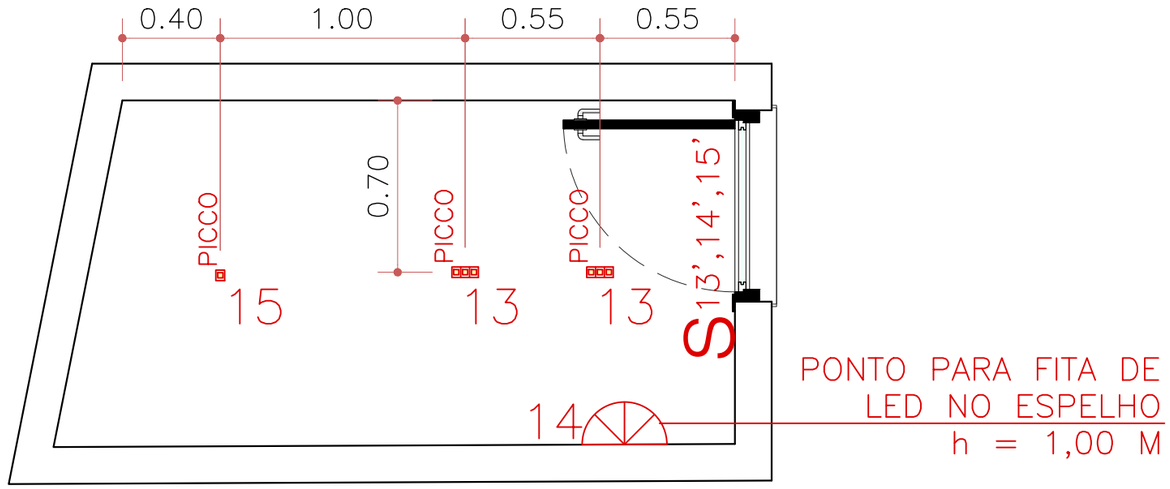

ILUMINAÇÃO – BANHO EXTERNO

ESC. 1:25

OBSERVAÇÕES
- COTAS EM METROS;
- COTAS DE NÍVEL EM METROS;
- CONFERIR MEDIDAS, ABERTURAS, NÍVEIS E PRUMOS NO LOCAL;
- MEDIDAS EM COTA PREVALECEM SOBRE O DESENHO;
- ESSA PRANCHA DEVE SER IMPRESSA COLORIDA;
- É RESPONSABILIDADE DO FORNECEDOR MEDIR E AJUSTAR O PROJETO;
- INSTALAR PENDENTES APÓS A INSTALAÇÃO DE MÓVEIS E MARCENARIA;

DATA 08/09/2026 | DESENHO REV00

RESPONSÁVEL
FERNANDA SUELLEM SIMÕES LIMA

LOCAL
R. **QUADRA B, LOTE 11 – CONDOMÍNIO HEVETIA PARK**

ESCALA **INDICADA** | COD. DO PROJETO **0000**

CIDADE
INDAIATUBA– SP

FASE
EXECUTIVO

FOLHA 27 / 39

FORMATO
A3


PROJETO
RESIDENCIAL

CLIENTE
KATIA

ASSUNTO
ILUMINAÇÃO

SIMÕES Arquitetura & Design de Interiores
EMAIL: ARQUITETURA@SIMOESARQUITETURA.COM.BR
INSTAGRAM: @SIMOESARQUITETURA

*VERIFICAR PONTOS EXISTENTE NO LOCAL E ADEQUAR CONFORME NECESSÁRIO

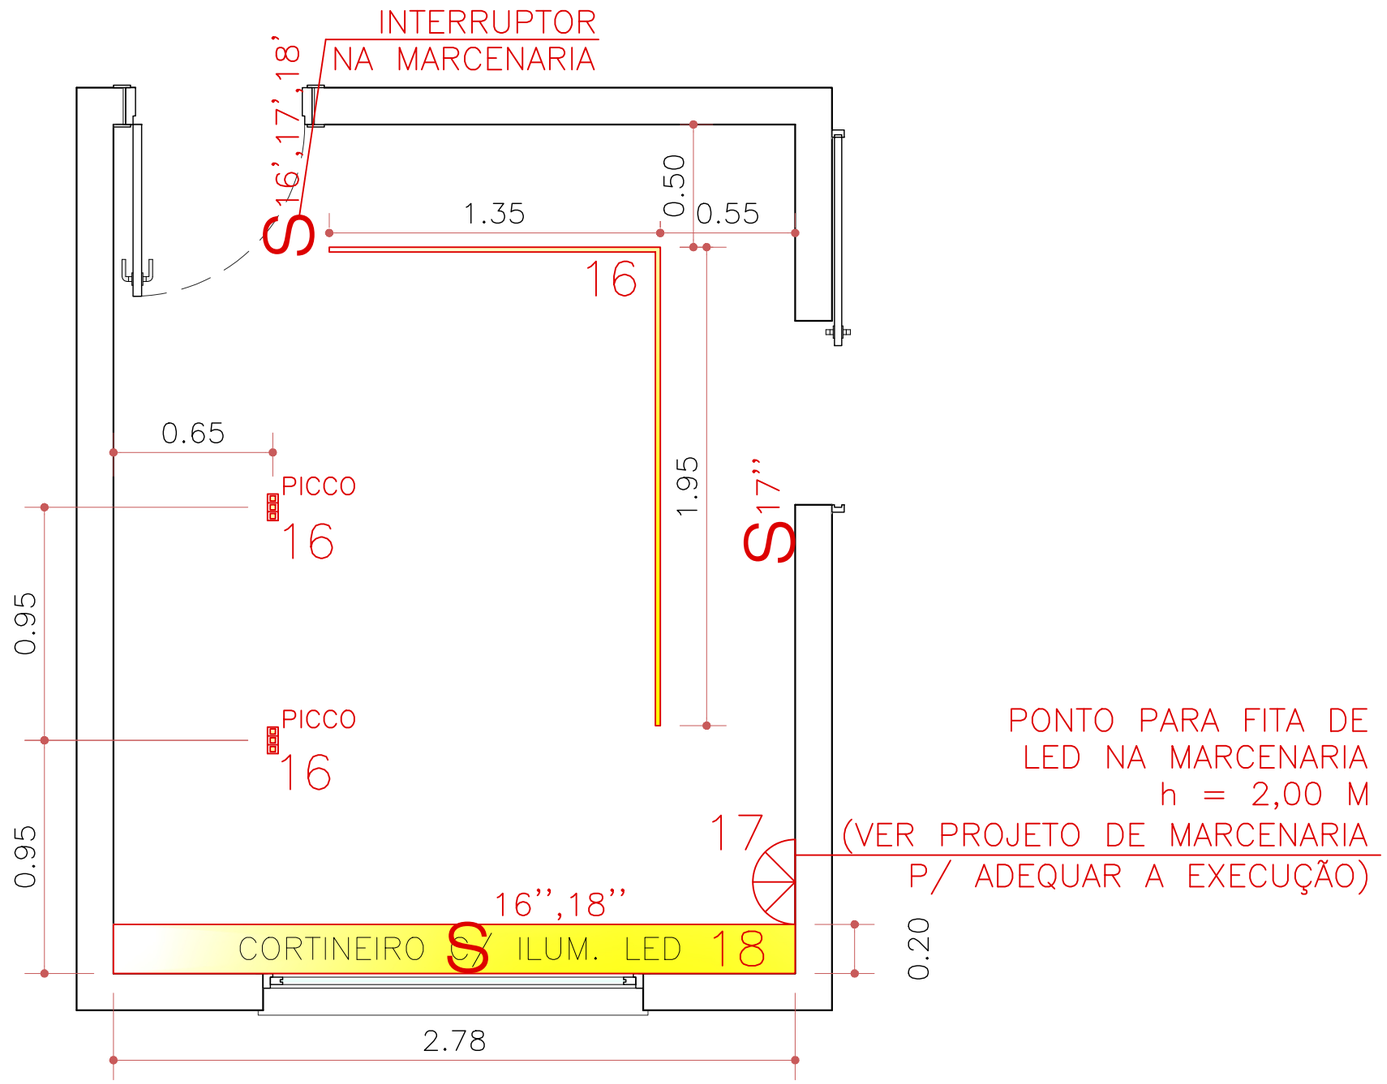

PONTO PARA FITA DE LED NA MARCENARIA h = 2,00 M

ILUMINAÇÃO – SUÍTE 01

ESC. 1:25

OBSERVAÇÕES
- COTAS EM METROS;
- COTAS DE NÍVEL EM METROS;
- CONFERIR MEDIDAS, ABERTURAS, NÍVEIS E PRUMOS NO LOCAL;
- MEDIDAS EM COTA PREVALECEM SOBRE O DESENHO;
- ESSA PRANCHA DEVE SER IMPRESSA COLORIDA;
- É RESPONSABILIDADE DO FORNECEDOR MEDIR E AJUSTAR O PROJETO;
- INSTALAR PENDENTES APÓS A INSTALAÇÃO DE MÓVEIS E MARCENARIA;

DATA 08/09/2026 | DESENHO REV00

RESPONSÁVEL FERNANDA SUELLEM SIMÕES LIMA

LOCAL R. QUADRA B, LOTE 11 – CONDOMÍNIO HEVETIA PARK

ESCALA INDICADA | COD. DO PROJETO 0000

CIDADE INDAIATUBA– SP

FASE EXECUTIVO

FOLHA 28 / 39

FORMATO A3


PROJETO RESIDENCIAL

CLIENTE KATIA

ASSUNTO ILUMINAÇÃO

SIMÕES Arquitetura & Design de Interiores
EMAIL: ARQUITETURA@SIMOESARQUITETURA.COM.BR
INSTAGRAM: @SIMOESARQUITETURA

*VERIFICAR PONTOS EXISTENTE NO LOCAL E
ADEQUAR CONFORME NECESSÁRIO

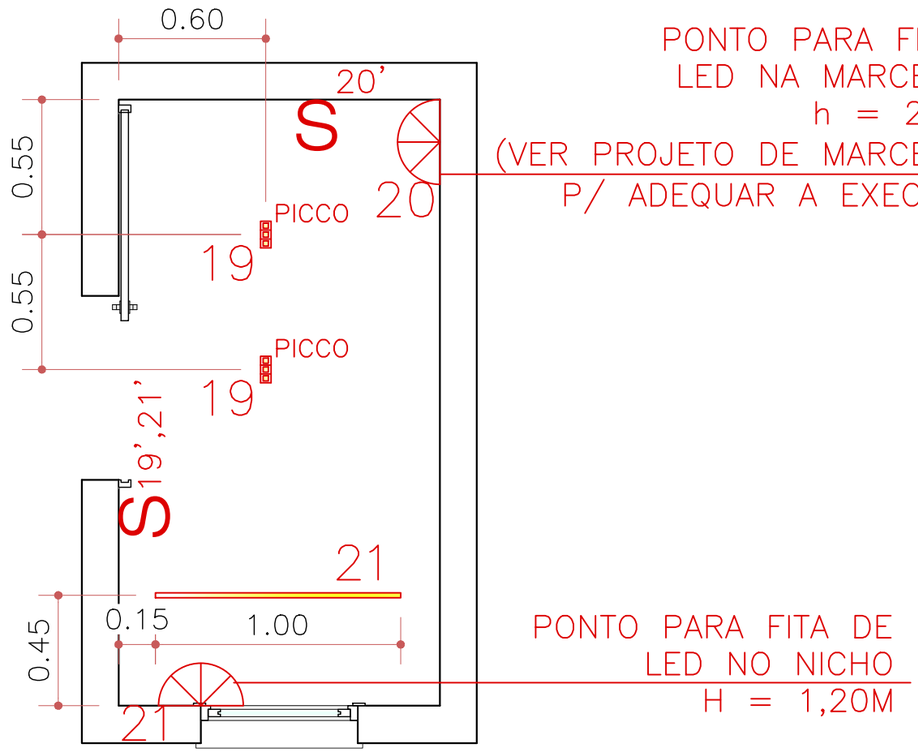

ILUMINAÇÃO – BANHO 01

ESC. 1:25

OBSERVAÇÕES
- COTAS EM METROS;
- COTAS DE NÍVEL EM METROS;
- CONFERIR MEDIDAS, ABERTURAS, NÍVEIS E PRUMOS NO LOCAL;
- MEDIDAS EM COTA PREVALECEM SOBRE O DESENHO;
- ESSA PRANCHA DEVE SER IMPRESSA COLORIDA;
- É RESPONSABILIDADE DO FORNECEDOR MEDIR E AJUSTAR O PROJETO;
- INSTALAR PENDENTES APÓS A INSTALAÇÃO DE MÓVEIS E MARCENARIA;

DATA 08/09/2026 | DESENHO REV00

RESPONSÁVEL FERNANDA SUELLEM SIMÕES LIMA

LOCAL R. **QUADRA B, LOTE 11 – CONDOMÍNIO HEVETIA PARK**

ESCALA **INDICADA** | COD. DO PROJETO **0000**

CIDADE INDAIATUBA– SP

FASE EXECUTIVO

FOLHA 29 / 39

FORMATO A3


PROJETO RESIDENCIAL

CLIENTE **KATIA**

ASSUNTO ILUMINAÇÃO

SIMÕES Arquitetura & Design de Interiores
EMAIL: ARQUITETURA@SIMOESARQUITETURA.COM.BR
INSTAGRAM: @SIMOESARQUITETURA

*VERIFICAR PONTOS EXISTENTE NO LOCAL E ADEQUAR CONFORME NECESSÁRIO

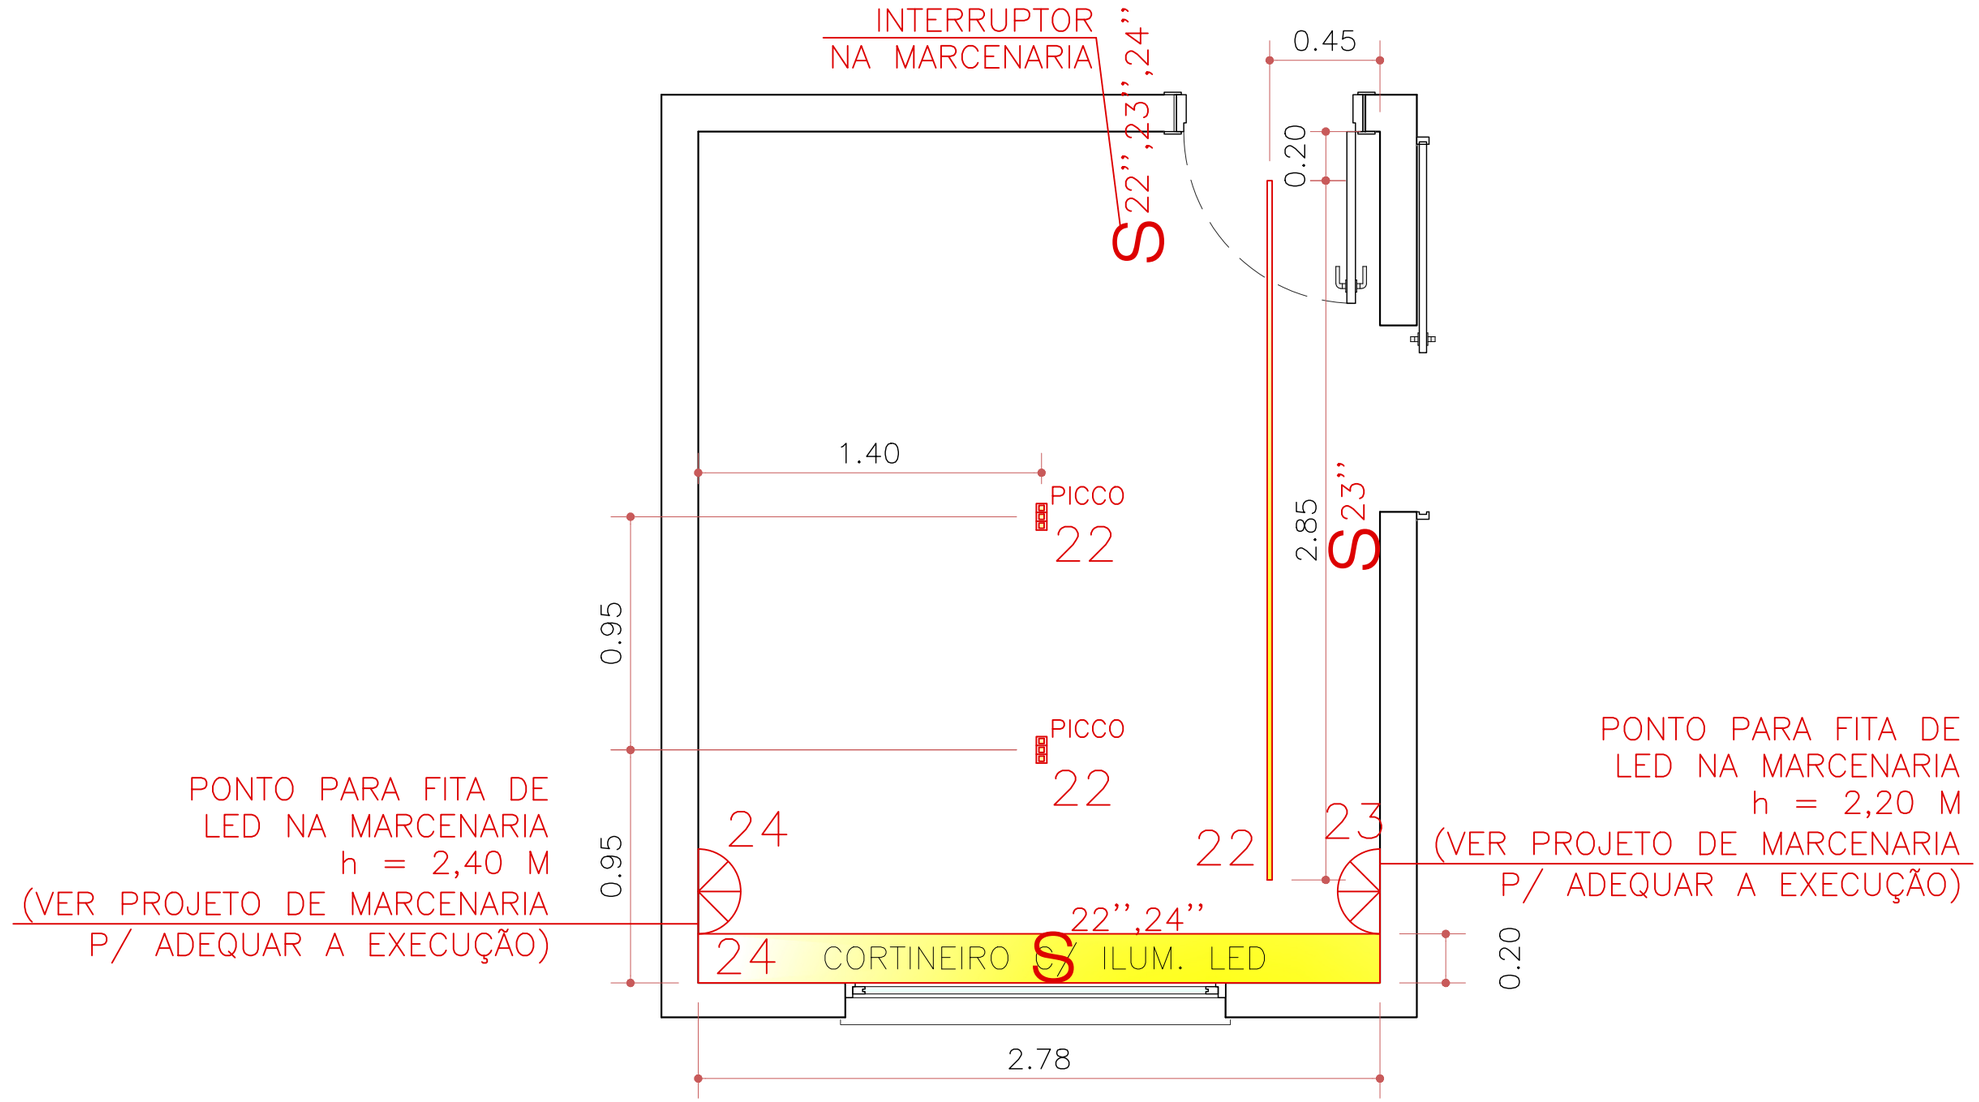

PONTO PARA FITA DE LED NA MARCENARIA h = 2,40 M (VER PROJETO DE MARCENARIA P/ ADEQUAR A EXECUÇÃO)

PONTO PARA FITA DE LED NA MARCENARIA h = 2,20 M (VER PROJETO DE MARCENARIA P/ ADEQUAR A EXECUÇÃO)

ILUMINAÇÃO – SUÍTE 02

ESC. 1:25

OBSERVAÇÕES
- COTAS EM METROS;
- COTAS DE NÍVEL EM METROS;
- CONFERIR MEDIDAS, ABERTURAS, NÍVEIS E PRUMOS NO LOCAL;
- MEDIDAS EM COTA PREVALECEM SOBRE O DESENHO;
- ESSA PRANCHA DEVE SER IMPRESSA COLORIDA;
- É RESPONSABILIDADE DO FORNECEDOR MEDIR E AJUSTAR O PROJETO;
- INSTALAR PENDENTES APÓS A INSTALAÇÃO DE MÓVEIS E MARCENARIA;

DATA 08/09/2026 | DESENHO REV00

RESPONSÁVEL FERNANDA SUELLEM SIMÕES LIMA

LOCAL R. QUADRA B, LOTE 11 – CONDOMÍNIO HEVETIA PARK

ESCALA INDICADA | COD. DO PROJETO 0000

CIDADE INDAIATUBA– SP

FASE EXECUTIVO

FOLHA 30 / 39

FORMATO A3


PROJETO RESIDENCIAL

CLIENTE KATIA

ASSUNTO ILUMINAÇÃO

SIMÕES Arquitetura & Design de Interiores
EMAIL: ARQUITETURA@SIMOESARQUITETURA.COM.BR
INSTAGRAM: @SIMOESARQUITETURA

*VERIFICAR PONTOS EXISTENTE NO LOCAL E ADEQUAR CONFORME NECESSÁRIO

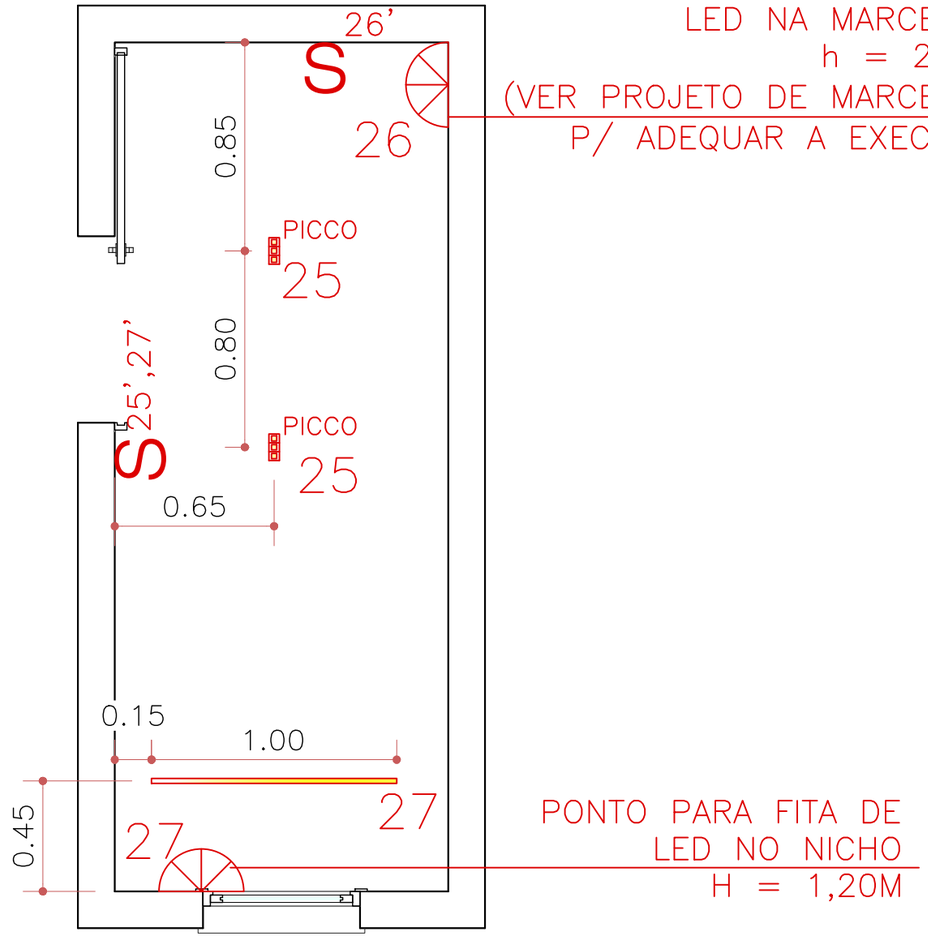

PONTO PARA FITA DE LED NA MARCENARIA h = 2,00 M (VER PROJETO DE MARCENARIA P/ ADEQUAR A EXECUÇÃO)

PONTO PARA FITA DE LED NO NICHO H = 1,20M

ILUMINAÇÃO – BANHO 02

ESC. 1:25

OBSERVAÇÕES
- COTAS EM METROS;
- COTAS DE NÍVEL EM METROS;
- CONFERIR MEDIDAS, ABERTURAS, NÍVEIS E PRUMOS NO LOCAL;
- MEDIDAS EM COTA PREVALECEM SOBRE O DESENHO;
- ESSA PRANCHA DEVE SER IMPRESSA COLORIDA;
- É RESPONSABILIDADE DO FORNECEDOR MEDIR E AJUSTAR O PROJETO;
- INSTALAR PENDENTES APÓS A INSTALAÇÃO DE MÓVEIS E MARCENARIA;

DATA 08/09/2026 | DESENHO REV00

RESPONSÁVEL FERNANDA SUELLEM SIMÕES LIMA

LOCAL R. **QUADRA B, LOTE 11 – CONDOMÍNIO HEVETIA PARK**

ESCALA **INDICADA** | COD. DO PROJETO **0000**

CIDADE INDAIATUBA– SP

FASE EXECUTIVO

FOLHA 31 / 39

FORMATO A3

PROJETO RESIDENCIAL


CLIENTE **KATIA**

ASSUNTO ILUMINAÇÃO

EMAIL: ARQUITETURA@SIMOESARQUITETURA.COM.BR
INSTAGRAM: @SIMOESARQUITETURA

*VERIFICAR PONTOS EXISTENTE NO LOCAL E ADEQUAR CONFORME NECESSÁRIO

TOMADAS – GARAGEM
ESC. 1:50

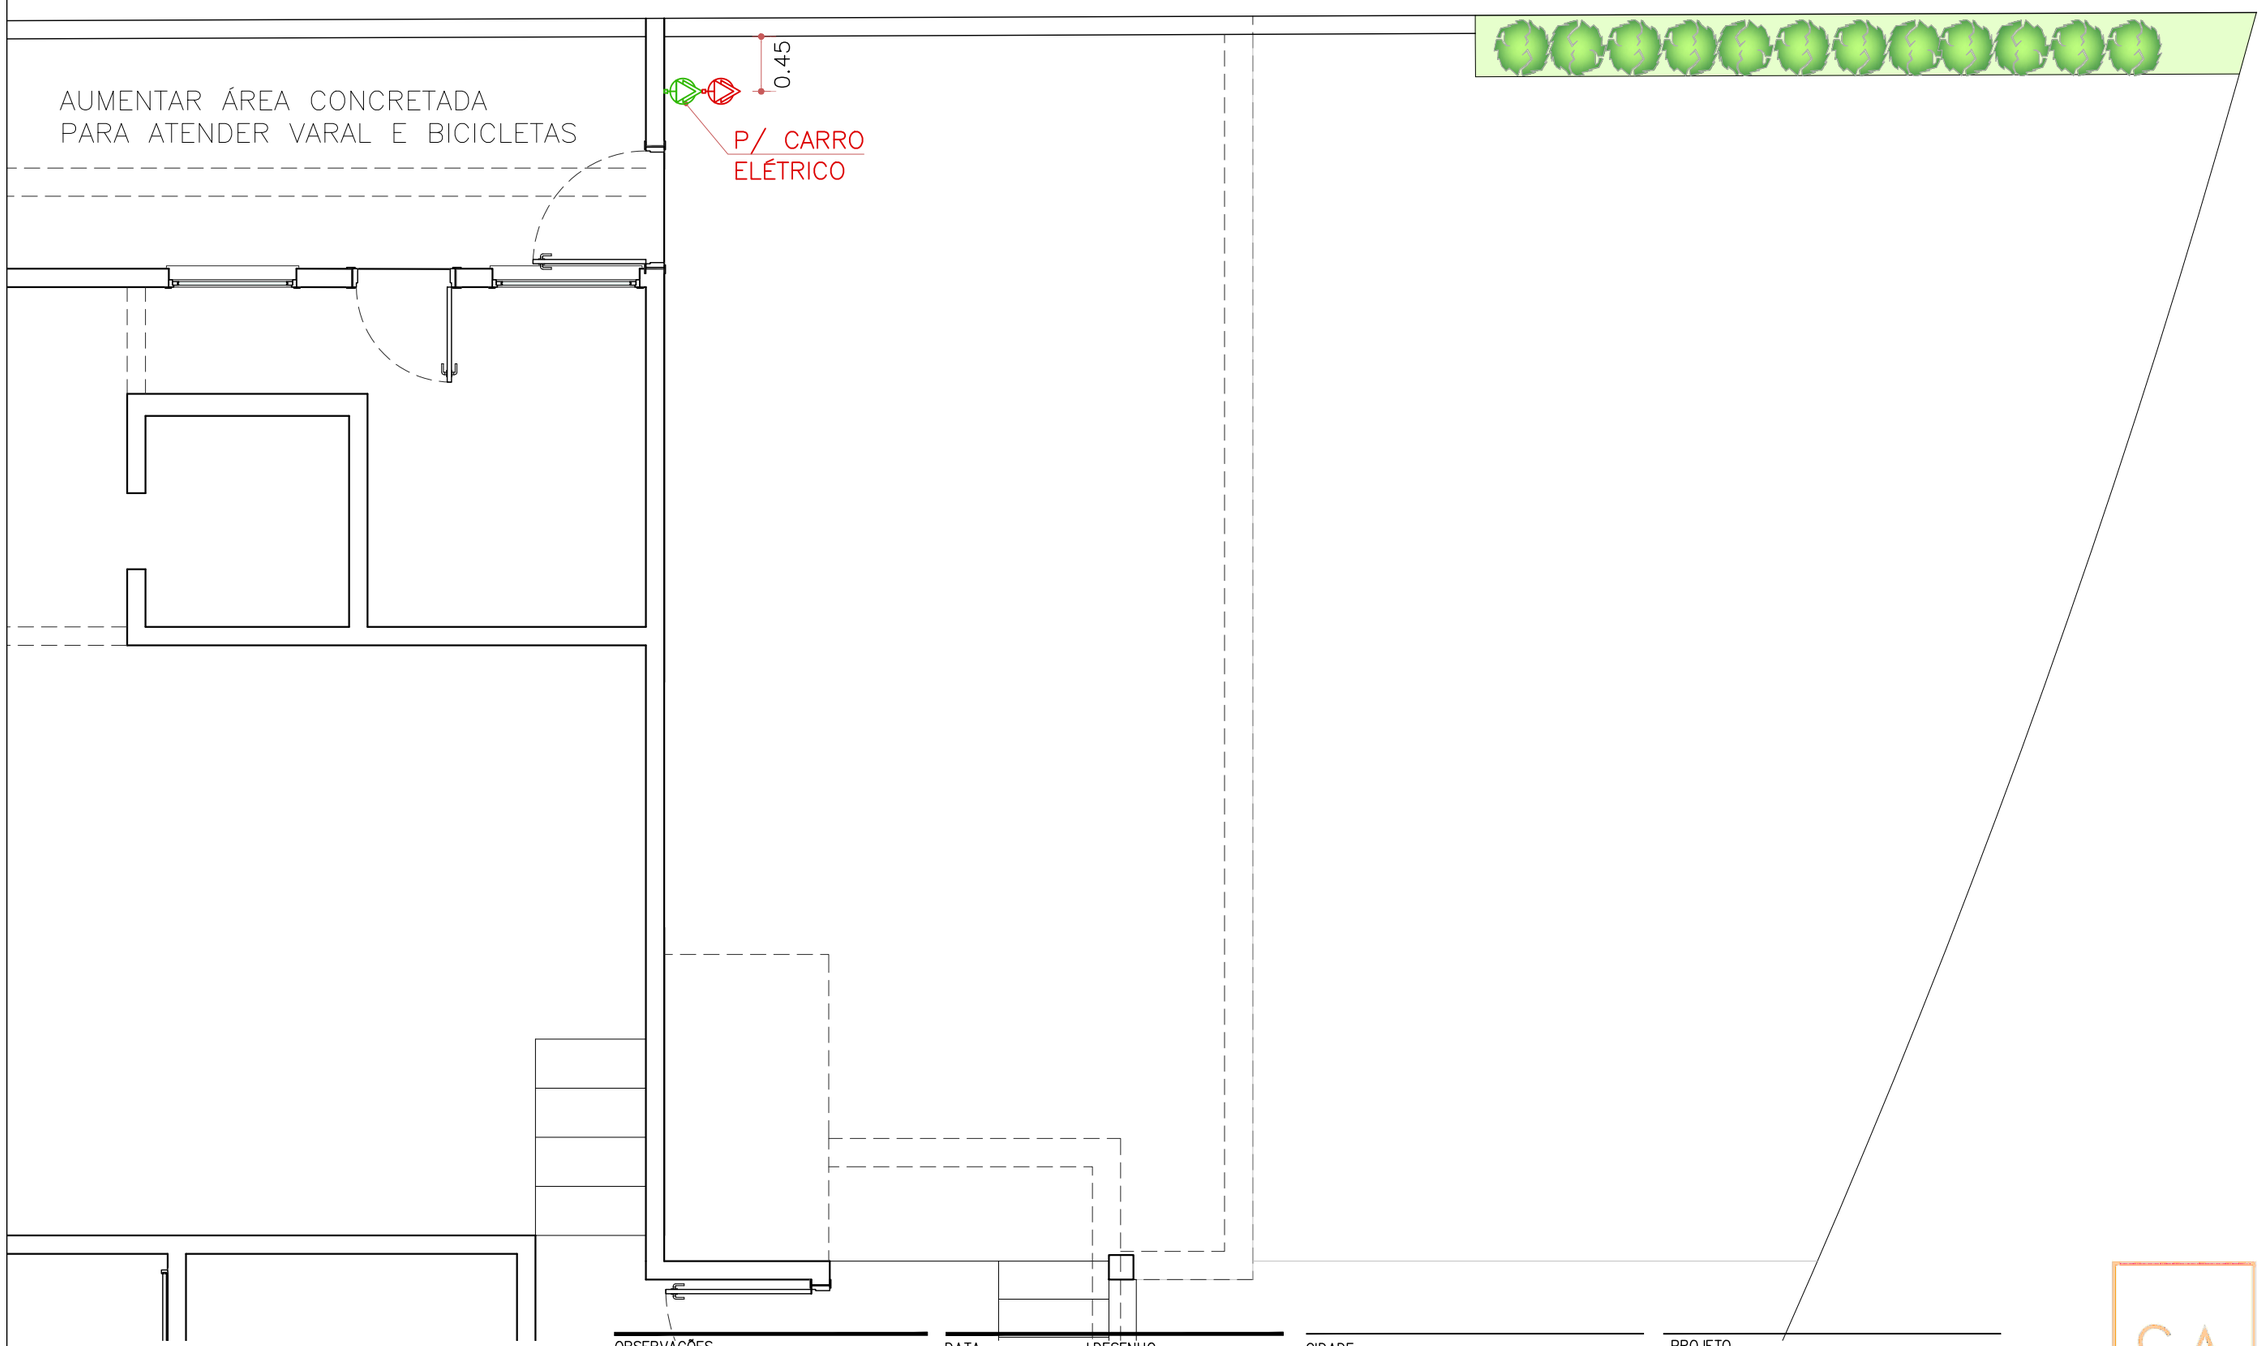

OBSERVAÇÕES
- COTAS EM METROS;
- COTAS DE NÍVEL EM METROS;
- CONFERIR MEDIDAS, ABERTURAS, NÍVEIS E PRUMOS NO LOCAL;
- MEDIDAS EM COTA PREVALECEM SOBRE O DESENHO;
- ESSA PRANCHA DEVE SER IMPRESSA COLORIDA;
- É RESPONSABILIDADE DO FORNECEDOR MEDIR E AJUSTAR O PROJETO;
- INSTALAR PENDENTES APÓS A INSTALAÇÃO DE MÓVEIS E MARCENARIA;

DATA: 08/09/2026 | DESENHO: REV00

RESPONSÁVEL: FERNANDA SUELLEM SIMÕES LIMA

LOCAL: R. **QUADRA B, LOTE 11 – CONDOMÍNIO HEVETIA PARK**

ESCALA: **INDICADA** | COD. DO PROJETO: **0000**

CIDADE: INDAIATUBA– SP

FASE: EXECUTIVO

FOLHA: 32 / 39

FORMATO: A3


PROJETO: RESIDENCIAL

CLIENTE: **KATIA**

ASSUNTO: TOMADAS

SIMÕES Arquitetura & Design de Interiores
EMAIL: ARQUITETURA@SIMOESARQUITETURA.COM.BR
INSTAGRAM: @SIMOESARQUITETURA

*VERIFICAR PONTOS EXISTENTE NO LOCAL E ADEQUAR CONFORME NECESSÁRIO

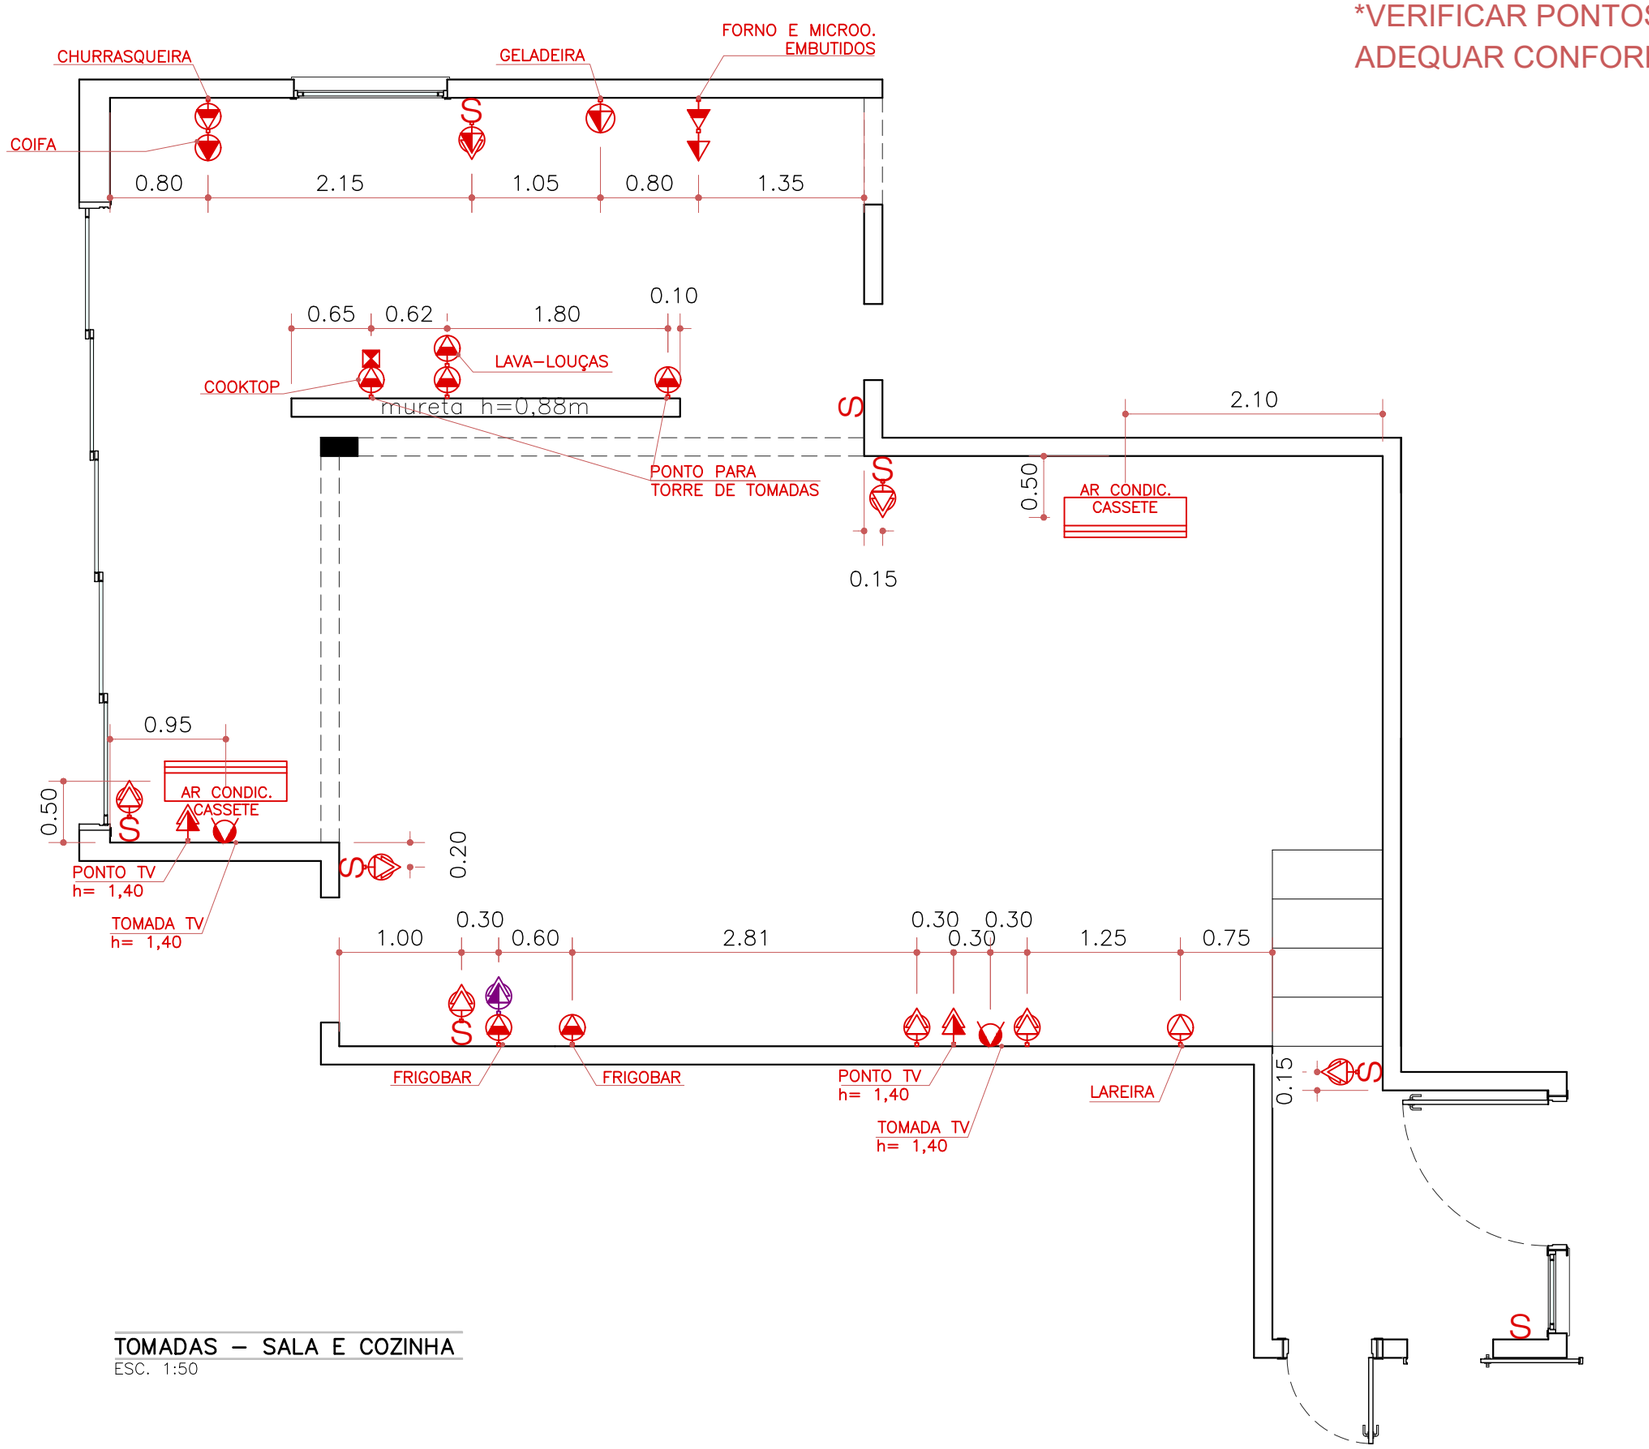

TOMADAS – SALA E COZINHA

ESC. 1:50

OBSERVAÇÕES

- COTAS EM METROS;
- COTAS DE NÍVEL EM METROS;
- CONFERIR MEDIDAS, ABERTURAS, NÍVEIS E PRUMOS NO LOCAL;
- MEDIDAS EM COTA PREVALECEM SOBRE O DESENHO;
- ESSA PRANCHA DEVE SER IMPRESSA COLORIDA;
- É RESPONSABILIDADE DO FORNECEDOR MEDIR E AJUSTAR O PROJETO;
- INSTALAR PENDENTES APÓS A INSTALAÇÃO DE MÓVEIS E MARCENARIA;

DATA 08/09/2026 | DESENHO REV00

RESPONSÁVEL FERNANDA SUELLEM SIMÕES LIMA

LOCAL R. **QUADRA B, LOTE 11 – CONDOMÍNIO HEVETIA PARK**

ESCALA **INDICADA** | COD. DO PROJETO **0000**

CIDADE INDAIATUBA– SP

FASE EXECUTIVO

FOLHA 33 / 39

FORMATO A3


PROJETO RESIDENCIAL

CLIENTE **KATIA**

ASSUNTO TOMADAS

SIMÕES Arquitetura & Design de Interiores
EMAIL: ARQUITETURA@SIMOESARQUITETURA.COM.BR
INSTAGRAM: @SIMOESARQUITETURA

*VERIFICAR PONTOS EXISTENTE NO LOCAL E ADEQUAR CONFORME NECESSÁRIO

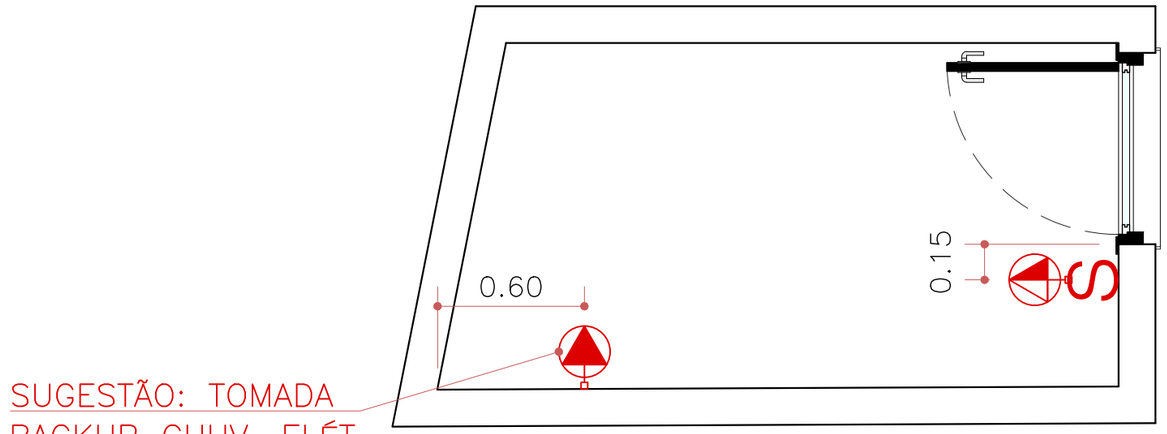

TOMADAS – BANHO EXTERNO

ESC. 1:25

OBSERVAÇÕES
- COTAS EM METROS;
- COTAS DE NÍVEL EM METROS;
- CONFERIR MEDIDAS, ABERTURAS, NÍVEIS E PRUMOS NO LOCAL;
- MEDIDAS EM COTA PREVALECEM SOBRE O DESENHO;
- ESSA PRANCHA DEVE SER IMPRESSA COLORIDA;
- É RESPONSABILIDADE DO FORNECEDOR MEDIR E AJUSTAR O PROJETO;
- INSTALAR PENDENTES APÓS A INSTALAÇÃO DE MÓVEIS E MARCENARIA;

DATA 08/09/2026 | DESENHO REV00

RESPONSÁVEL FERNANDA SUELLEM SIMÕES LIMA

LOCAL R. QUADRA B, LOTE 11 – CONDOMÍNIO HEVETIA PARK

ESCALA INDICADA | COD. DO PROJETO 0000

CIDADE INDAIATUBA– SP

FASE EXECUTIVO

FOLHA 34 / 39

FORMATO A3


PROJETO RESIDENCIAL

CLIENTE KATIA

ASSUNTO TOMADAS

SIMÕES Arquitetura & Design de Interiores
EMAIL: ARQUITETURA@SIMOESARQUITETURA.COM.BR
INSTAGRAM: @SIMOESARQUITETURA

*VERIFICAR PONTOS EXISTENTE NO LOCAL E
ADEQUAR CONFORME NECESSÁRIO

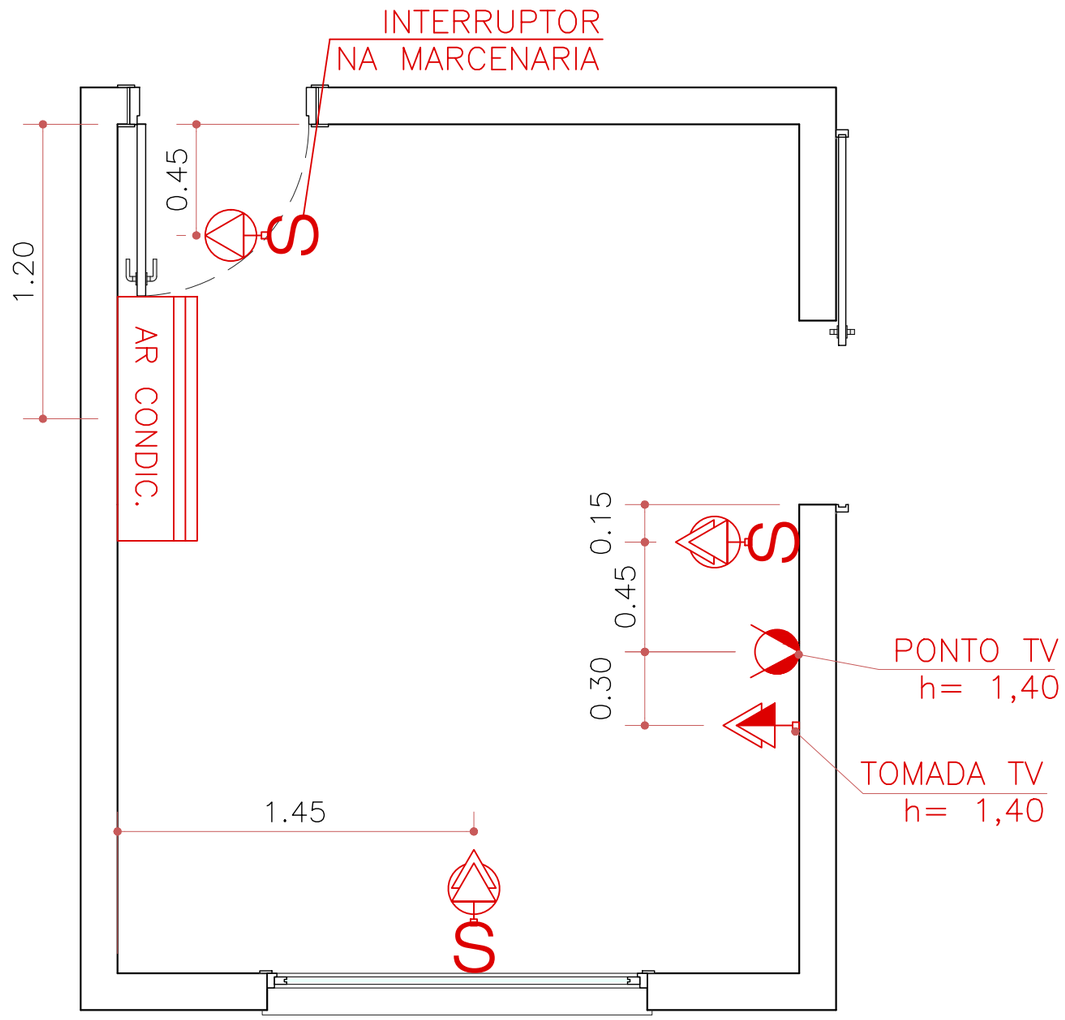

TOMADAS – SUÍTE 01

ESC. 1:25

OBSERVAÇÕES
- COTAS EM METROS;
- COTAS DE NÍVEL EM METROS;
- CONFERIR MEDIDAS, ABERTURAS, NÍVEIS E PRUMOS NO LOCAL;
- MEDIDAS EM COTA PREVALECEM SOBRE O DESENHO;
- ESSA PRANCHA DEVE SER IMPRESSA COLORIDA;
- É RESPONSABILIDADE DO FORNECEDOR MEDIR E AJUSTAR O PROJETO;
- INSTALAR PENDENTES APÓS A INSTALAÇÃO DE MÓVEIS E MARCENARIA;

DATA 08/09/2026 | DESENHO REV00

RESPONSÁVEL FERNANDA SUELLEM SIMÕES LIMA

LOCAL R. QUADRA B, LOTE 11 – CONDOMÍNIO HEVETIA PARK

ESCALA INDICADA | COD. DO PROJETO 0000

CIDADE INDAIATUBA– SP

FASE EXECUTIVO

FOLHA 35 / 39

FORMATO A3


PROJETO RESIDENCIAL

CLIENTE KATIA

ASSUNTO TOMADAS

SIMÕES Arquitetura & Design de Interiores
EMAIL: ARQUITETURA@SIMOESARQUITETURA.COM.BR
INSTAGRAM: @SIMOESARQUITETURA

*VERIFICAR PONTOS EXISTENTE NO LOCAL E
ADEQUAR CONFORME NECESSÁRIO

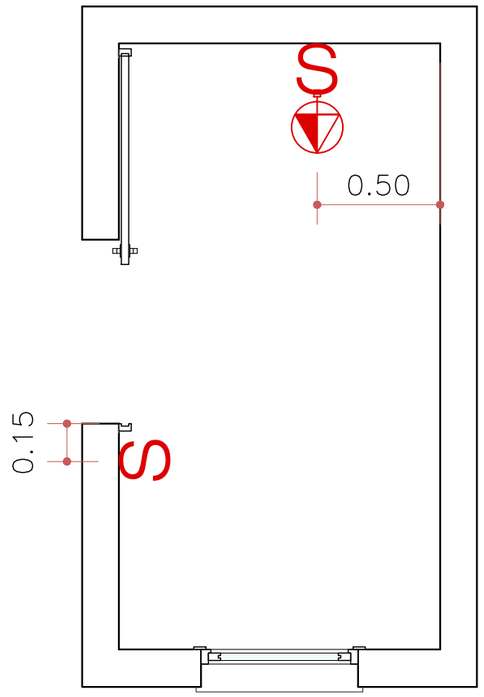

TOMADAS – BANHO 01

ESC. 1:25

OBSERVAÇÕES
- COTAS EM METROS;
- COTAS DE NÍVEL EM METROS;
- CONFERIR MEDIDAS, ABERTURAS, NÍVEIS E PRUMOS NO LOCAL;
- MEDIDAS EM COTA PREVALECEM SOBRE O DESENHO;
- ESSA PRANCHA DEVE SER IMPRESSA COLORIDA;
- É RESPONSABILIDADE DO FORNECEDOR MEDIR E AJUSTAR O PROJETO;
- INSTALAR PENDENTES APÓS A INSTALAÇÃO DE MÓVEIS E MARCENARIA;

DATA 08/09/2026 | DESENHO REV00

RESPONSÁVEL FERNANDA SUELLEM SIMÕES LIMA

LOCAL R. **QUADRA B, LOTE 11 – CONDOMÍNIO HEVETIA PARK**

ESCALA **INDICADA** | COD. DO PROJETO **0000**

CIDADE INDAIATUBA– SP

FASE EXECUTIVO

FOLHA 36 / 39

FORMATO A3


PROJETO RESIDENCIAL

CLIENTE **KATIA**

ASSUNTO TOMADAS

SIMÕES Arquitetura & Design de Interiores
EMAIL: ARQUITETURA@SIMOESARQUITETURA.COM.BR
INSTAGRAM: @SIMOESARQUITETURA

*VERIFICAR PONTOS EXISTENTE NO LOCAL E ADEQUAR CONFORME NECESSÁRIO

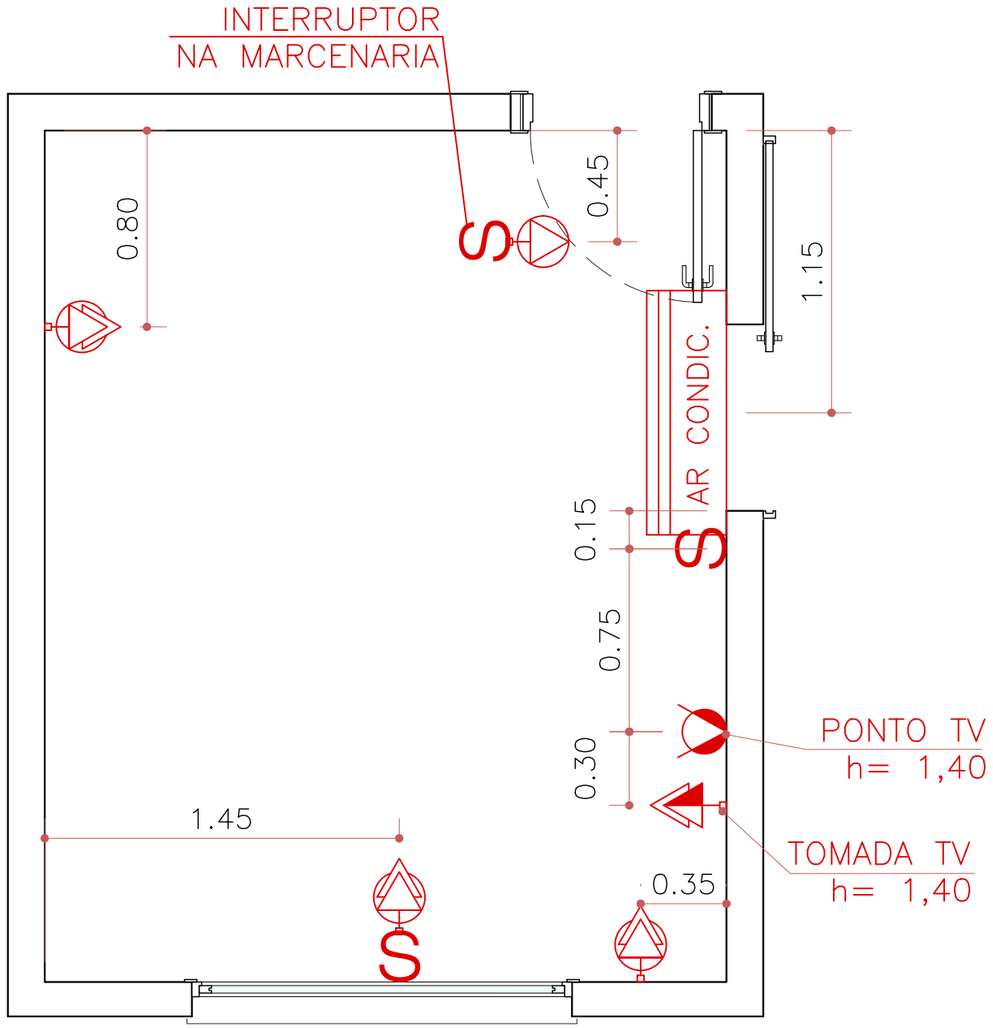

TOMADAS – SUÍTE 02

ESC. 1:25

OBSERVAÇÕES
- COTAS EM METROS;
- COTAS DE NÍVEL EM METROS;
- CONFERIR MEDIDAS, ABERTURAS, NÍVEIS E PRUMOS NO LOCAL;
- MEDIDAS EM COTA PREVALECEM SOBRE O DESENHO;
- ESSA PRANCHA DEVE SER IMPRESSA COLORIDA;
- É RESPONSABILIDADE DO FORNECEDOR MEDIR E AJUSTAR O PROJETO;
- INSTALAR PENDENTES APÓS A INSTALAÇÃO DE MÓVEIS E MARCENARIA;

DATA 08/09/2026 | DESENHO REV00

RESPONSÁVEL FERNANDA SUELLEM SIMÕES LIMA

LOCAL R. QUADRA B, LOTE 11 – CONDOMÍNIO HEVETIA PARK

ESCALA INDICADA | COD. DO PROJETO 0000

CIDADE INDAIATUBA– SP

FASE EXECUTIVO

FOLHA 37 / 39

FORMATO A3


PROJETO RESIDENCIAL

CLIENTE KATIA

ASSUNTO TOMADAS

SIMÕES Arquitetura & Design de Interiores
EMAIL: ARQUITETURA@SIMOESARQUITETURA.COM.BR
INSTAGRAM: @SIMOESARQUITETURA

*VERIFICAR PONTOS EXISTENTE NO LOCAL E ADEQUAR CONFORME NECESSÁRIO

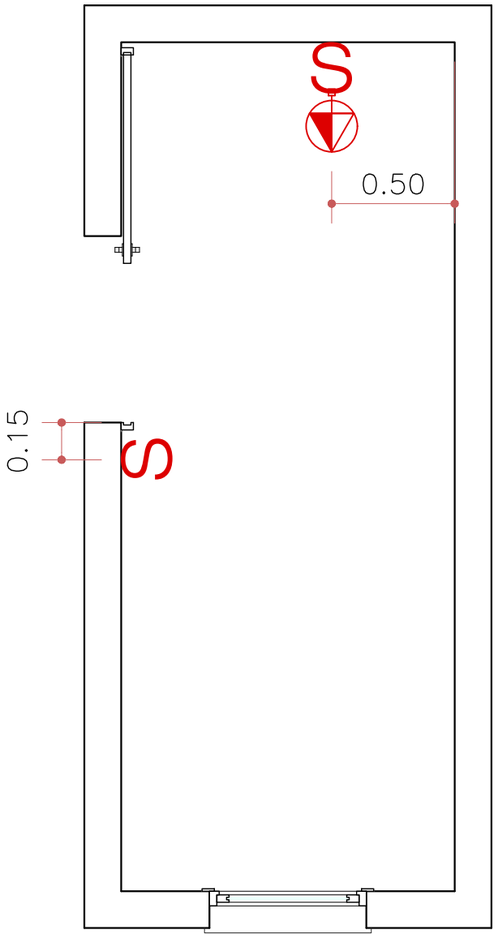

TOMADAS – BANHO 02

ESC. 1:25

OBSERVAÇÕES
- COTAS EM METROS;
- COTAS DE NÍVEL EM METROS;
- CONFERIR MEDIDAS, ABERTURAS, NÍVEIS E PRUMOS NO LOCAL;
- MEDIDAS EM COTA PREVALECEM SOBRE O DESENHO;
- ESSA PRANCHA DEVE SER IMPRESSA COLORIDA;
- É RESPONSABILIDADE DO FORNECEDOR MEDIR E AJUSTAR O PROJETO;
- INSTALAR PENDENTES APÓS A INSTALAÇÃO DE MÓVEIS E MARCENARIA;

DATA: 08/09/2026 | DESENHO: REV00

RESPONSÁVEL: FERNANDA SUELLEM SIMÕES LIMA

LOCAL: R. QUADRA B, LOTE 11 – CONDOMÍNIO HEVETIA PARK

ESCALA: INDICADA | COD. DO PROJETO: 0000

CIDADE: INDAIATUBA– SP

FASE: EXECUTIVO

FOLHA: 38 / 39

FORMATO: A3

PROJETO: RESIDENCIAL

CLIENTE: KATIA

ASSUNTO: TOMADAS

SIMÕES Arquitetura & Design de Interiores
EMAIL: ARQUITETURA@SIMOESARQUITETURA.COM.BR
INSTAGRAM: @SIMOESARQUITETURA


161





