


A piscina nova está deslocada

Sobreposição pelas divisas do terreno. Contornos internos cotados + paredes de 20 cm para fora.

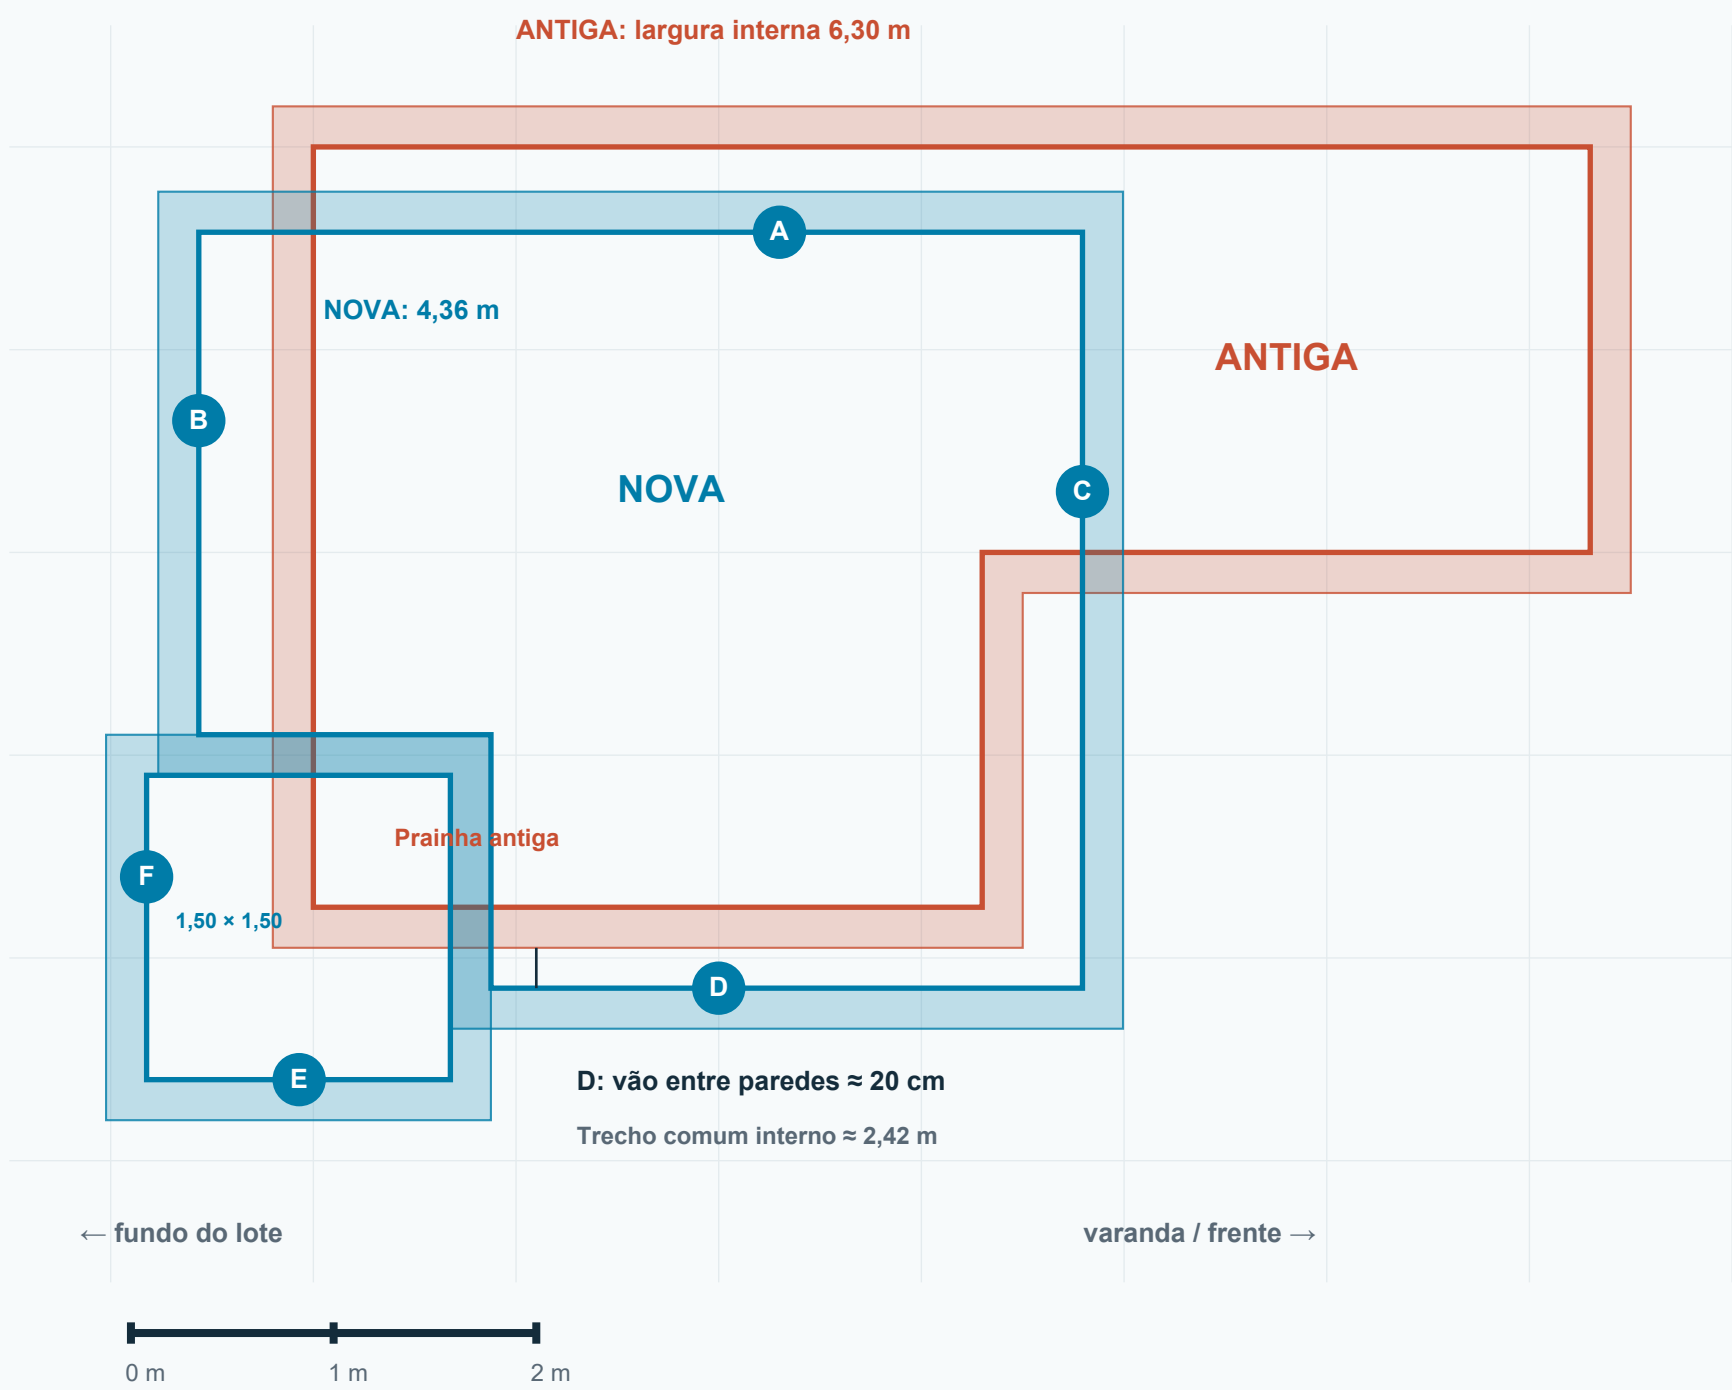

NENHUMA PAREDE PRINCIPAL COINCIDE

- A** Topo / divisa superior
≈ 42 cm em direção à suíte
- B** Lateral esquerda principal
≈ 57 cm em direção ao fundo do lote
- C** Lateral direita principal
≈ 2,50 m em direção ao fundo do lote
- D** Base principal × prainha antiga
≈ 40 cm em direção à suíte
- E** Base do quadrado de 1,50 m
≈ 85 cm em direção à suíte
- F** Esquerda do quadrado de 1,50 m
≈ 82 cm em direção ao fundo do lote

O QUE SIGNIFICAM OS 20 CM


As faixas coloridas representam paredes adicionadas para fora da medida interna. Na comparação D, os 40 cm entre faces internas deixam cerca de 20 cm livres entre as paredes, no trecho comum.

A borda antiga desenhada tem cerca de 50 cm. Ela não foi confundida com parede estrutural de 50 cm.

Resultado de leitura gráfica, não levantamento de campo. Coincidência em planta não comprova possibilidade de reaproveitamento.

Sobreposição das imagens originais

Terracota = existente (PDF p.2 / folha 01). Azul = proposta (PDF p.5 / folha 04).

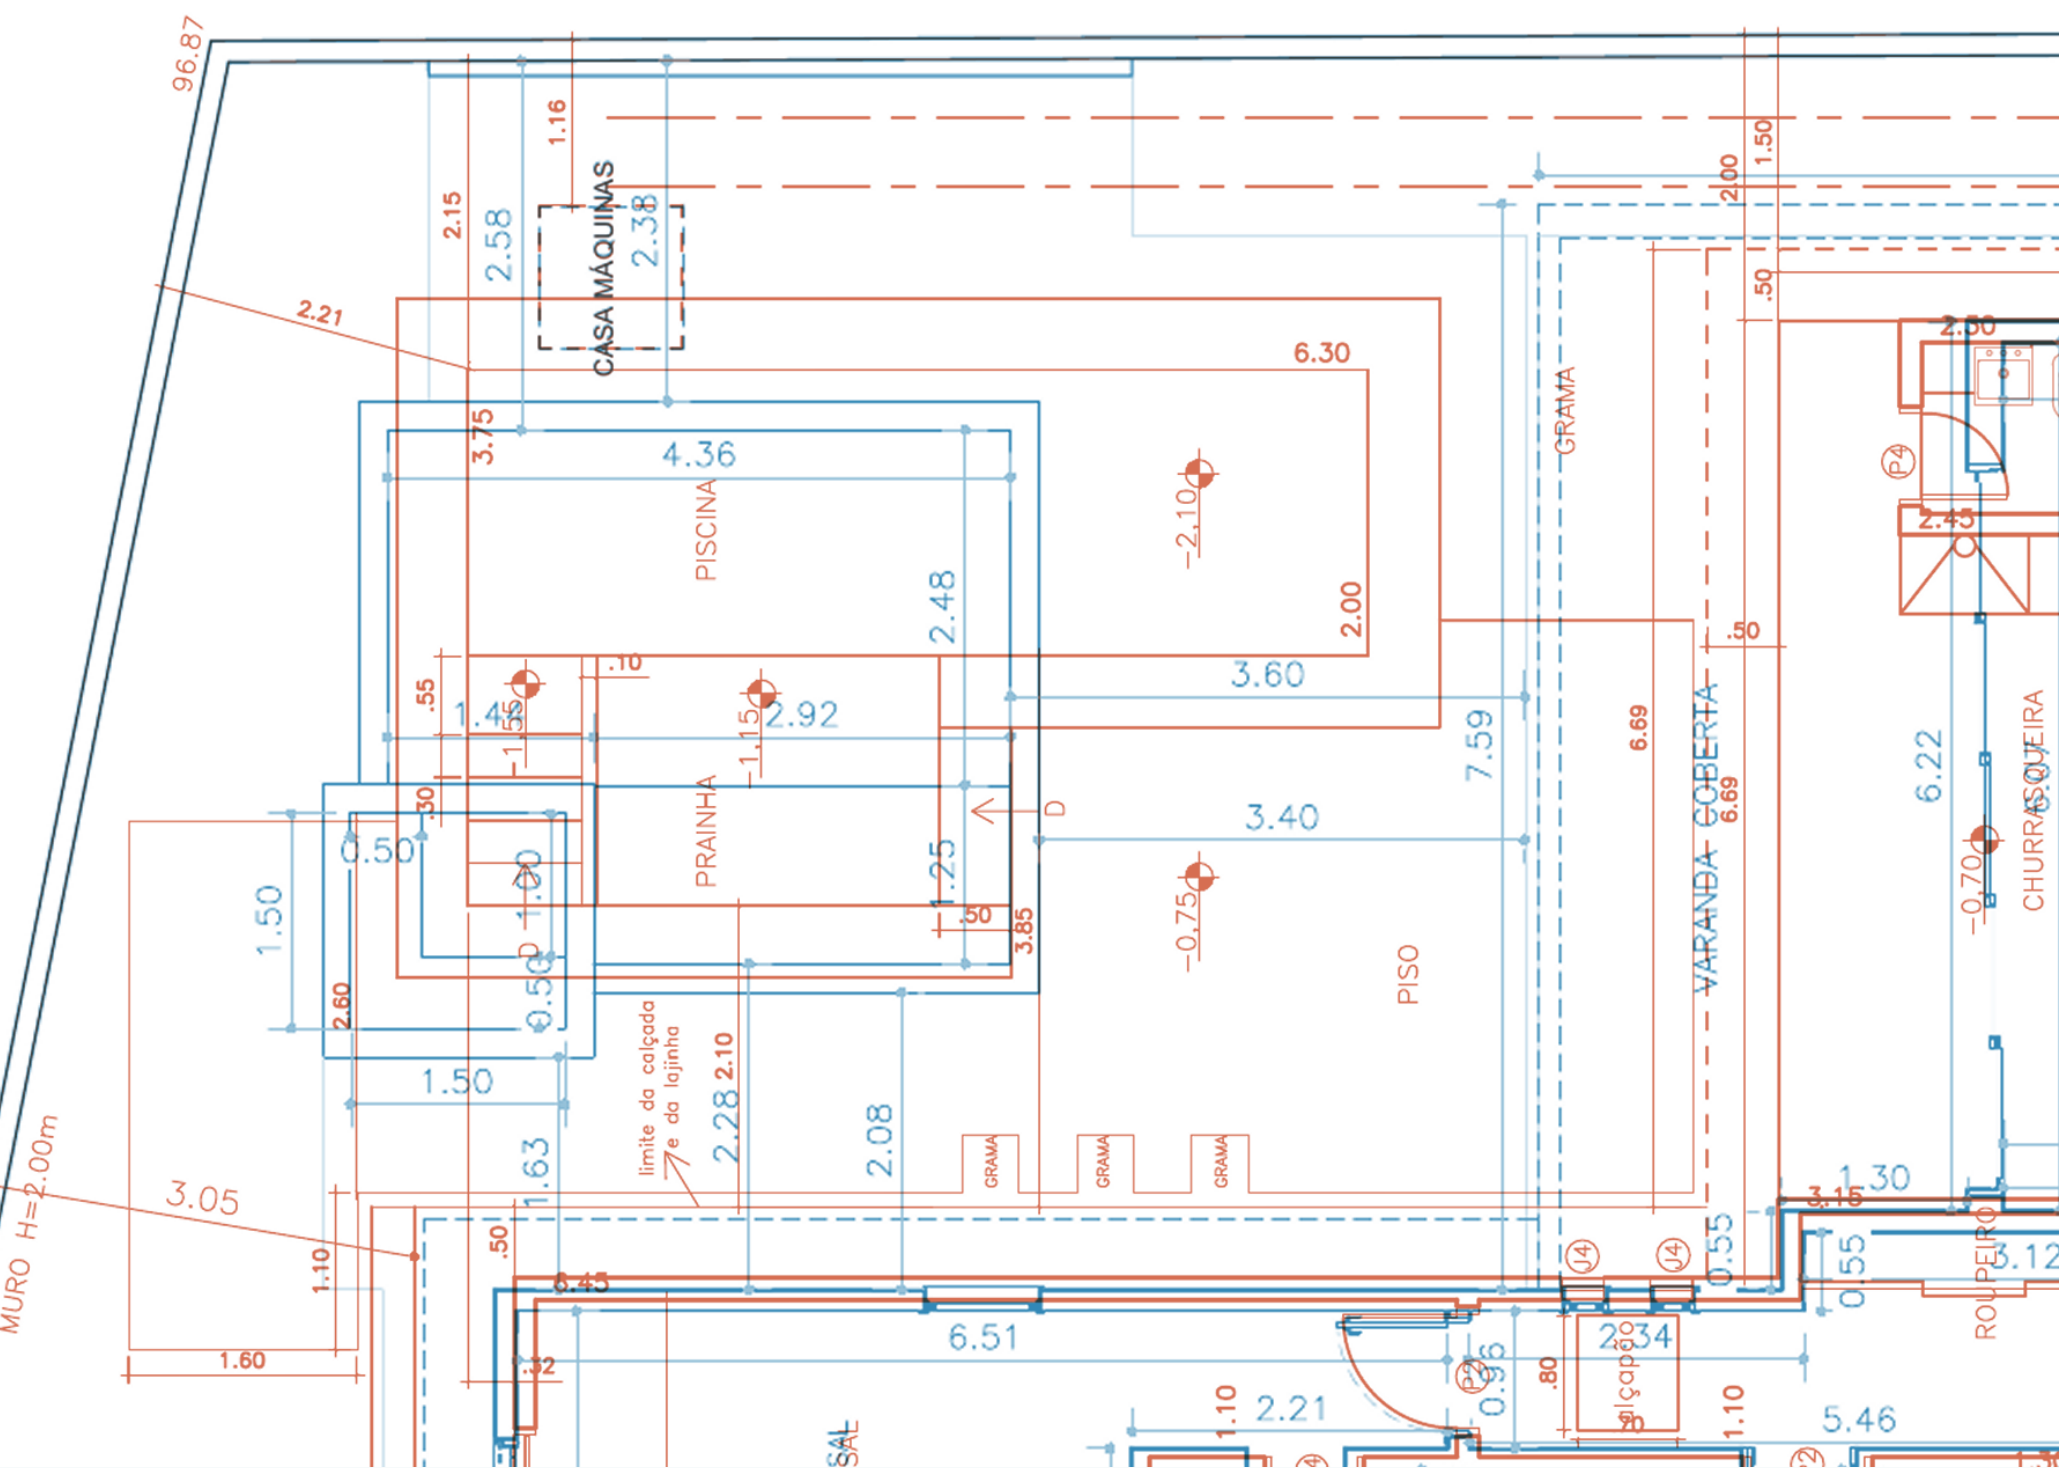

COMO FOI ALINHADO

1. Duas extremidades da divisa superior do lote alinham escala, posição e orientação das pranchas.
2. O canto inferior direito do lote foi usado como verificação independente e coincidiu a aproximadamente 3 mm na geometria do PDF.
3. As cotas internas 6,30 m (existente) e 4,36 m (nova) calibram a leitura. O detalhe da piscina, p.9 / folha 08, confirma a nova geometria e os 20 cm indicados.

DIVERGÊNCIA DA CASA

O canto da suíte não coincide entre desenhos: aproximadamente 13 cm na horizontal e 8 cm na vertical. Por isso, a casa não foi usada para forçar o encaixe das piscinas.

MEDIDAS INTERNAS

Antiga: 6,30 × 2,00 m no trecho principal; extensão de 3,30 × 1,75 m. Nova: 4,36 m de largura e 3,73 m de extensão máxima, com recorte; quadrado de 1,50 × 1,50 m.

A nova base principal fica 2,15 m além da base antiga do trecho de 2,00 m. A comparação D da primeira página usa a base da antiga prainha, que é a parede mais próxima.

Leitura das fontes e limites

Pranchas consultadas: p.2 existente, p.3 demolição, p.4 construção, p.5 planta baixa e p.9 detalhe da piscina. A posição relativa foi medida nos vetores do PDF, sem deslocar as piscinas para fazê-las coincidir. As cotas escritas prevalecem; o arredondamento ao centímetro é apenas apresentação do estudo.

Antes de definir demolição ou aproveitamento, conferir no local a implantação e a espessura real das paredes. O estudo não verifica fundação, armadura, impermeabilização ou condição da estrutura existente. Fontes originais preservadas.